
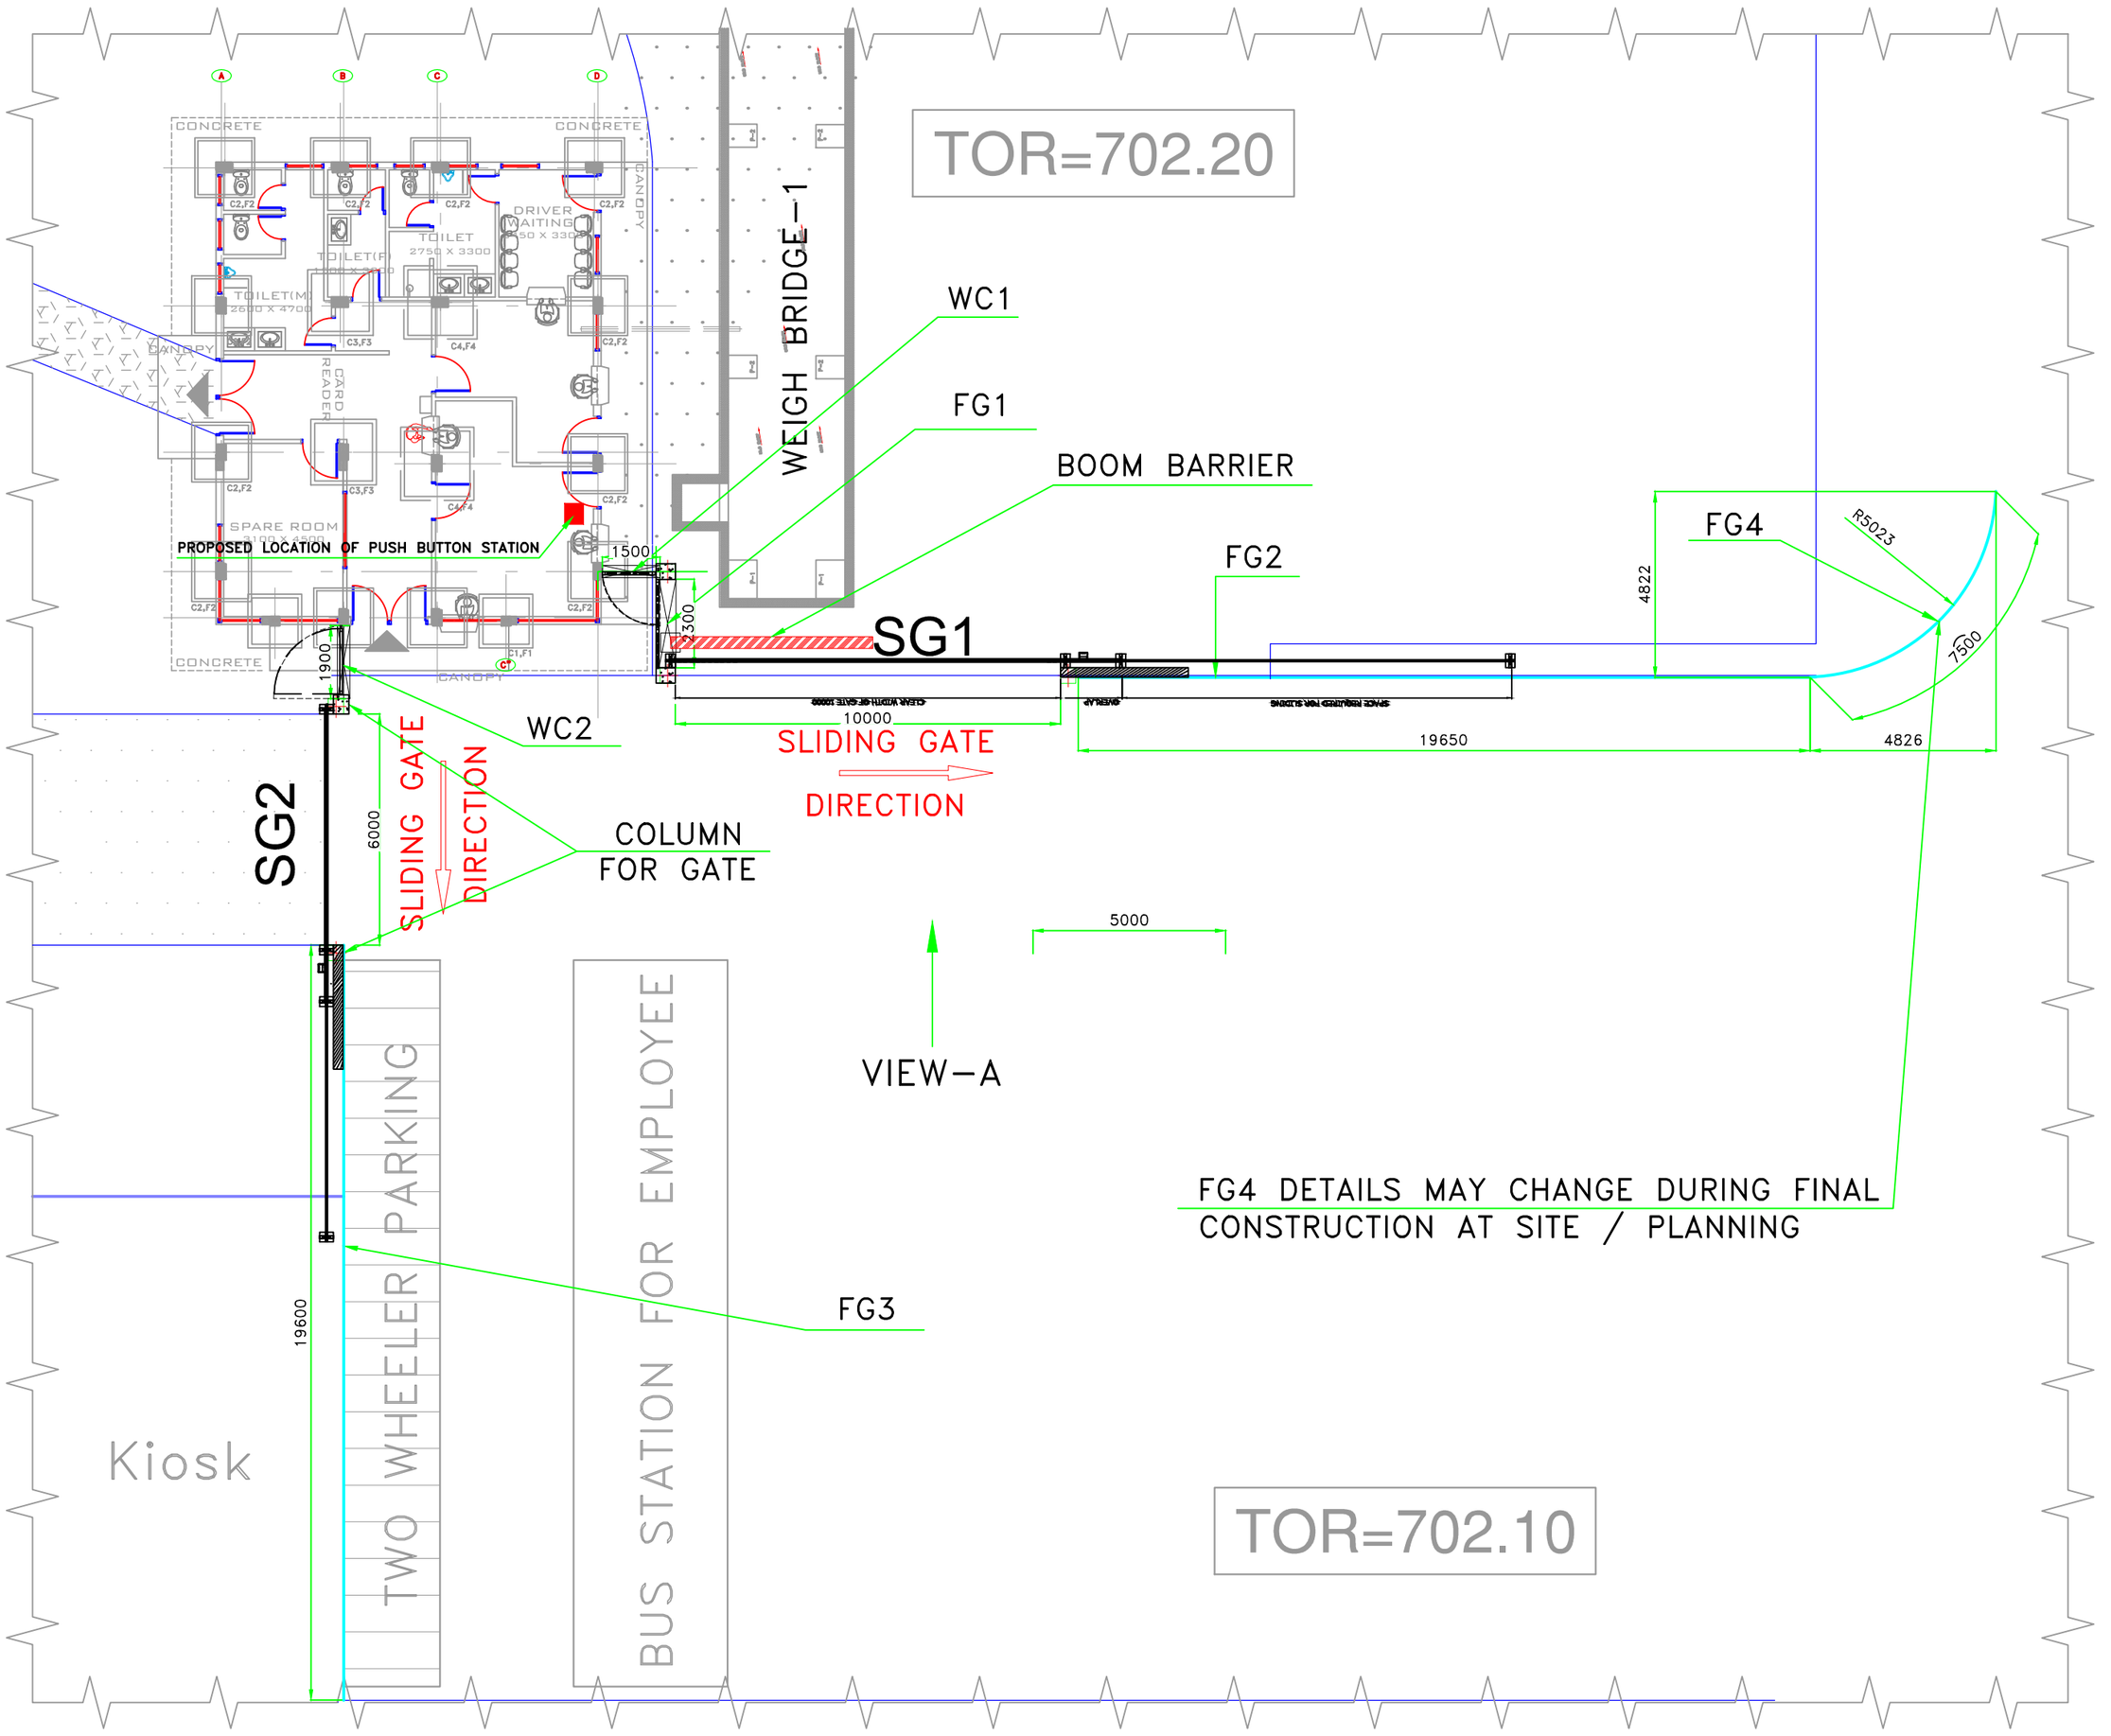


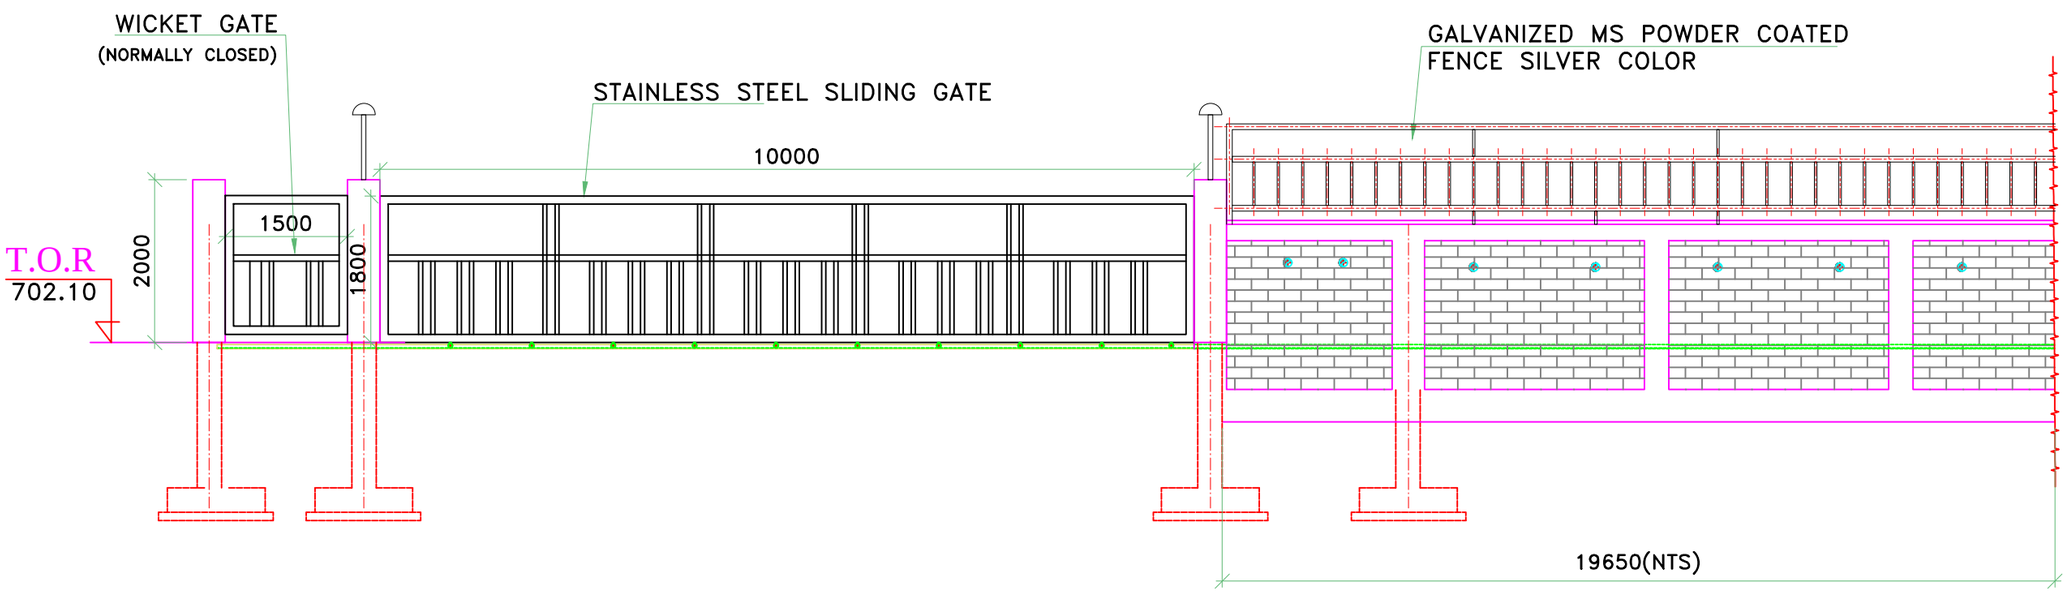

VIEW-AA
(SCALE:- 2:1)

NOTES:

1. ALL THE DIMENSIONS ARE IN MM UNLESS NOTED OTHERWISE
2. FOLLOW WRITTEN DIMENSIONS ONLY, DO NOT SCALE THE DRG.
3. ABOVE INFORMATION ARE ONLY FOR REFERENCE.
4. ALL CURVED FIXED FENCE (MARKED AS FG3 & FG4) SHALL BE AS PER THE FINAL SITE CONDITION. APPROVAL SHOULD BE TAKEN BEFORE FABRICATION.

REV. NO.	DATE	DESCRIPTION	BY	APPROVED
D	24.11.2014	BOOM BARRIER MARKED	GIRISH	V.K. JAIN
C	31.10.2014	GENERALLY REVISED	GIRISH	V.K. JAIN
B	14.10.2014	GENERALLY REVISED	GIRISH	V.K. JAIN
A	17.09.2014	GENERALLY REVISED	GIRISH	V.K. JAIN

REVISIONS

DO NOT SCALE IF IN DOUBT PLEASE ASK

THIS DRAWING IS THE PROPERTY OF ESPIC CONSULTING PRIVATE LIMITED. THIS MUST NOT BE COPIED OR REPRODUCED IN ANY MANNER OR DESIGN DISCLOSED OR PARTS MANUFACTURED THERE OF WITHOUT WRITTEN PERMISSION OF ESPIC CONSULTING PVT.LTD.

ESPIC
Engineering Solutions For Projects & Industrial Constructions

Espic Consulting Private Limited
3rd FLOOR, SAPPHIRE TWINS-RIGHT WING,
PU-3, SCHEME NO.54, AB ROAD, INDORE-452010 INDIA.

TITLE: ENTRANCE GATE & FENCE DETAILS

CLIENT	JSW MI STEEL SERVICE CENTER PVT. LTD. KHED CITY DIST.-PUNE (M.S.)	PROJECT	SERVICE CENTER
DRAWN BY	GIRISH	CHECKED BY	V.K. JAIN
APPROVED BY	D.K. JAIN		
DATE	11-09-14	SCALE	1:100
DRG NO.	323-A-020	SHEET	1 OF 2
SIZE	A1	REV.	D