

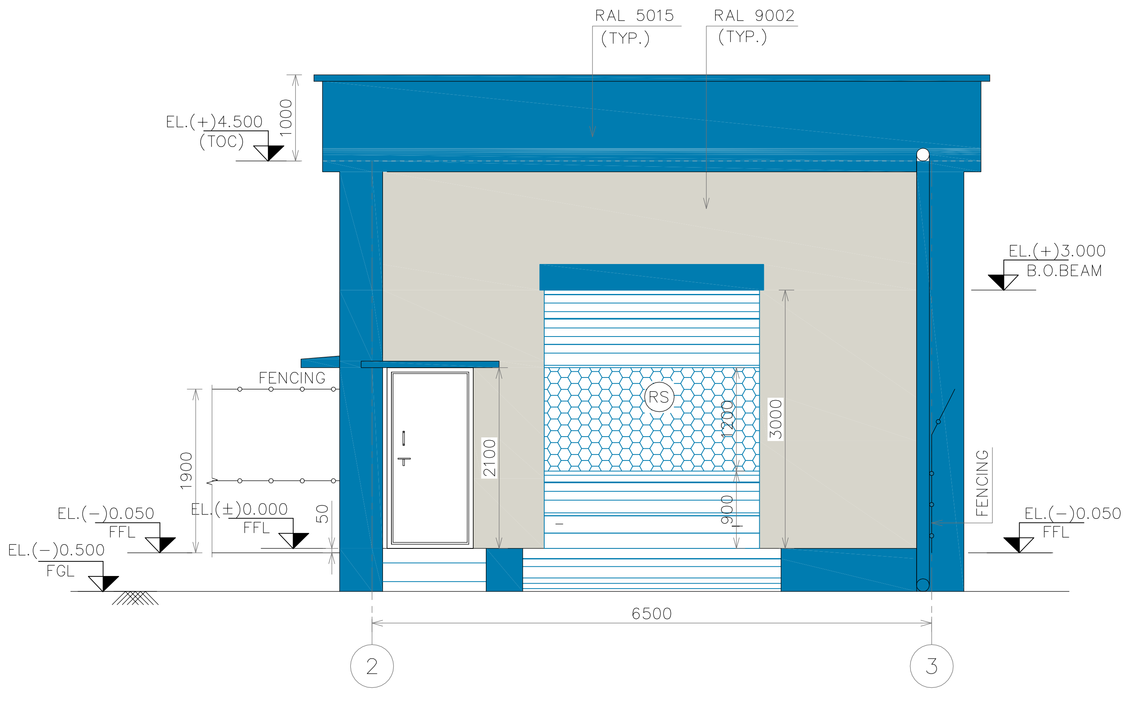



VIEW 1-1
1:50

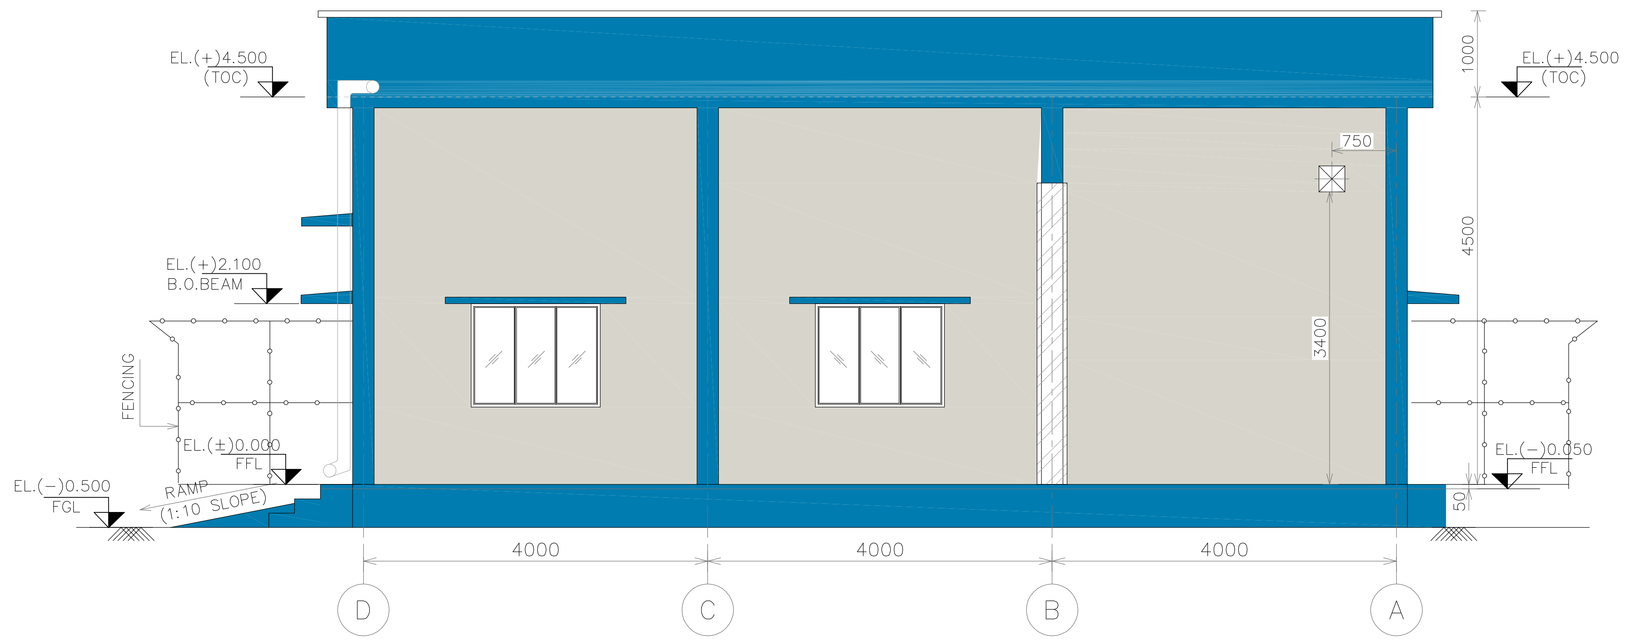


VIEW 2-2
1:50

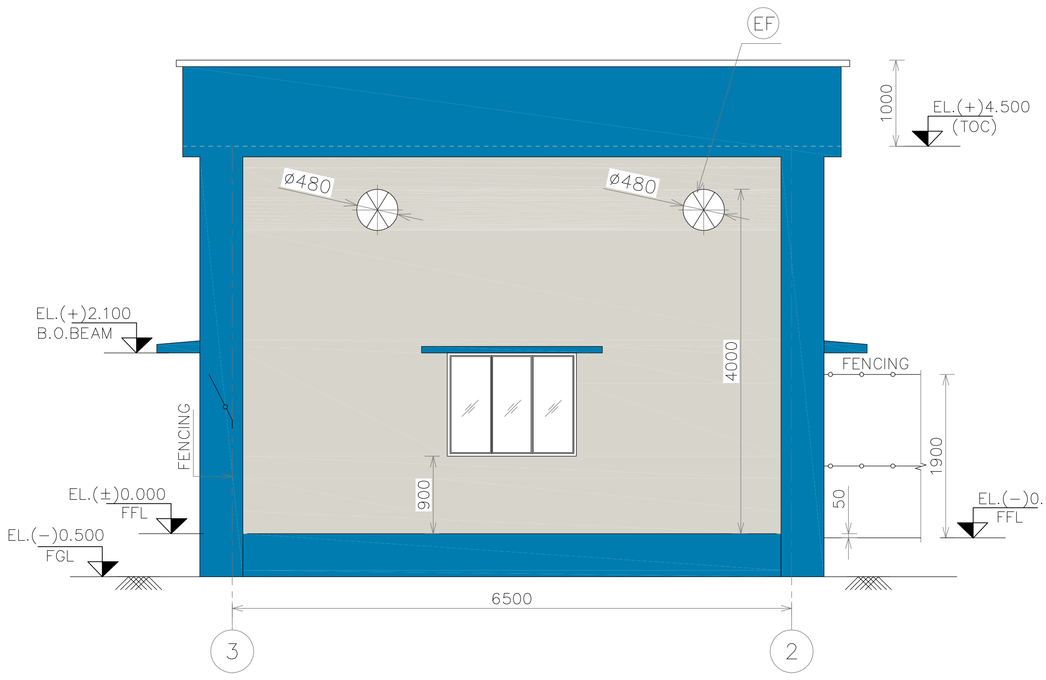

VIEW 3-3
1:50

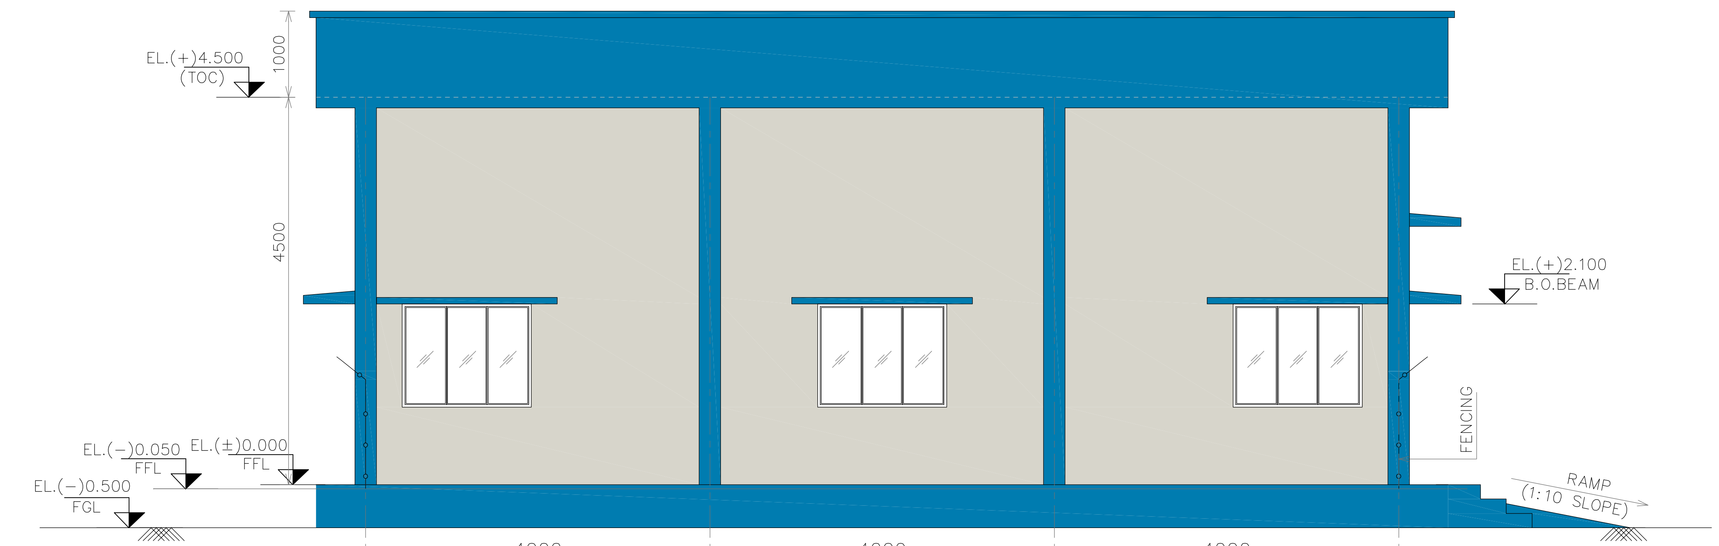

VIEW 4-4
1:50

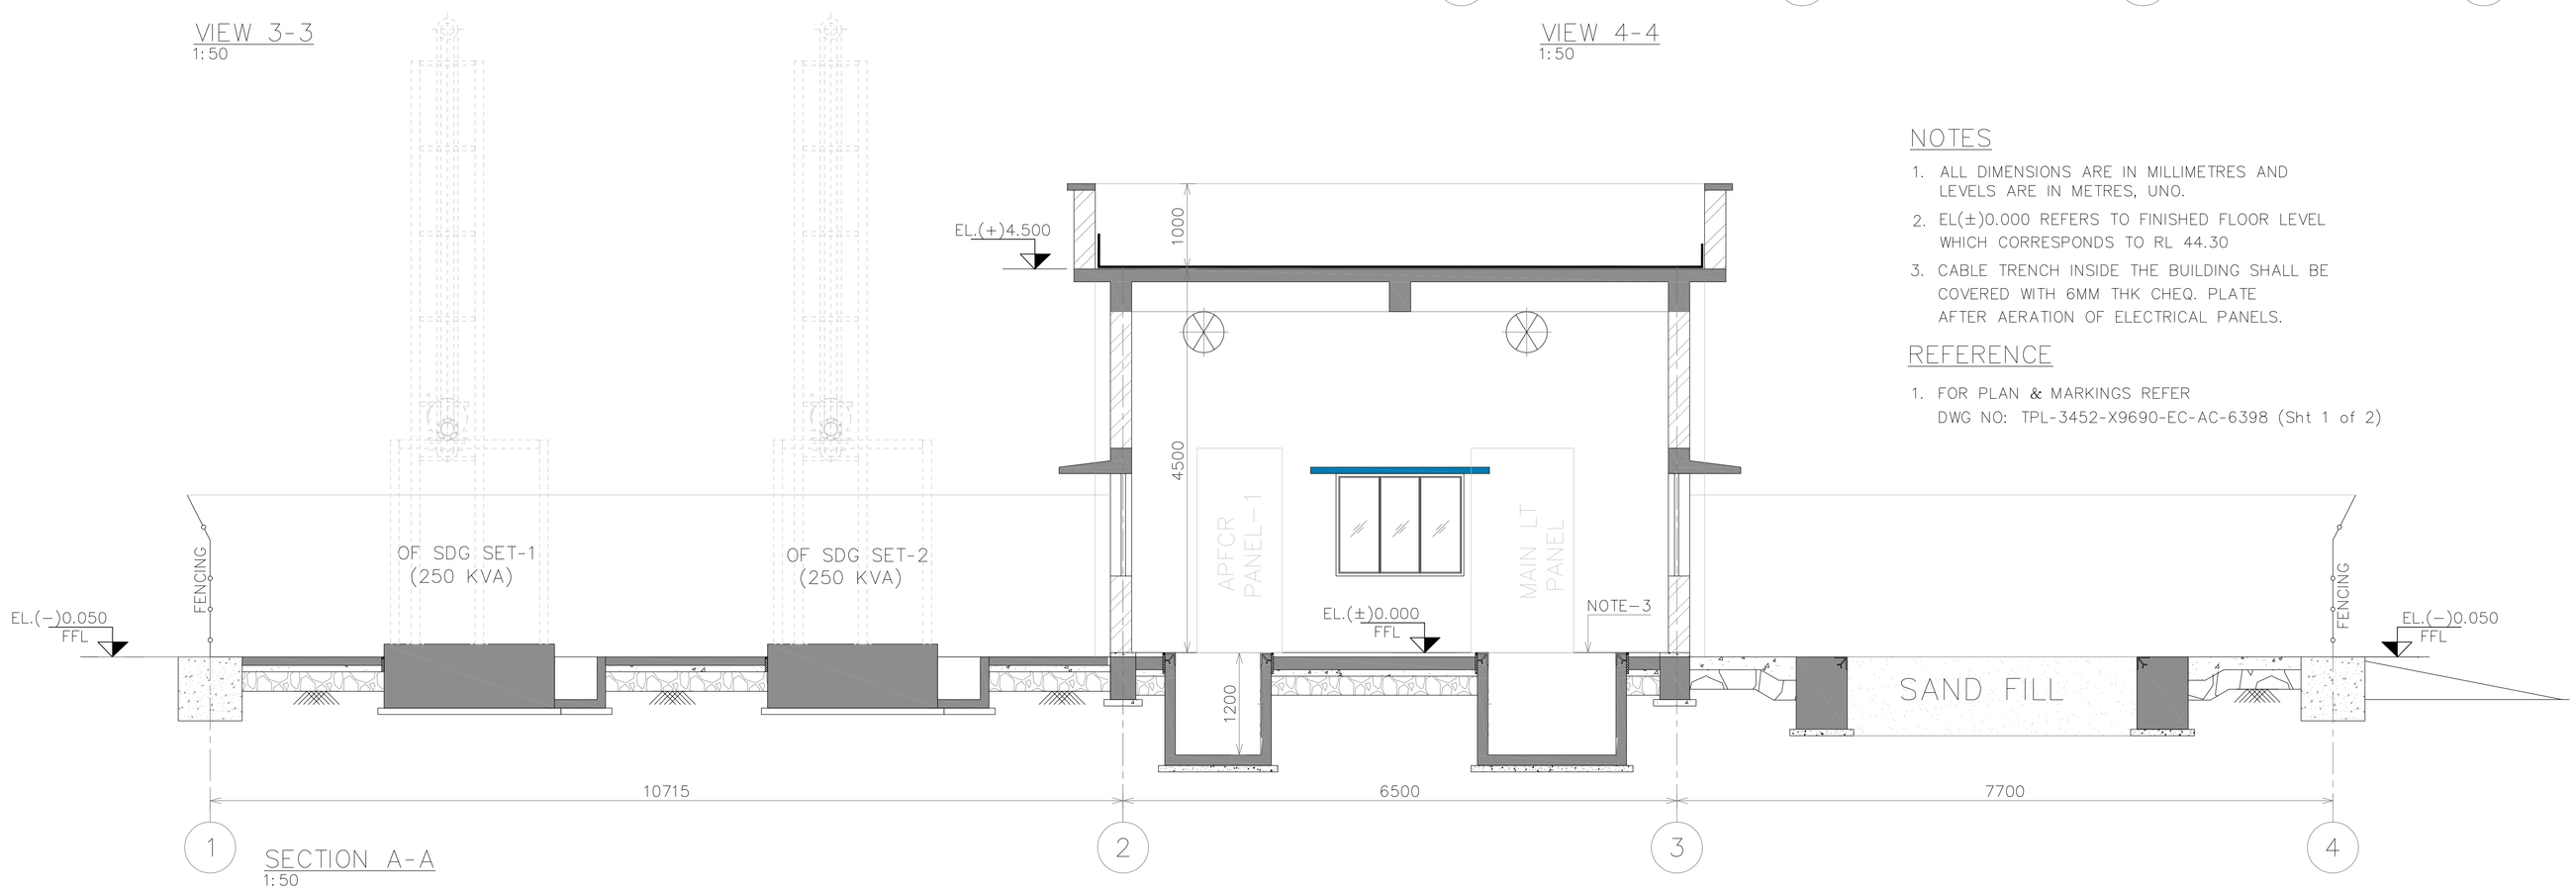

SECTION A-A
1:50

NOTES

1. ALL DIMENSIONS ARE IN MILLIMETRES AND LEVELS ARE IN METRES, UNO.
2. EL(±)0.000 REFERS TO FINISHED FLOOR LEVEL WHICH CORRESPONDS TO RL 44.30
3. CABLE TRENCH INSIDE THE BUILDING SHALL BE COVERED WITH 6MM THK CHEQ. PLATE AFTER AERATION OF ELECTRICAL PANELS.

REFERENCE

1. FOR PLAN & MARKINGS REFER DWG NO: TPL-3452-X9690-EC-AC-6398 (Sht 1 of 2)

REV.NO.	DATE	REVISION	CIVIL	MECH	ELEC	INST	APPD	DRAWN
			CLEARED					
1	03.03.17	ISSUED FOR CONSTRUCTION	NP				AS	GMN
0	14.02.17	ISSUED FOR APPROVAL	NP				AS	GMN

THIS DRAWING IS PROPERTY OF **"TATA PROJECTS LIMITED"** MUST NOT BE PASSED ON TO ANY PERSON OR BODY NOT AUTHORIZED BY US TO RECEIVE IT NOR BE COPIED OR OTHERWISE MADE USE EITHER IN FULL OR IN PART BY SUCH PERSON OR BODY WITHOUT OUR PRIOR PERMISSION IN WRITING.

EPC CONTRACTOR
TATA PROJECTS LIMITED
H. NO.1-7-80 TO 87, "MITHONA TOWERS - 1"
PRENDERGHAST ROAD, SECUNDERABAD - 500003.

PROJECT TITLE
PLANT FACILITY FOR
MADHEPURA ELECTRIC LOCOMOTIVE PRIVATE LIMITED
AT MADHEPURA, BIHAR.

OWNER
MADHEPURA ELECTRIC LOCOMOTIVE PRIVATE LIMITED

OWNER A/E CONSULTANT :
SEMAC CONSULTANTS PVT LTD
6-1-276, 2ND FLOOR, ARCHANA BLOCK,
CONJEEVARAM HOUSE, PADMARAO NAGAR
SECUNDERABAD - 500025.

	SIGNATURE	DATE
DRAWN	GMN/MZ	14.02.17
DESIGNED	NP	14.02.17
CHECKED	AS	14.02.17
DEPT.HEAD	AS	14.02.17

DWG. TITLE:
TOWNSHIP AREA
ELECTRICAL SUBSTATION BUILDING
ARCHITECTURAL ELEVATIONS & SECTIONS

RELEASED FOR	
INFORMATION	
APPROVAL	
ENGINEERING	
CONSTRUCTION	✓

DEPT. CIVIL | JOB NO. 0000 | SCALE: – | SHEET: 2 OF 2 | SIZE : A1
FILE NAME. ALSTOM-M-AR-SS-101 | REV./ISSUE
DWG.NO. TPL-3452-X9690-EC-AC-6398 | R1