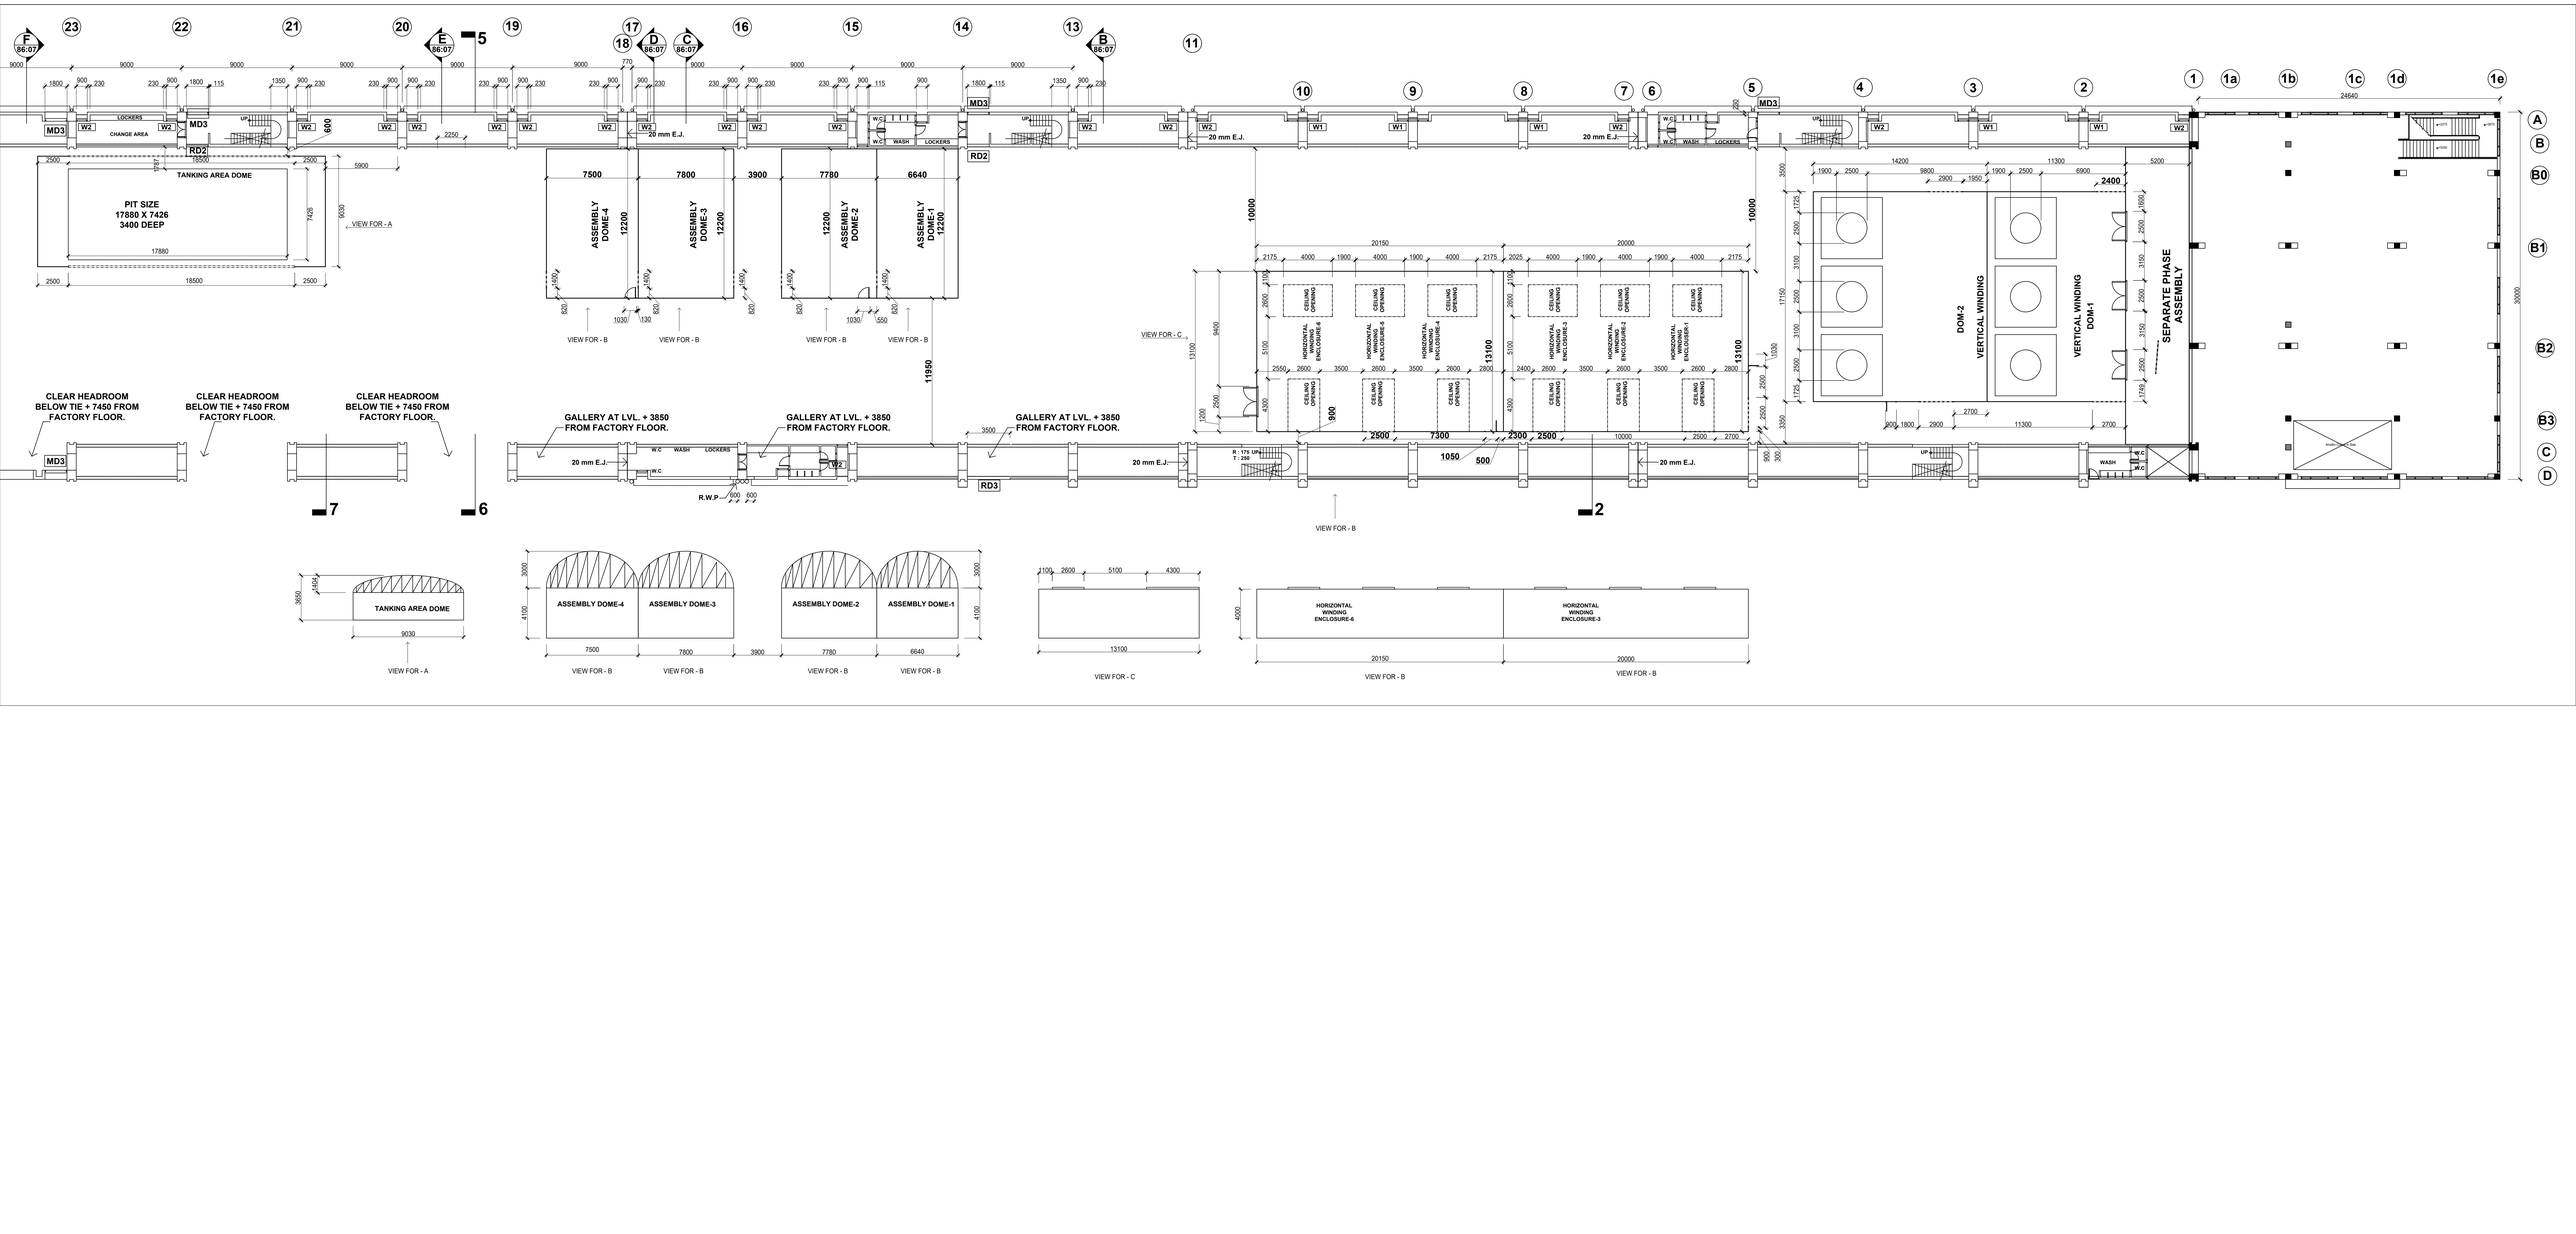

TANKING AREA DOME
PIT SIZE
17880 X 7426
3400 DEEP
VIEW FOR - A
ASSEMBLY DOME-4
ASSEMBLY DOME-3
ASSEMBLY DOME-2
ASSEMBLY DOME-1
VIEW FOR - B
VIEW FOR - C
20 mm E.J.
LOCKERS
CHANGE AREA
WASH
W.C
MD3
RD2
RD3
DOM-2
VERTICAL WINDING
DOM-1
SEPARATE PHASE ASSEMBLY
CEILING OPENING
HORIZONTAL WINDING ENCLOSURE-1
HORIZONTAL WINDING ENCLOSURE-2
HORIZONTAL WINDING ENCLOSURE-3
HORIZONTAL WINDING ENCLOSURE-4
HORIZONTAL WINDING ENCLOSURE-6
CLEAR HEADROOM BELOW TIE + 7450 FROM FACTORY FLOOR.
GALLERY AT LVL. + 3850 FROM FACTORY FLOOR.
R.W.P
R : 175 UP
T : 250
UP
W1
W2