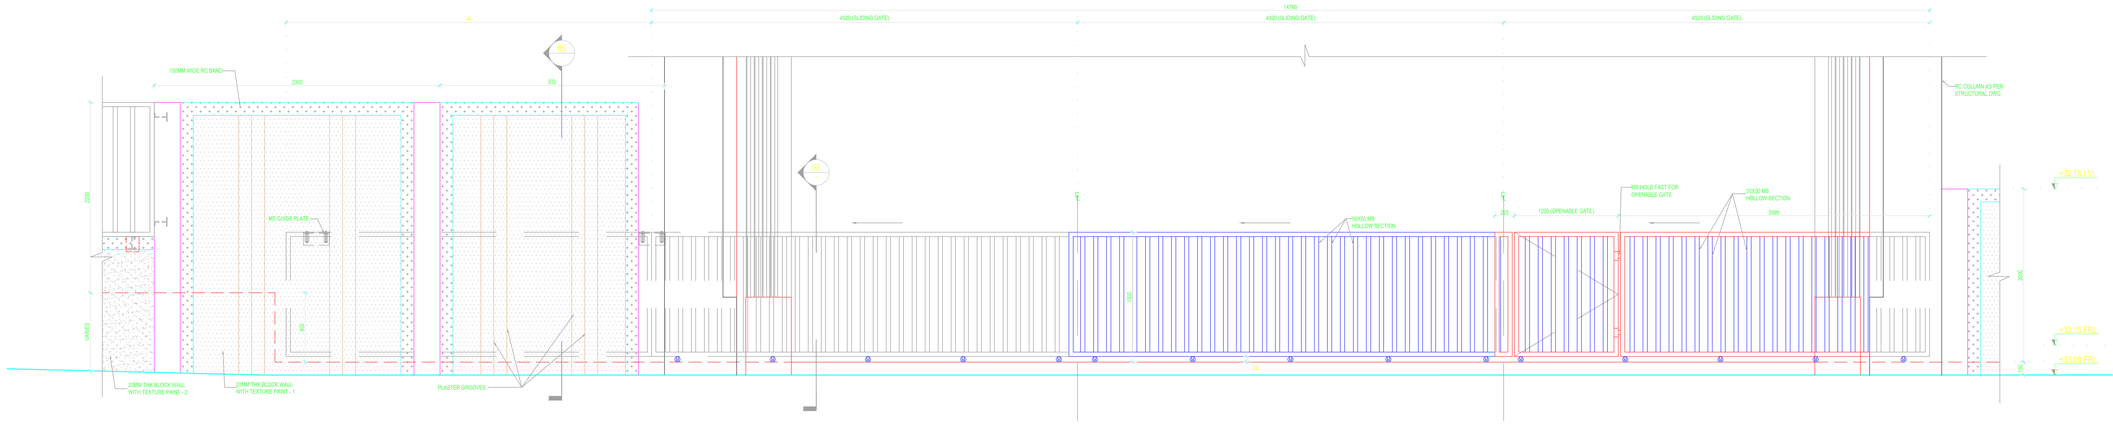
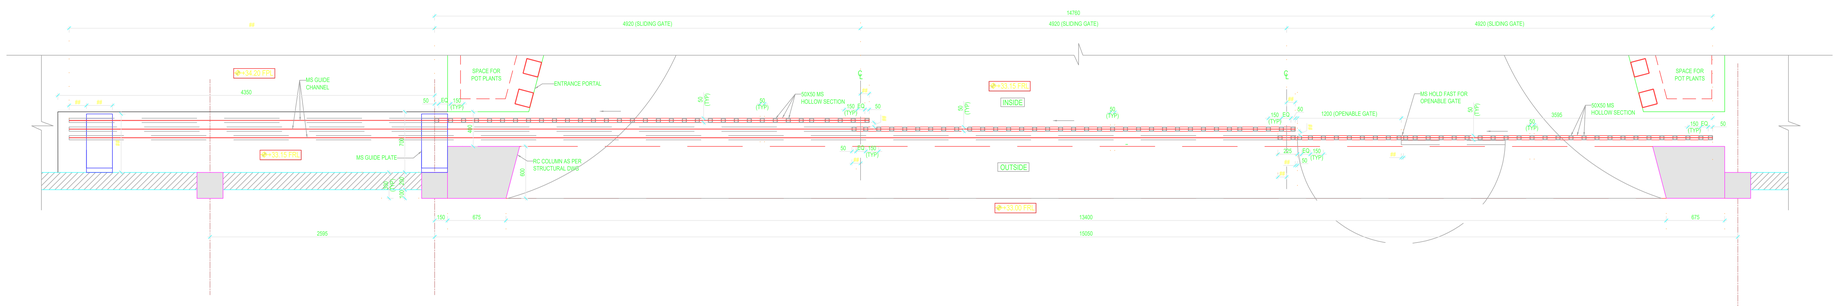

14790
4920 (SLIDING GATE)
4920 (SLIDING GATE)
4920 (SLIDING GATE)
3300
EQ
05
05
150MM WIDE RC BAND
RC COLUMN AS PER STRUCTURAL DWG
MS GUIDE PLATE
50X50 MS HOLLOW SECTION
MS HOLD FAST FOR OPENABLE GATE
50X50 MS HOLLOW SECTION
1200 (OPENABLE GATE)
3595
205
+35.15 LVL
+33.15 FRL
+33.00 FRL
3200
2000
VARIES
300
20MM THK BLOCK WALL WITH TEXTURE PAINT - 2
20MM THK BLOCK WALL WITH TEXTURE PAINT - 1
PLASTER GROOVES


14790
4920 (SLIDING GATE)
4920 (SLIDING GATE)
4920 (SLIDING GATE)
+33.20 FRL
MS GUIDE CHANNEL
SPACE FOR POT PLANTS
ENTRANCE PORTAL
50X50 MS HOLLOW SECTION
+33.15 FRL
INSIDE
MS HOLD FAST FOR OPENABLE GATE
1200 (OPENABLE GATE)
3595
50X50 MS HOLLOW SECTION
SPACE FOR POT PLANTS
4300
+33.15 FRL
MS GUIDE PLATE
RC COLUMN AS PER STRUCTURAL DWG
OUTSIDE
+33.00 FRL
2995
150
675
13400
15650
675