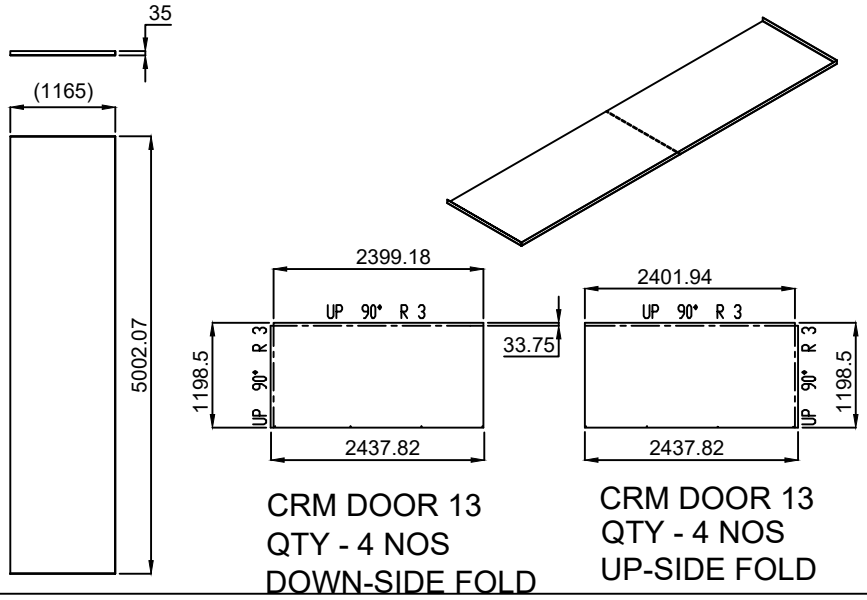
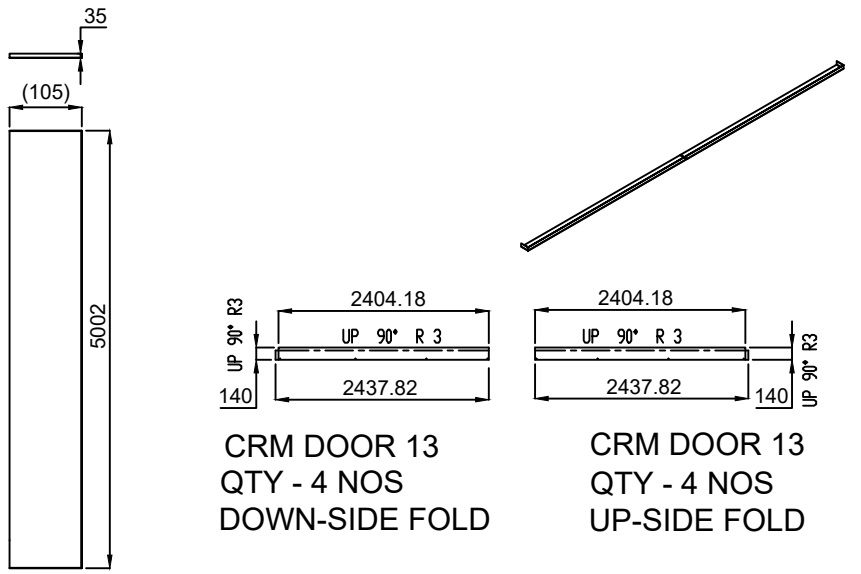


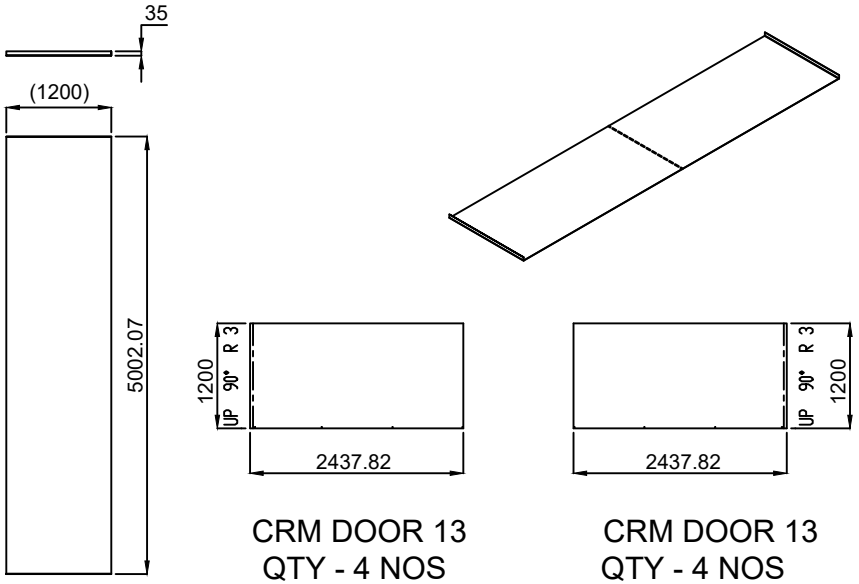

CRM DOOR 13
QTY - 4 NOS
DOWN-SIDE FOLD

CRM DOOR 13
QTY - 4 NOS
UP-SIDE FOLD




CRM DOOR 13
QTY - 4 NOS
DOWN-SIDE FOLD

CRM DOOR 13
QTY - 4 NOS
UP-SIDE FOLD



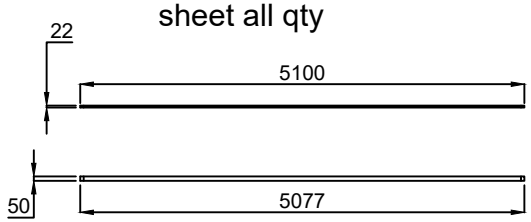

CRM DOOR 13
QTY - 4 NOS
DOWN-SIDE FOLD

CRM DOOR 13
QTY - 4 NOS
UP-SIDE FOLD

## NOTE: DURING BENDING CRITICAL DIMENSION SHOULD BE MANDETORY

CRM DOOR 13

QTY - 16 NOS / each sheet all qty




PPGI SHEET 1 MM

| REV. | REVISION DESCRIPTION | Date | Revised By |
|---|---|---|---|
| 000 | MODIFIED DUE TO RECIEVED COIL SIZE 1210 MM INSTEAD OF 1250 MM | 21/05/2022 | MAHESH S. |
| | | | |
| | | | |

This drawing & design is the property of NIHVA TECHNOLOGIES. Not to be sold or copied to any other concern.

TITLE:- 4 LEAF PPGI CLADDING CRM DOOR 13

NIHVA TECHNOLOGIES PVT. LTD.

NIHVA TECHNOLOGIES PVT. LTD. PUNE
Tel : 020 66304033
Email:- info@nihva.com
Website:- www.nihva.com

| | NAME | DATE | SIGN |
|---|---|---|---|
| DRAWN | M.SUTAR | 21/05/2022 | |
| CHECK | M.SUTAR | 21/05/2022 | |
| APPRD. | | | |

If any queries contact : design@nihva.com

ALL DIMENSION ARE IN mm

CLIENT - NIHVA TECHNOLOGIES PVT.LTD

LOCATION -

PRODUCT - SLIDING DOOR

DWG NO:-NIHVA/22-23/VDR/0015 | REV- 0

SCALE: NTS | SCALE:-- 1:1 | SHEET: 01 OF 02