


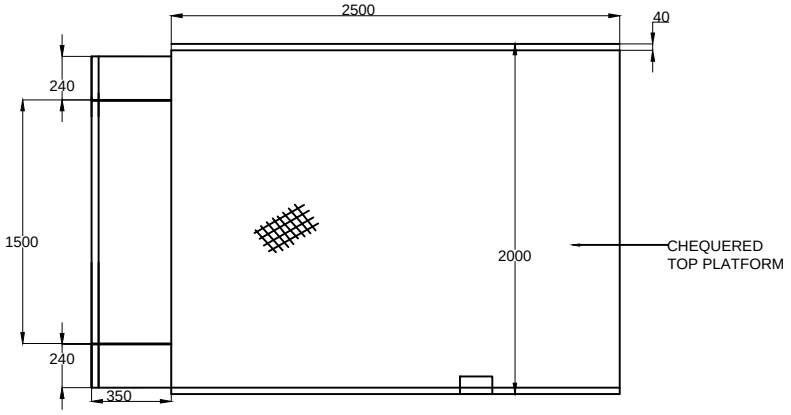


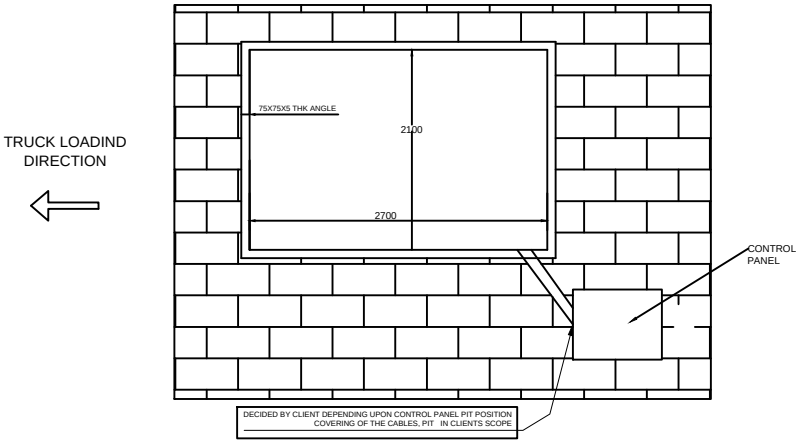

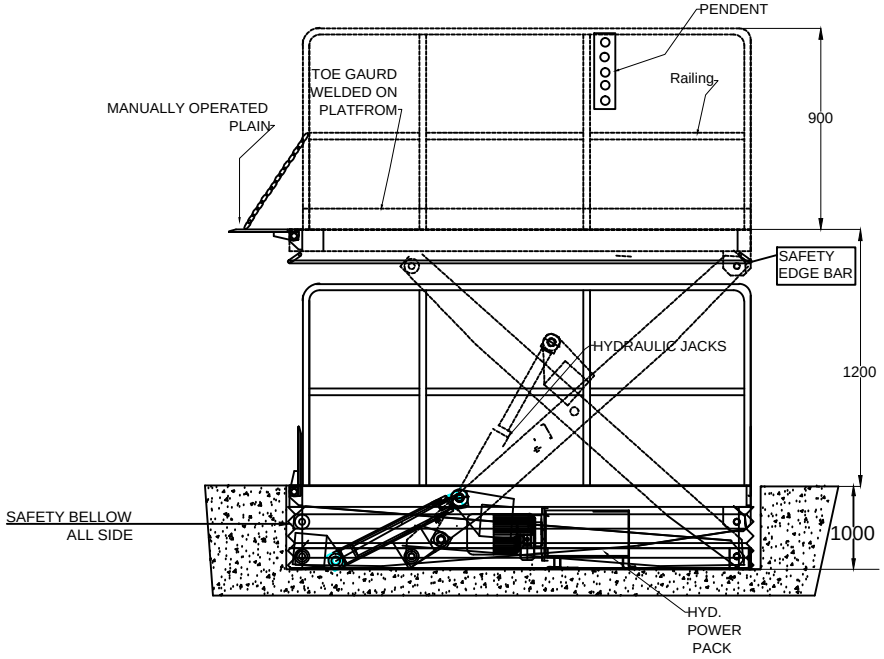

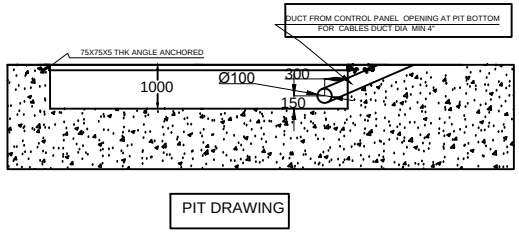

PIT DRAWING

NOTE :
1. PIT FOR SCISSORLIFT HAS TO BE DIAGONALLY WITHIN 3-5 MM
2. BASE OF THE PIT HAS TO BE IN WATER LEVEL AND RIGHT ANGLE TO THE VERTICAL SIDE WALLS
3. PROPER ARRANGEMENT FOR ROUTING HOSES AND CABLES HAVE TO BE MADE DEPENDING ON SITE CONDITIONS AND POSITION OF POWER PACK
4. COVERING REQUIRED FOR HOSES AND CABLES AND RELATED CIVIL WORK IS IN CLIENTS SCOPE
5. WATER DRAINAGE AND PIT CLEANING NEEDS TO BE CONSIDERED AND DONE BY CLIENT.
6. PIT & ALL CIVIL WORK IS IN CLIENT SCOPE .

SPECIFICATIONS OF SCISSOR LIFT -
1. PLATFORM SIZE -2000WX2500L
2. CLOSE HEIGHT - 1000 MM
3. LIFT HEIGHT ABOVE FLOOR LEVEL - 1200 MM
4. CAPACITY - 6 TON UDL
5. FINISH - HOT DEEP GALVANISING
6. QTY - TOTAL 4 NOS OF SCISSOR LIFT (2 NOS FOR PHASE 1 & 2 NOS FOR PHASE 2)
7. HYDRAULIC POWERPACK - 7.5 HP , 3 PHASE AC , 50 Hz , MOUNTED INSIDE PIT
8. LIP - ONE SIDE MANUAL , 3 PIECE SPLIT TYPE(240+1500+240)
9. SAFETY BELLOW - ALL SIDE
10. CUTOFF LIMIT SWITCH FOR MAXIMUM LIFT
11. MAINTENANCE STOPPER - MANUAL , 2 NOS
12. SCISSOR LIFT INTERLOCK PROVIDED WITH SECTIONAL DOOR & DOCK LEVELER

This drawing & designing is the property of NIHVA TECHNOLOGIES. Not be sold or copy to any other concern.

TITLE			
PIT MOUNTED ELECTRO-HYDRAULIC SCISSOR LIFT			NIHVA TECHNOLOGIES PVT. LTD.
	SIGN	DATE	
DRAWN	SS	17.7.2021	CLIENT - SUBHASHREE ENGG & CONSTRUCTIONS PVT LTD
CHECK	VJ		PROJECT - E+H FLOWTECH INDIA PVT LTD
REV.	AK		SITE - AURANGABAD
APPROVAL	VT		DWG. NO. : NIHVA/21-22/045/SL / REV NO - R00
If any queries contact : nihvacare@nihva.com			SCALE: NTS / WT: / SHEET: 01 OF 01
ALL DIMENSION ARE IN mm			

NIHVA TECHNOLOGY PVT. LTD. PUNE
Tel : 020 66304033
Email:- info@nihva.com
Website:- www.nihva.com