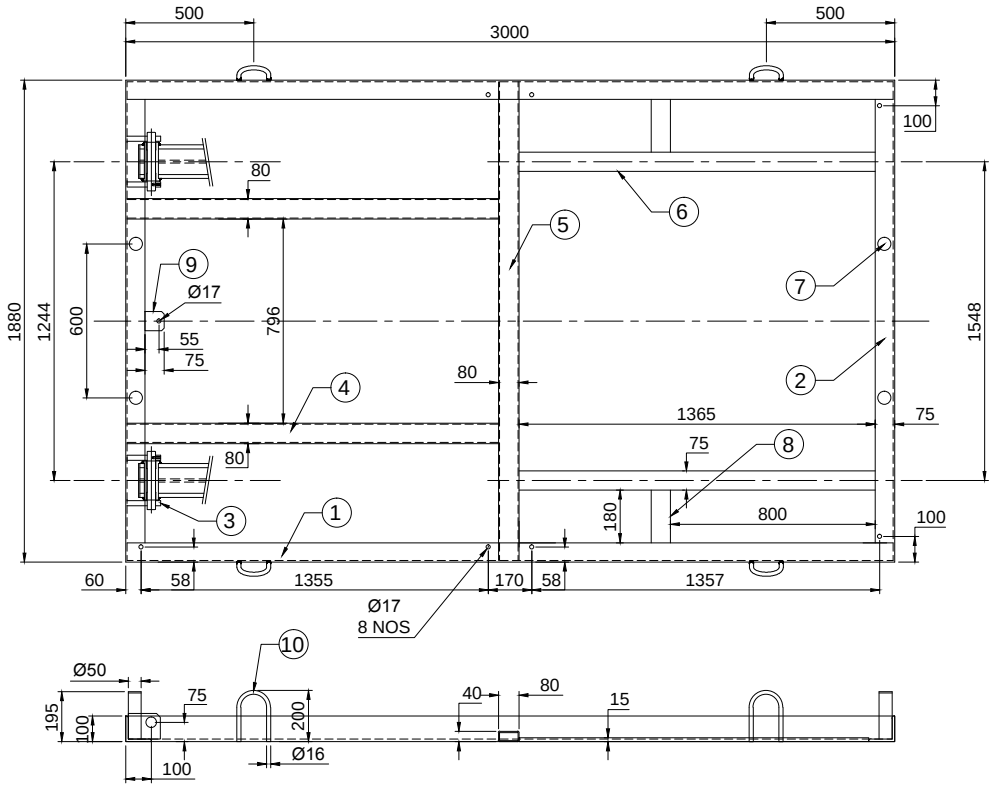
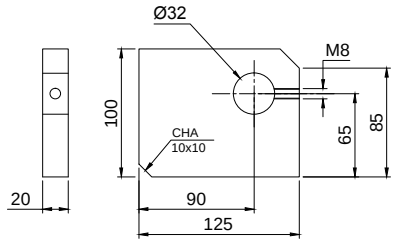



| SR NO | PART NAME | SPECIFICATION | QTY |
|---|---|---|---|
| 1 | ISA | 100 X 100 X 10 X 3000L | 2 NOS |
| 2 | ISA | 100 X 100 X 10 X 1860L | 2 NOS |
| 3 | LASER PRO. | 100 X 20 THK X 125L | 4 NOS |
| 4 | R.TUBE | 80 X 40 X 4 X 1445L | 2 NOS |
| 5 | R.TUBE | 80 X 40 X 4 X 1860L | 1 NO |
| 6 | EN8 FLAT | 75 X 15 X 1365L | 2 NOS |
| 7 | STOPPER | EN8 Ø50 X 200L | 4 NOS |
| 8 | FLAT | 75 X 15 X 180L | 2 NOS |
| 9 | FLAT | 75 X 15 X 75L | 1 NO |
| 10 | MS BAR | Ø16 X 500L | 4 NOS |
| 11 | ANCHOR BOLT | M16 X 150L | 9 NOS |

| | | | |
|---|---|---|---|
| 01 | 20.11.18 | P.A | POINT NO 4,6 & 8 SIZES CHANGE |
| REV NO | DATE | DRAWN | REMARK |

This drawing & design is the property of NIHVA TECHNOLOGIES. Not to be sold or copied to any other concern.

TITLE: BASE FRAME

NIHVA TECHNOLOGIES PVT. LTD.
NIHVA TECHNOLOGIES PVT. LTD. PUNE
Tel : 020 66304033
Email:- info@nihva.com
Website:- www.nihva.com

| | NAME | SIGN | DATE |
|---|---|---|---|
| DRAWN | P.A | | 19.11.2018 |
| CHECK | R.D | | 19.11.2018 |
| APPRD. | V.T | | 19.11.2018 |

CLIENT -
PROJECT -
SITE LOCATION -

If any queries contact : design@nihva.com
DWG. NO. :NIHVA/18-19/MFG/NSL1002/03/R01
REV- 01
ALL DIMENSION ARE IN mm
SCALE: NTS
WT:
SHEET: 01 OF 01