

Revision		Date	By
A	Beam clamps removed	2016-04-13	PL
B	TH was 7639, TW was 37690,	2016-04-29	PL
C	TH was 7321	2016-05-10	PL

LOAD DIAGRAM


Nominal static vertical loads are indicated. Value within brackets include dynamic surload factor 1.25 for door leaf loads in open position.
Includes items provided by ASSA ABLOY only.

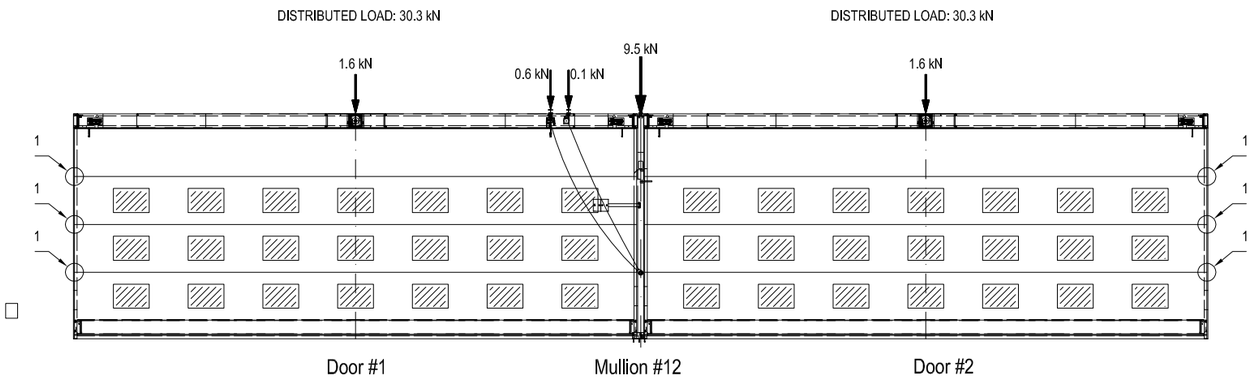


Interior view, Door closed

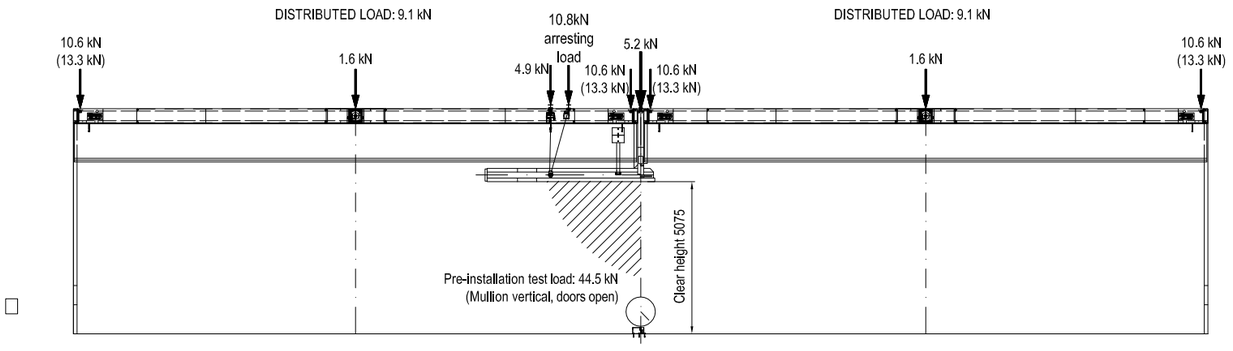

Interior view, Door open

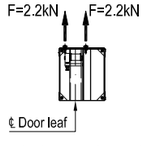

Load on header box attachment (each screw), due to wind load and door weight

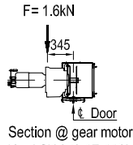


Section @ gear motor
Nord SK 973.1Z-112M/4
Scale 1:20




Arresting load: 10.8kN
Rupture load: 31.0kN


Extra load arrester rotation during lifting sequence. Scale 1:20

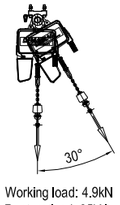

Working load: 4.9kN
Rupture load: 35kN

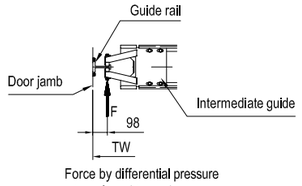

Force by differential pressure transferred to guide rail at each intermediate position.
(located at pos 1)
F=14.8 kN

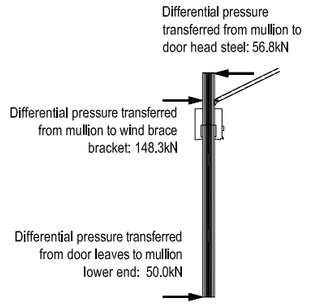

NOT INCLUDED IN DOOR SUPPLY:

1. Design and supply of all door supporting structural components.
2. Design and supply of all closure between door and adjacent steel.
3. Door jambs adjustable for overall door width and true to plumb.
4. Paint job after completed door installation.
5. Any frameworks being provided by ASSA ABLOY will be clearly indicated as "by ASSA ABLOY".

REQUIREMENTS ON BUILDING:

6. Door head support must be straight within 1/600 of span in the in/out direction and free from protrusions of any kind.
7. For a single door leaf, door head support should be horizontal and straight within 1/600 of span at distributed full door load.
8. Door side jambs must be smooth, straight and parallel, out of plumb must not exceed 2mm/m (total deviation at full length 5 mm) in any direction.
9. Any footings at bottom of jamb columns must not interfere with installation of guide rails at floor level.
10. At time of installation, finished floor, free from obstructions, out to a distance of 2 m on each side of door centreline must be available.

DOOR PROPERTIES:

11. The door is designed to withstand a differential pressure of 1.0kPa.
14. Mullions #12 and mullion pits are designed to allow for 0mm of downward deflection and 0mm of upward deflection due to external loads such as wind.
15. Guide rails, top- and intermediate beams in extruded aluminium with natural finish.
16. Environmental category: Megadoor standard
17. Bottom beams & Mullions carbon steel painted: Light grey (RAL7047)
18. Color of header box: BLACK (NCS 9000-N. RAL 9005)
17. Door header box enclosed on both sides.
18. Motor cover.
19. Colored clamp strips on both sides: Translucent
20. Vision panels 1200x800 (21x)/door
21. The door fabric is a UV stabilized, flame retardant, self-extinguishing, PVC coated polyester fabric with fire technical properties Euroclass C-s2, d0 (according to EN 13501-1:2007).
    Colour of fabric: TRANSLUCENT WHITE

ELECTRICAL:

22. One main control panel provided of PLC type.
23. Control mode : Impulse up / Constant contact down.
24. Cables are included.
25. Back-up power socket & switch.
26. Audible & visual alarm.
27. Wet terminals for external fire alarm.
28. Approx. size of main control panel: WxHxD (500mm x 600mmx250 mm),
29. Location of main control panel: Inside, left inside view.
30. Aux. Voltage 24VDC
31. Power supply: 400V /3Ph /50Hz
32. Power: 10.0kW
33. Nom. current: 20.4A
34. Start. current: 90.0A
35. (max. allowed voltage drop at start: 5%)

BELT HOIST UNITS:#1 & #2
NORD SK 973.1Z-112M/4
75mm wide polyester belt. Rupture load 80.0kN/belt.

MULLION CHAIN HOISTS:
DEMAG DC-PRO5.
Chain rupture load: 35kN

EXTRA LOAD ARRESTER
SALA PL-A 500-5
Rupture load 31kN

Steel building company in cooperation with door installing company must make a pre-installation load test on the structure, where the mullions are located, in order to simulate the vertical deflection of the structure that occurs when doors are installed. This vertical deflection figure will be used to determine the correct installation level of the mullions. Required material/equipment and personnel by others than ASSA ABLOY.

DOOR IDENTITY NUMBER: 84005001-002

INTERFACE, ref. to drwng. no. 62169

DESIGNED	APPROVED	SIZE	SCALE
PL		A1	1:100

CODE 84005
ITEM NO
DATE 2016-04-06

If not otherwise stated:
Tolerances ISO 2768-m EN ISO 13920-B
Cutting class ISO 9013-442
Weld class ISO 5817-C
Surface finish Smooth raw surface

ASSA ABLOY

NVIDIA
India
Megadoor 37610 x 5732/5075
Load diagram & Notes

PLOT DATE

DRAWING NO 62170
REVISION C

This document is the property of ASSA ABLOY Entrance Systems AB and shall not without our written permission be copied, imparted to a third party or used for any other unauthorized purpose.