

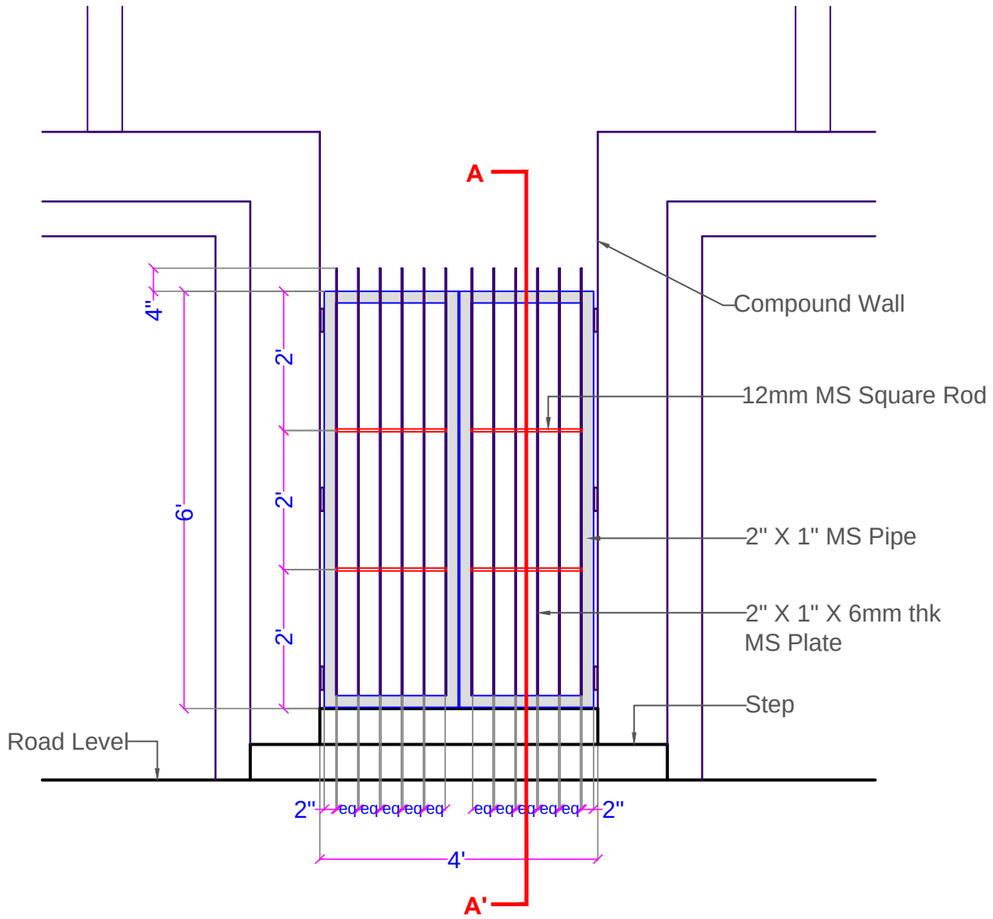


FRONT ELEVATION

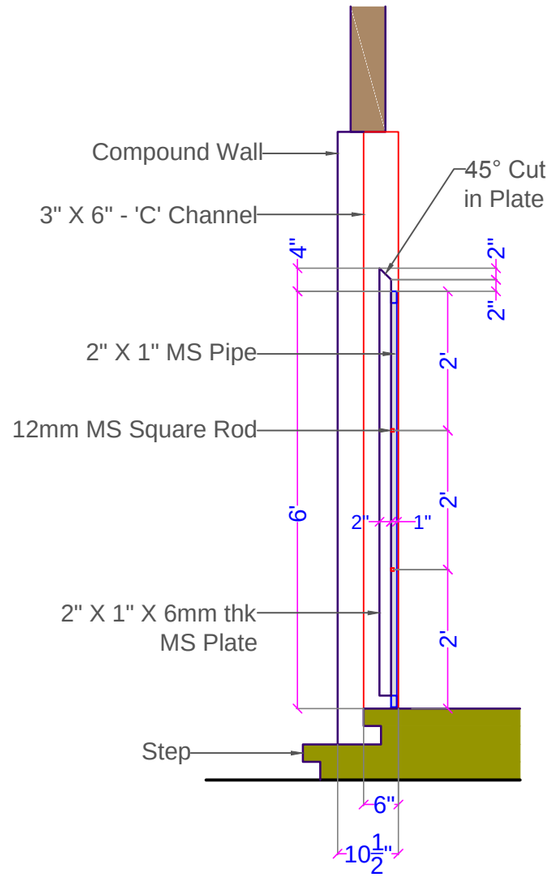

SECTION A-A'

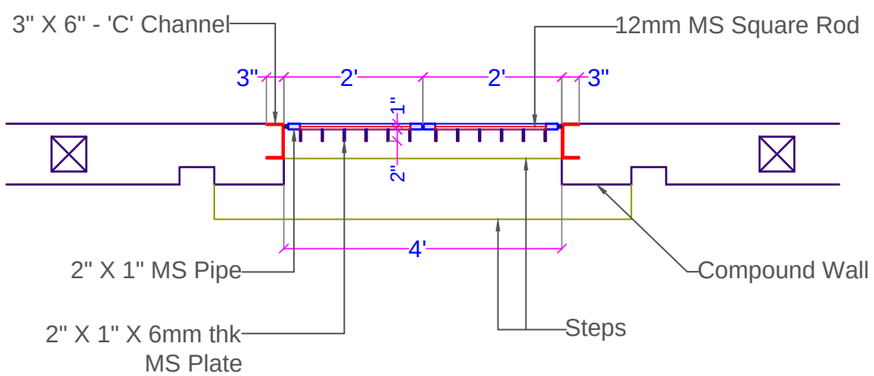

PLAN

REVISION:	DATE:

REVISION NOTE:

* This revised drawing supercedes all the previous drawings given for the same job title/ drg no .

SIGN:
Designer

SIGN:
Client

DRAWING STATUS:
A D V A N C E C O P Y

TITLE:
LANDSCAPE AREA - PEDESTRIAN GATE DETAILS

PROJECT:
PROPOSED INTERIOR DESIGNING WORK OF RESIDENCE FOR MR. SANJAY ADHAV

NOTE:

* Do not scale the drawing for measurements.
* All dimensions are in feet and inches
* Drawings with multiple reference are to be read in conjunction of respective drawings.
* Dimensions are to be verified at site before starting the work.
* Any discrepancy in the drawing should be bought to the attention of designer or site coordinator and clarified before starting the work.

* **This Drawing is the property of ANIRUDDHA SANE & ASSOCIATES. It should not be copied, reproduced or retransfer in any manner either in part or full, and it shall be used only for the job issued for.**

Scale : NTS	Date : 30.05.2022
Drg No : RES/WD/FUR/02	
Job No :	
Drg By : NIKHIL	Chk By : ASA

ANIRUDDHA SANE & ASSOCIATES
Interior Designers & Consultants

A12, Shree Keshav Smruti,
197 Sadashiv Peth, Pune 30.
Ph No : 020 - 24530277
email: aniruddha.sane@yahoo.in