


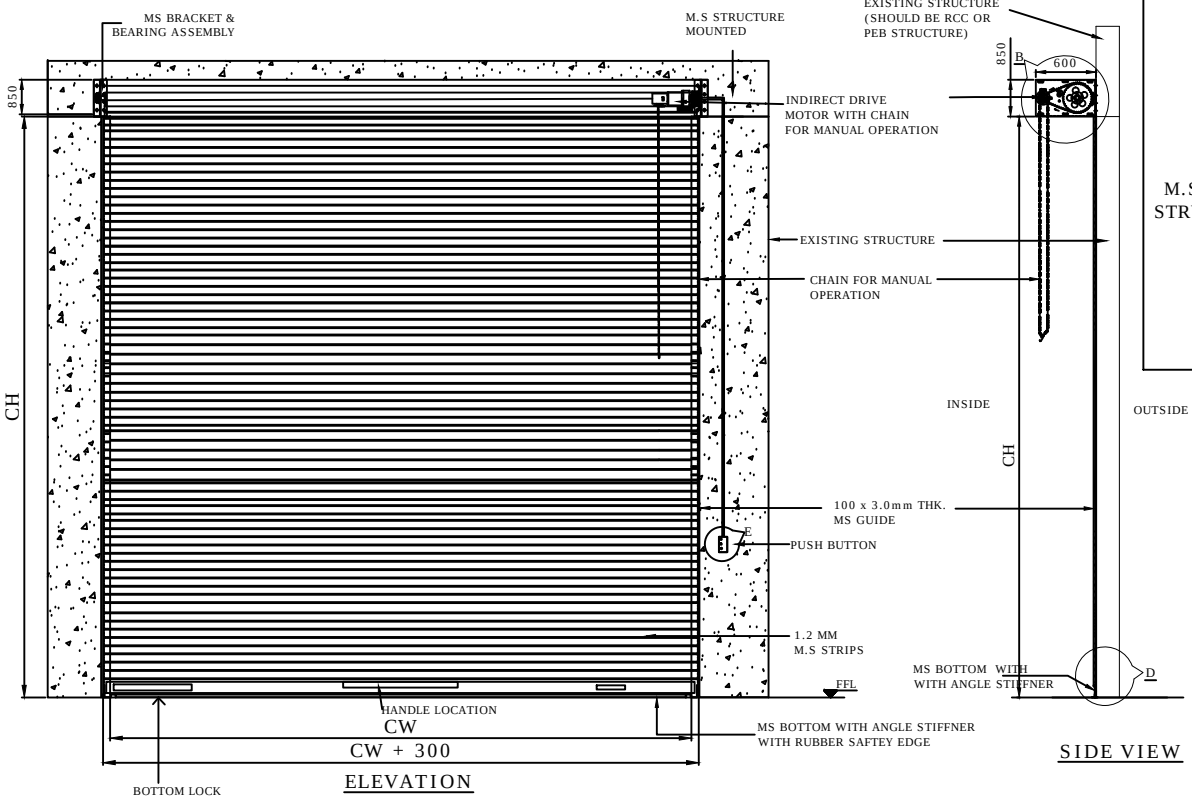


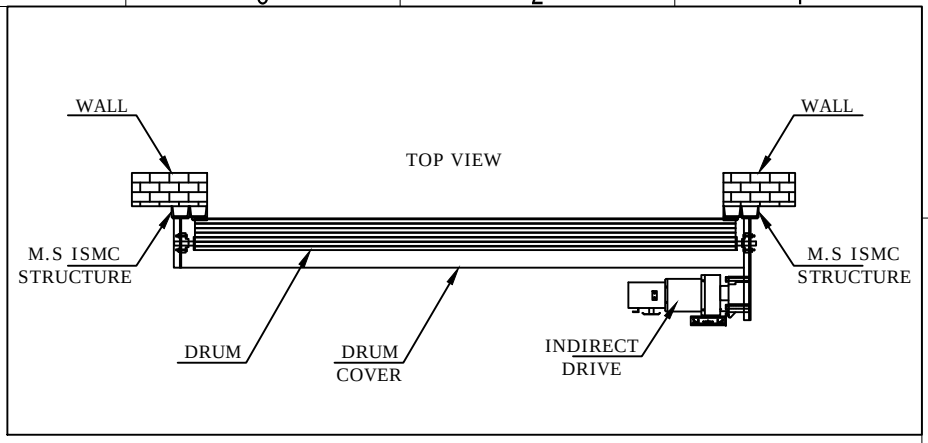

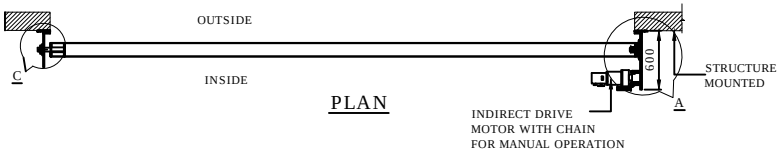

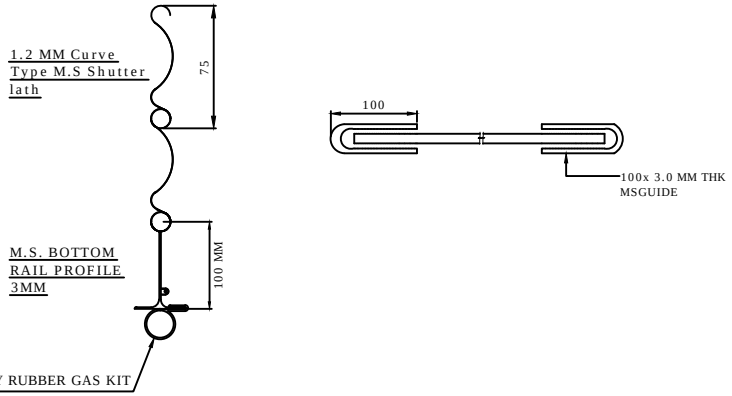

(NOTE: REQUIRED STRUCTURE FOR SHUTTER SHOULD BE IN CLIENT SCOPE.)

RAL 1003			
RAL 2004			
RAL 3000			
RAL 5002			
RAL 6005			
RAL 7035			
RAL 9005			
RAL 9010			

CLEAR WIDTH (CW)	CLEAR HEIGHT (CH)	QUANTITY
4000	6000	1
4500	4500	1
3000	4700	1
3000	3500	1

REV NO	REV DATE	DRAWN BY	REMARK
R01	09.09.2019	P.V.A	1. TOP ENLARGE VIEW ADDED. 2. LATH THK MENSION.

This drawing & design is the property of NIHVA TECHNOLOGIES. Not to be sold or copied to any other concern.

TITLE: MOTORIZED ROLLING SHUTTER

	NAME	SIGN	DATE
DRAWN	P.V.A		14.08.2019
CHECK	V.M.T		14.08.2019
APPRD.			

NIHVA TECHNOLOGIES PVT. LTD.
NIHVA TECHNOLOGIES PVT. LTD. PUNE
Tel : 020 66304033
Email:- info@nihva.com
Website:- www.nihva.com

CLIENT - DHOOT BUILDER

PROJECT -

SITE LOCATION - ADR AXLES SITE,RAJGURUNAGAR KHED

If any queries contact : design@nihva.com

DWG. NO. : NIHVA/19-20/0077/R01 | REV- R01

ALL DIMENSION ARE IN mm | SCALE: NTS | WT: | SHEET: