
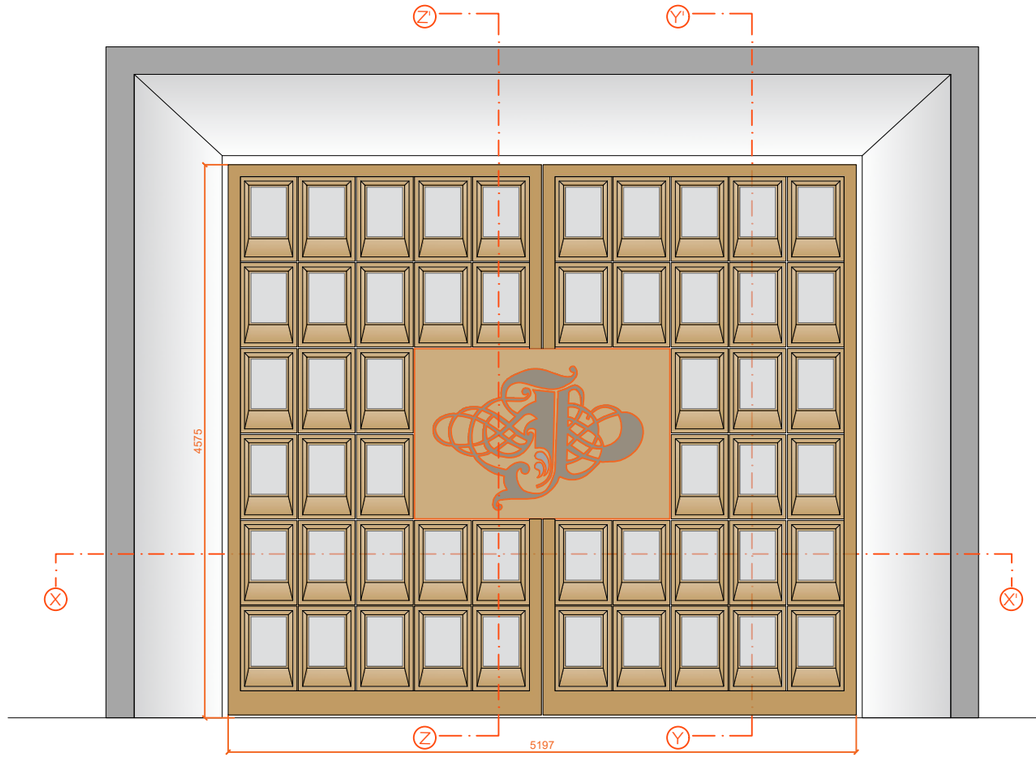



Gate to be Finished with PU Matt

01 Main Gate Front Elevation
Scale NTS

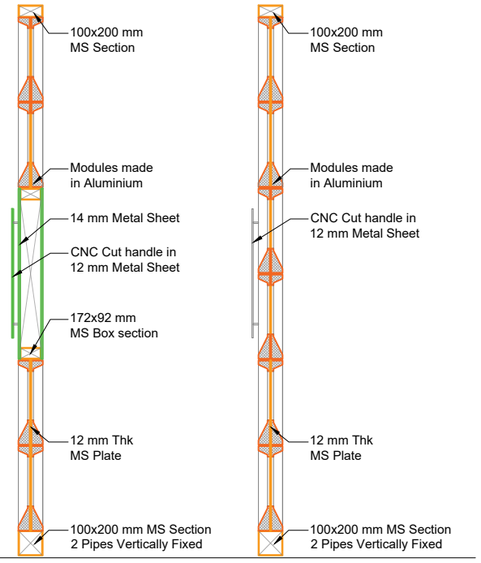

03 Section Z-Z'
Scale 1:20

04 Section Y-Y'
Scale 1:20

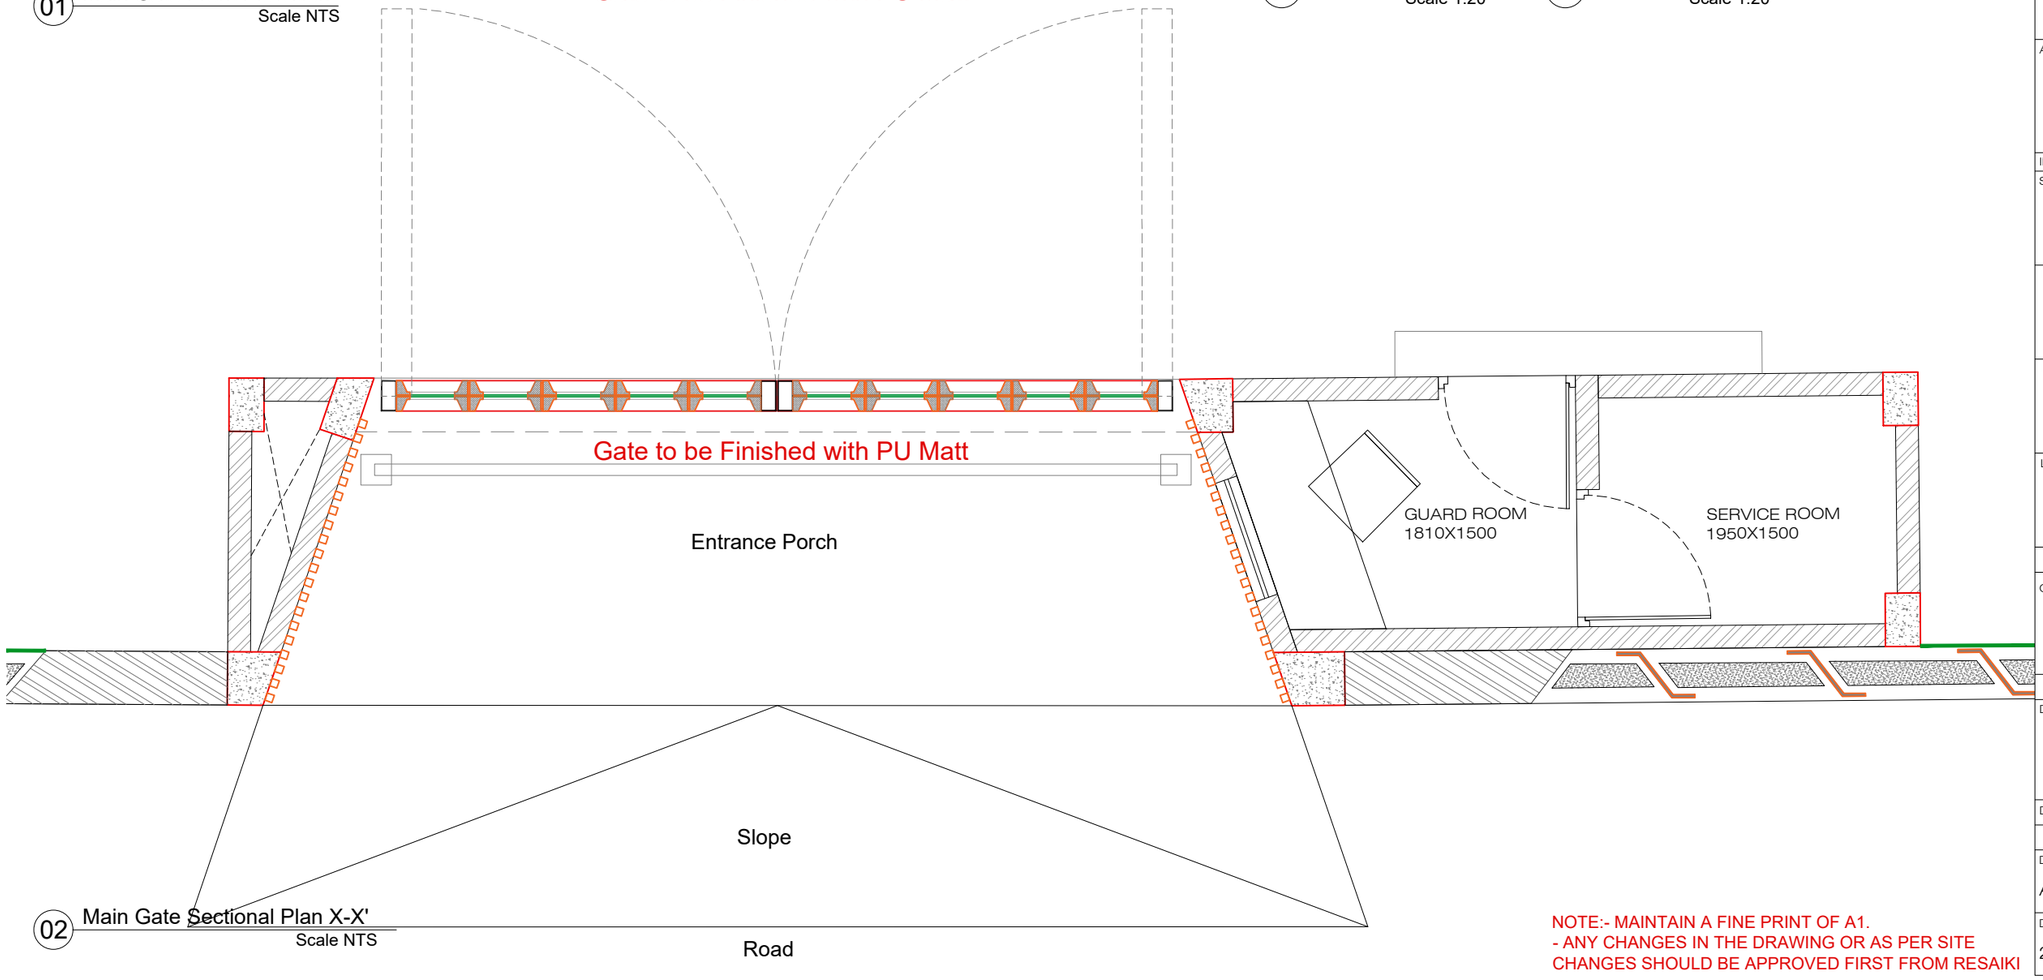

02 Main Gate Sectional Plan X-X'
Scale NTS

NOTE:- MAINTAIN A FINE PRINT OF A1.
- ANY CHANGES IN THE DRAWING OR AS PER SITE CHANGES SHOULD BE APPROVED FIRST FROM RESAIKI

NOTES

1. DO NOT SCALE THE DRAWING, FOLLOW ONLY FIGURED DIMENSIONS.
2. ALL DIMENSIONS GIVEN IN THIS DRAWING ARE EITHER IN FEET INCHES UNLESS NOTED OTHERWISE.
3. ALL DIMENSIONS TO BE VERIFIED ON SITE AND APPROVED BY THE SITE ENGINEER.
4. ANY DISCREPANCY OR AMBIGUITY IN THE DRAWINGS SHOULD IMMEDIATELY BE BROUGHT TO NOTICE OF THE ARCHITECT.
5. ALL DRAWINGS SHOULD BE READ IN CONJUNCTION WITH OTHER RELEVANT ARCHITECTURAL, STRUCTURAL, PLUMBING, MECHANICAL AND ELECTRICAL DRAWINGS.
6. THE ± 0 REFERS TO LEVEL ESTABLISHED AT SITE IN PRESENCE OF THE SITE SUPERVISOR AND THE ARCHITECT. ALL REMAINING LEVELS ARE RELATIVE TO THIS LEVEL.
7. THIS DRAWING IS THE COPYRIGHT OF RESAIKI AND MUST NOT BE RETAINED, COPIED OR USED WITHOUT THEIR AUTHORITY.

S No.	Revision No.	Revision Description	Drawn By	Check By	Design By
#	#	#	#	#	#
#	#	#	#	#	#
#	#	#	#	#	#
#	#	#	#	#	#

ARCHITECTS

resaiki

IN ASSOCIATION WITH

STRUCTURE

PLUMBING & FIRE FIGHTING

HVAC

LANDSCAPE CONSULTANTS

CLIENT NAME

MRS. SMITA JADHAV

DRAWING TITLE

RAJ BUNGALOW
MAIN GATE DETAILS


DRG.No. A-23005-MG-04A

GOOD FOR CONSTRUCTION


DRAWN BY	CHECKED BY	DESIGN BY
AG	AB	KVA

DATE	SCALE	PROJECT NO.
21.02.2024	NTS	23005

R0

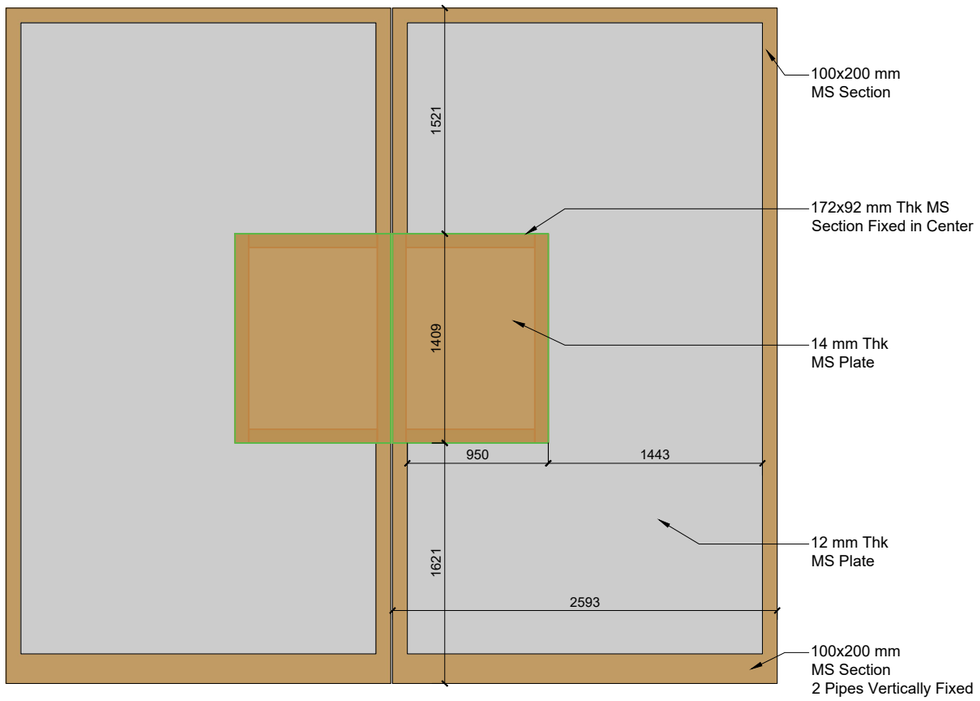

01 Main Gate MS Frame
Scale NTS

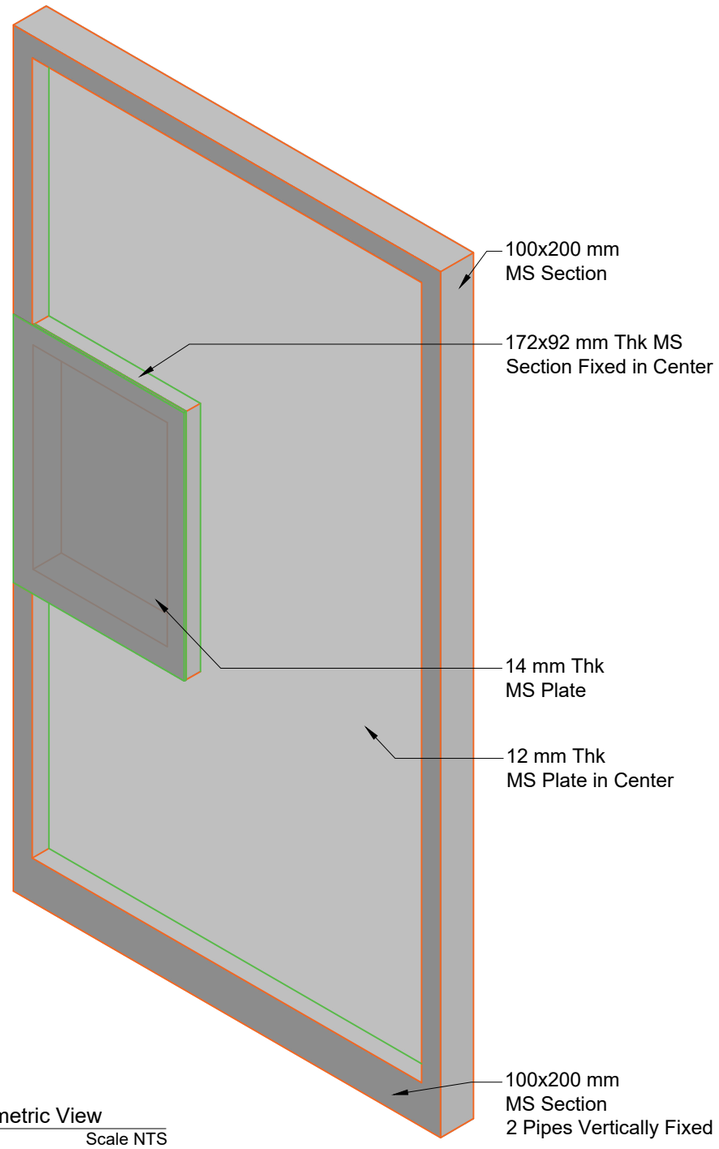

03 Isometric View
Scale NTS

NOTES

1. DO NOT SCALE THE DRAWING, FOLLOW ONLY FIGURED DIMENSIONS.
2. ALL DIMENSIONS GIVEN IN THIS DRAWING ARE EITHER IN FEET INCHES UNLESS NOTED OTHERWISE.
3. ALL DIMENSIONS TO BE VERIFIED ON SITE AND APPROVED BY THE SITE ENGINEER.
4. ANY DISCREPANCY OR AMBIGUITY IN THE DRAWINGS SHOULD IMMEDIATELY BE BROUGHT TO NOTICE OF THE ARCHITECT.
5. ALL DRAWINGS SHOULD BE READ IN CONJUNCTION WITH OTHER RELEVANT ARCHITECTURAL, STRUCTURAL, PLUMBING, MECHANICAL AND ELECTRICAL DRAWINGS.
6. THE ± 0 REFERS TO LEVEL ESTABLISHED AT SITE IN PRESENCE OF THE SITE SUPERVISOR AND THE ARCHITECT. ALL REMAINING LEVELS ARE RELATIVE TO THIS LEVEL.
7. THIS DRAWING IS THE COPYRIGHT OF RESAIKI AND MUST NOT BE RETAINED, COPIED OR USED WITHOUT THEIR AUTHORITY.

S No.	Revision No.	Revision Description	Drawn By	Check By	Design By
#	#	#	#	#	#
#	#	#	#	#	#
#	#	#	#	#	#
#	#	#	#	#	#

ARCHITECTS

resaiki

IN ASSOCIATION WITH

STRUCTURE

PLUMBING & FIRE FIGHTING

HVAC

LANDSCAPE CONSULTANTS

CLIENT NAME

MRS. SMITA JADHAV

DRAWING TITLE

RAJ BUNGALOW
MAIN GATE DETAILS

DRG.No. A-23005-MG-04B

DRAWN BY	CHECKED BY	DESIGN BY
AG	AB	KVA
DATE	SCALE	PROJECT NO.
21.02.2024	NTS	23005

R0