

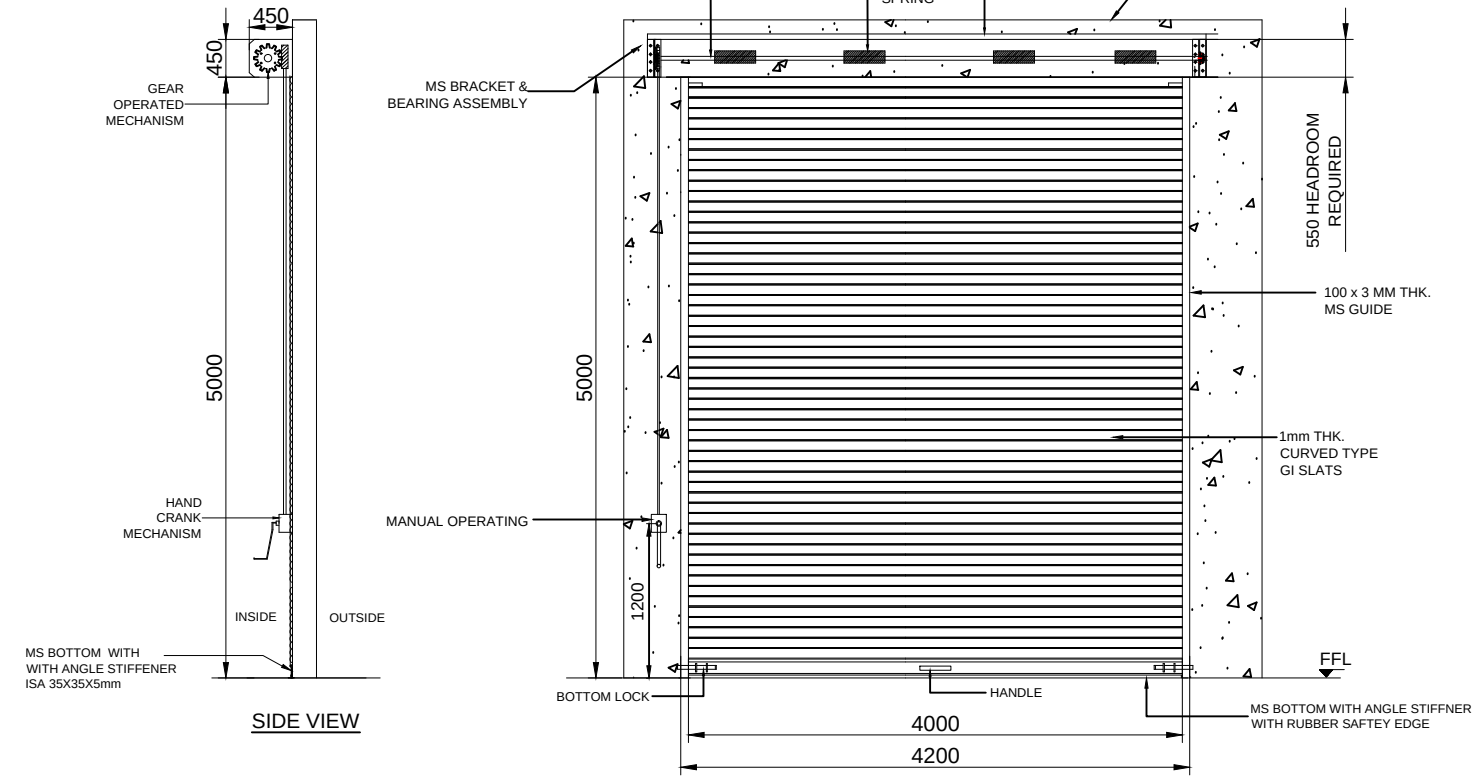


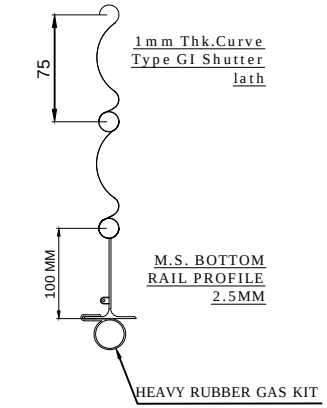

M.S. BOTTOM RAIL PROFILE 2.5MM

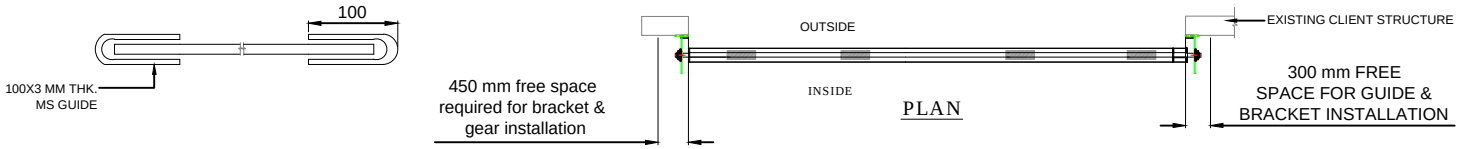

S.N.	LOCATION	SIZE	QUANTITY- Right side gearbox
1	B400	4000(W)X5000(H)	01
2	B500	4000(W)X5000(H)	-
3	B600	4000(W)X5000(H)	01
TOTAL QTY. OF SHUTTER			02

NOTE-
1. ALL CIVIL WORK WILL BE CLIENT'S SCOPE.
2.STRUCTURE REQUIRED FOR SHUTTER IS IN CLIENT'S SCOPE.
3.FINAL FINISH OF SHUTTER WILL BE IN POWDER COATING OF APPROVED COLOR i.e.RAL 7001.

TOLERANCE - ±10mm

REV:-28-04-2018 .01.Changed hand crank mechanism location.

This drawing & design is the property of NIHVA TECHNOLOGIES. Not to be sold or copied to any other concern.

TITLE: GEAR OPERATED ROLLING SHUTTER 4mX5m With Left side gearbox

	NAME	SIGN	DATE
DRAWN	OMKAR		28-04-2018
CHECK	PRADEEP		28-04-2018
APPRD.	PRADEEP		28-04-2018

NIHVA TECHNOLOGIES PVT. LTD.
NIHVA TECHNOLOGIES PVT. LTD. PUNE
Tel : 020 66304033
Email:- info@nihva.com
Website:- www.nihva.com

CLIENT - INDOSPACE
PROJECT - BUILDING B500 & B600
SITE LOCATION - CHAKAN 3

If any queries contact : design@nihva.com | DWG. NO. : NIHVA/18-19/0016/1 | REV- 0

ALL DIMENSION ARE IN mm | SCALE: NTS | WT: | SHEET: 01 OF 01