


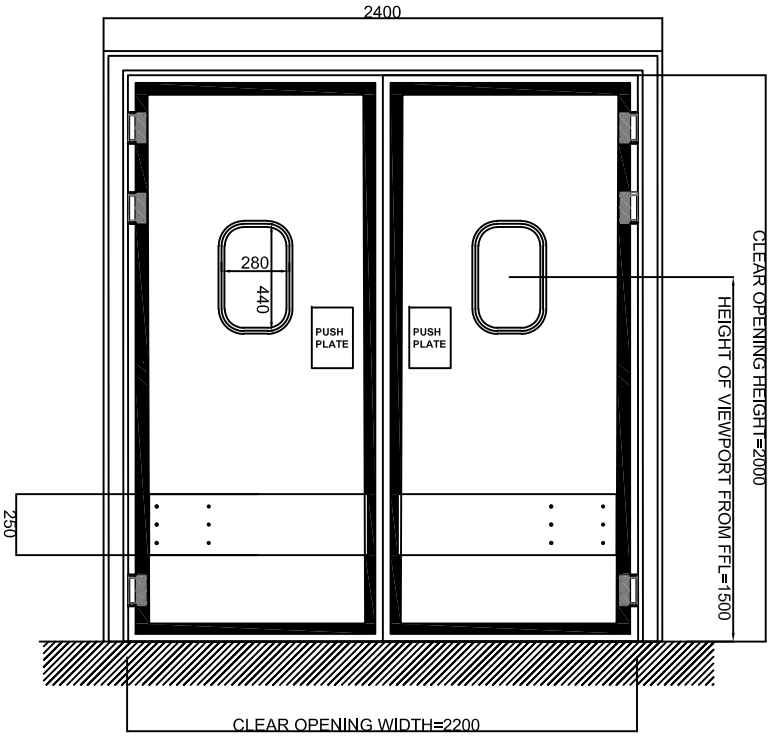


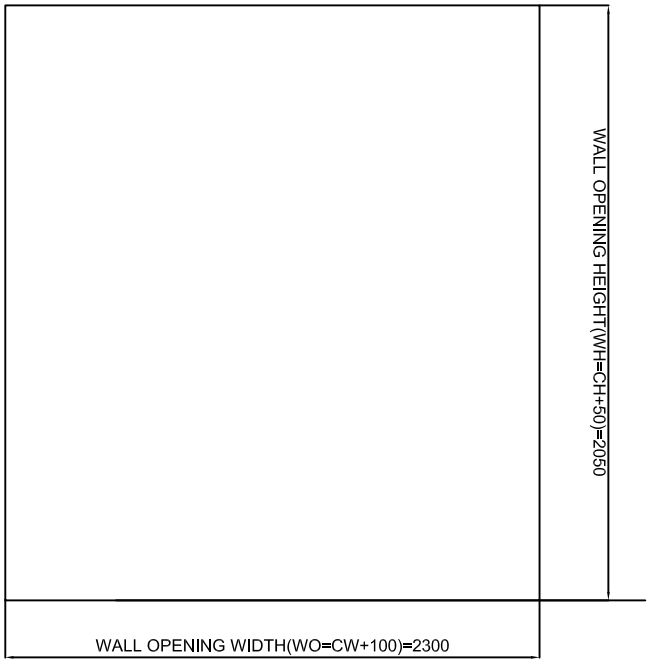

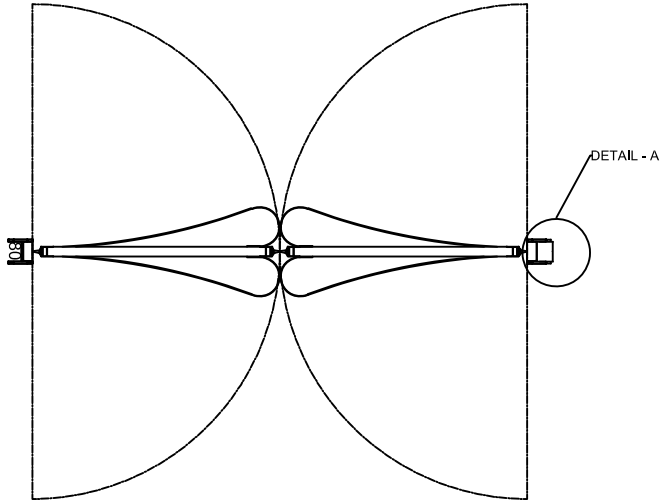

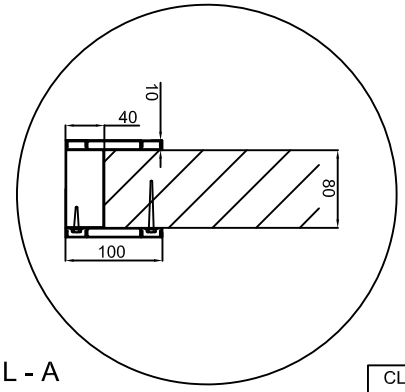

DETAIL - A

LEAF FINISH : SS FINISH
HINGES MOC : DOUBLE ACTION STAINLESS STEEL
VIEW WINDOW : 1 UNIT ON EACH LEAF
VIEW WINDOW HEIGHT : 440 MM
VIEW WINDOW WIDTH : 280 MM
VIEW WINDOW POSITION FROM FFL : 1500 MM

CLEAR OPENING WIDTH	CLEAR OPENING HEIGHT	QTY	LOCATION
2200 MM	2000 MM	1 NO	

This drawing & design is the property of NIHVA TECHNOLOGIES. Not to be sold or copied to any other concern.

TITLE FLIP FLAP DOOR

NIHVA TECHNOLOGIES PVT. LTD.
NIHVA TECHNOLOGIES PVT. LTD. PUNE
Tel : 020 66304033
Email:- info@nihva.com
Website:- www.nihva.com

	NAME	SIGN	DATE
DRAWN	S.M.S.		15.2.2021
CHECK	S.M.S.		15.2.2021
APPRD.			

If any queries contact : projectsupport@nihva.com

ALL DIMENSION ARE IN mm

CLIENT - TRANS ENGINEERS INDIA PVT LTD

PROJECT - MARS INTERNATIONAL INDIA PVT LTD

SITE LOCATION - PUNE

DWG. NO. : NIHVA/20-21/0160 REV- R00

SCALE: NTS WT: SHEET: