


PRODUCED BY AN AUTODESK EDUCATIONAL PRODUCT

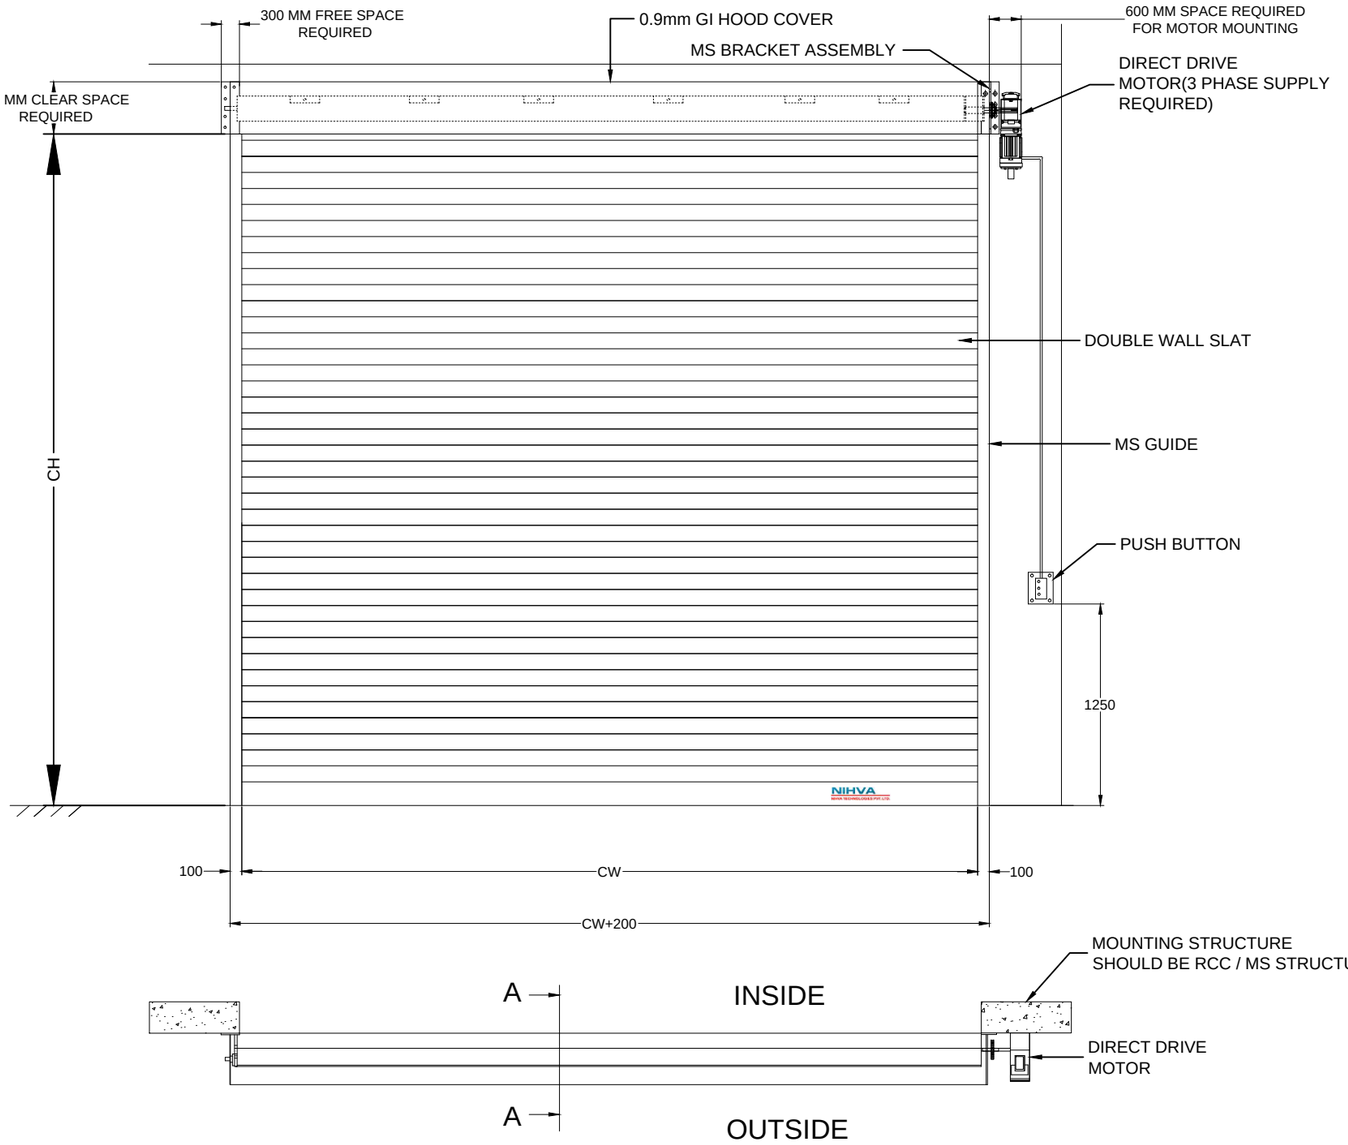


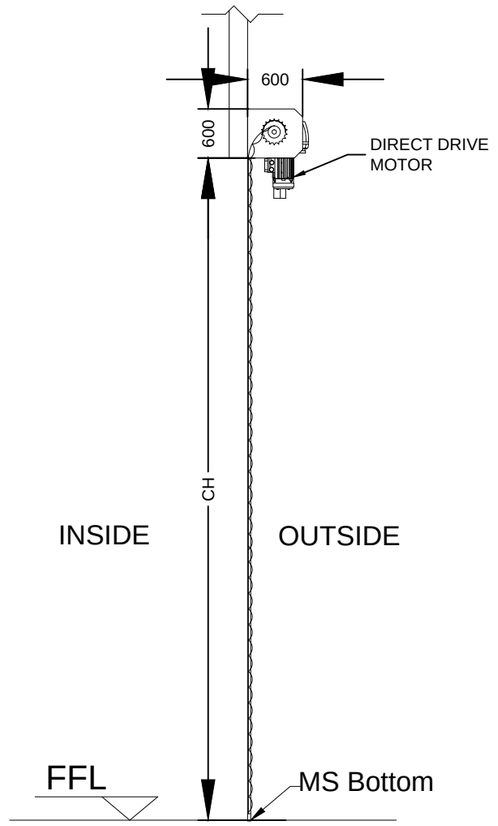

Section A-A

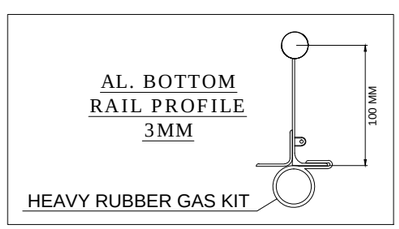

Main Slats
Double Wall Puff Rolling Shutter

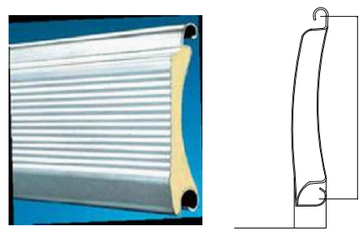

DIMENSION :

CLEAR WIDTH	CLEAR HEIGHT	QUANTITY
4900 mm	3900 mm	1 NOS

NOTE:-

1. 3 PHASE SUPPLY SHOULD BE PROVIDED.

NIHVA TECHNOLOGIES PVT. LTD.
NIHVA TECHNOLOGIES PVT. LTD. PUNE
Email:- info@nihva.com
Website:- www.nihva.com

TITLE:

DOUBLE WALL ROLLING SHUTTER
RS01. LGF south side
RS02. LGF south side

COLOR OF SLATS & SHUTTER -RAL9002 (GRAY WHITE)

CLIENT -

PROJECT -

SITE LOCATION -

DWG. NO. : NIHVA/21-22/VDR/017

SCALE: NTS	WT:	SHEET:01 OF 02
DRAWN BY: G.P.		DATE: 23-12-2021
CHECKED BY: A.K.		DATE: 23-12-2021
APPROVED BY :		

If any queries contact : design@nihva.com

NOTE: ALL DIMENSIONS ARE IN mm

THIS DRAWING & DESIGN IS THE PROPERTY OF NIHVA TECHNOLOGIES. NOT TO BE SOLD OR COPIED TO ANY OTHER CONCERN.

PRODUCED BY AN AUTODESK EDUCATIONAL PRODUCT

PRODUCED BY AN AUTODESK EDUCATIONAL PRODUCT