
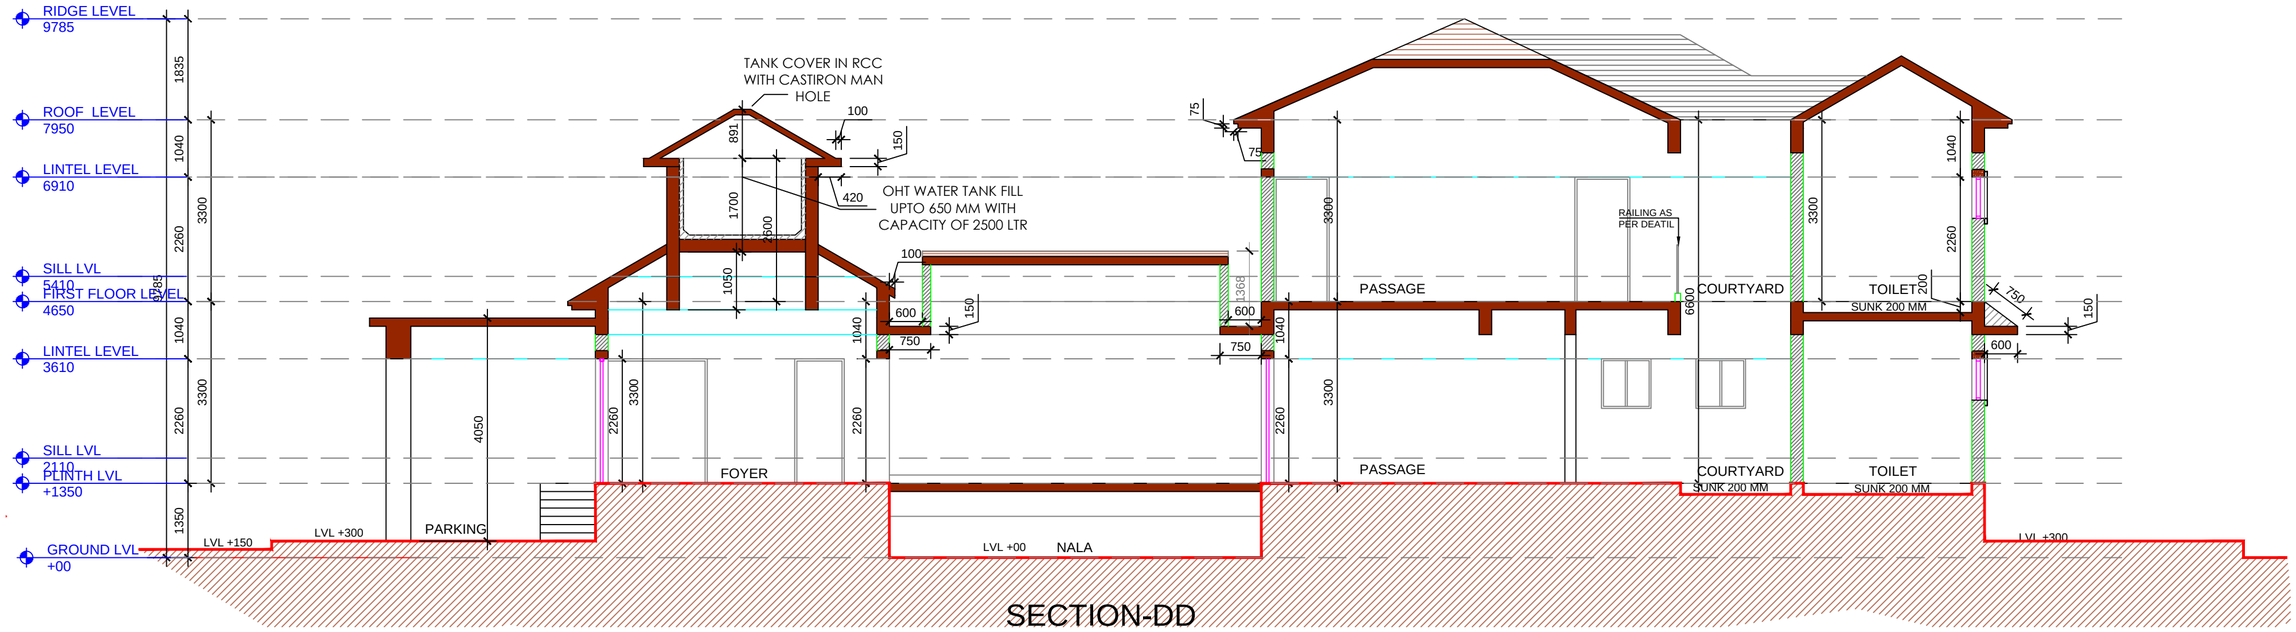



SECTION-DD

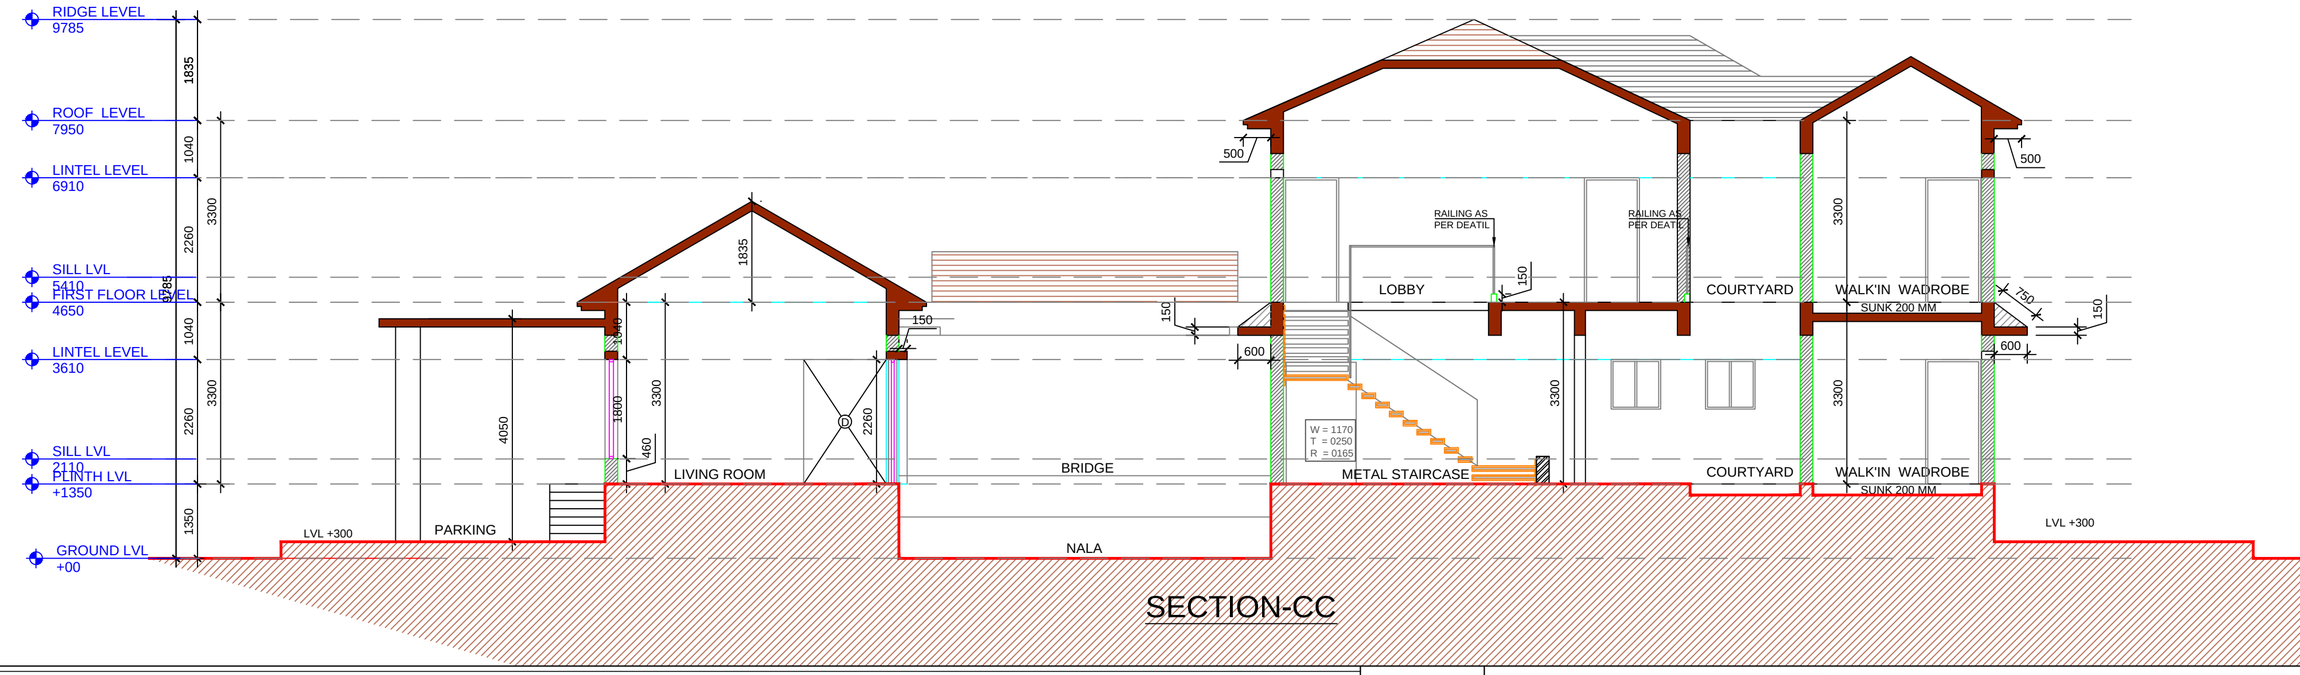


SECTION-CC

TITLE

| NO. | REVISION | DATE | PRINTS | ISSUED TO | DATE |
|---|---|---|---|---|---|
| | | | - | | |
| | | | - | | |
| | | | - | | |
| | | | - | | |
| | | | - | | |
| | | | - | | |

DWG. REMARK

GOOD FOR CONSTRUCTION

SCHEDULE OF CLEAR OPENING AFTER PLASTER

| DOOR | CODE | SIZE | CILL | LINTEL | NO. |
|---|---|---|---|---|---|
| | D | 1.50 X 2.26 | - | 2.26 | |
| | D1 | 0.90 X 2.26 | - | 2.26 | |
| | D2 | 0.80 X 2.26 | - | 2.26 | |
| | D3 | 1.00 X 2.26 | - | 2.26 | |
| | D4 | 1.94 X 2.26 | - | 2.26 | |
| | D5 | 2.27 X 2.26 | - | 2.26 | |
| | D6 | 2.72 X 2.26 | - | 2.26 | |
| | D7 | 1.30 X 2.26 | - | 2.26 | |
| | D8 | 2.00 X 2.26 | - | 2.26 | |

SCHEDULE OF CLEAR OPENING AFTER PLASTER

| WINDOW | CODE | SIZE | SILL | LINTEL | NO. |
|---|---|---|---|---|---|
| | W | - | 0.76 | 2.26 | |
| | W1 | 2.40 X 1.80 | 0.46 | 2.26 | |
| | W2A | 1.80 X 1.80 | 0.46 | 2.26 | |
| | W3 | 1.50 X 1.50 | 0.76 | 2.26 | |
| | W4 | 1.20 X 1.50 | 0.76 | 2.26 | |
| | W4A | 1.20 X 1.96 | 0.30 | BEAM | |
| | W5 | 0.90 X 0.90 | 1.36 | 2.26 | |
| | V | 0.60 X 0.75 | 1.51 | 2.26 | |

NOTES -

- ALL DESIGNS ARE PROPERTY OF THE ARCHITECTS PIYUSH KHADKE AND CANNOT BE USED WITHOUT THEIR PERMISSION.
- DO NOT SCALE THE DRAWINGS
- ALL MEASUREMENTS TO BE CHECKED AND VERIFIED ON SITE.
- ANY DISCREPANCIES IN DIMENSION BETWEEN DRAWING AND SITE MUST BE CLARIFIED WITH THE ARCHITECTS PRIOR TO EXECUTION.
- THIS DRAWINGS, DETAILS, SPECIFICATIONS, QUANITIES ETC. ARE BASED ON THE INFORMATION SUPPLIED BY THE OWNER / POWER OF ATTORNEY HOLDER, BUILDER, PROMOTER ETC.
- ALL PLANS ARE SUBJECT TO SANCTION OF CONCERED AUTHORITIES.
- THE ARCHITECT WILL NOT BE RESPONSIBLE FOR INCORRECT, BAD OR DEFECTIVE WORK.
- RESPONSSIBLE PARTY FOR CONSTRUCTION OWNER / CONTRACTOR .

NORTH

SIGN & STAMP

PROJECT

PROPOSED BUNGALOW

AT FOREST TRAIL, BHUGAON PUNE

MR.VIKAS BHILARE

SECTOR R10A_BHILARE BUNGALOW
S2 -213 + K2 - 214_


piyush khadke

architects & interior design consultants

4th floor , kavyanjali building opp. vishawas samrudhi society
vadgaon,pune-411041(MAH.)INDIA
mob no : +91 - 9595558119
email id : piyushdkhadke@gmail.com


| DATE | DRG.NO. | DWG BY | CHECKED BY | REVISION |
|---|---|---|---|---|
| 06.09.22 | R-3/20.09 | piyush | | R-2 |