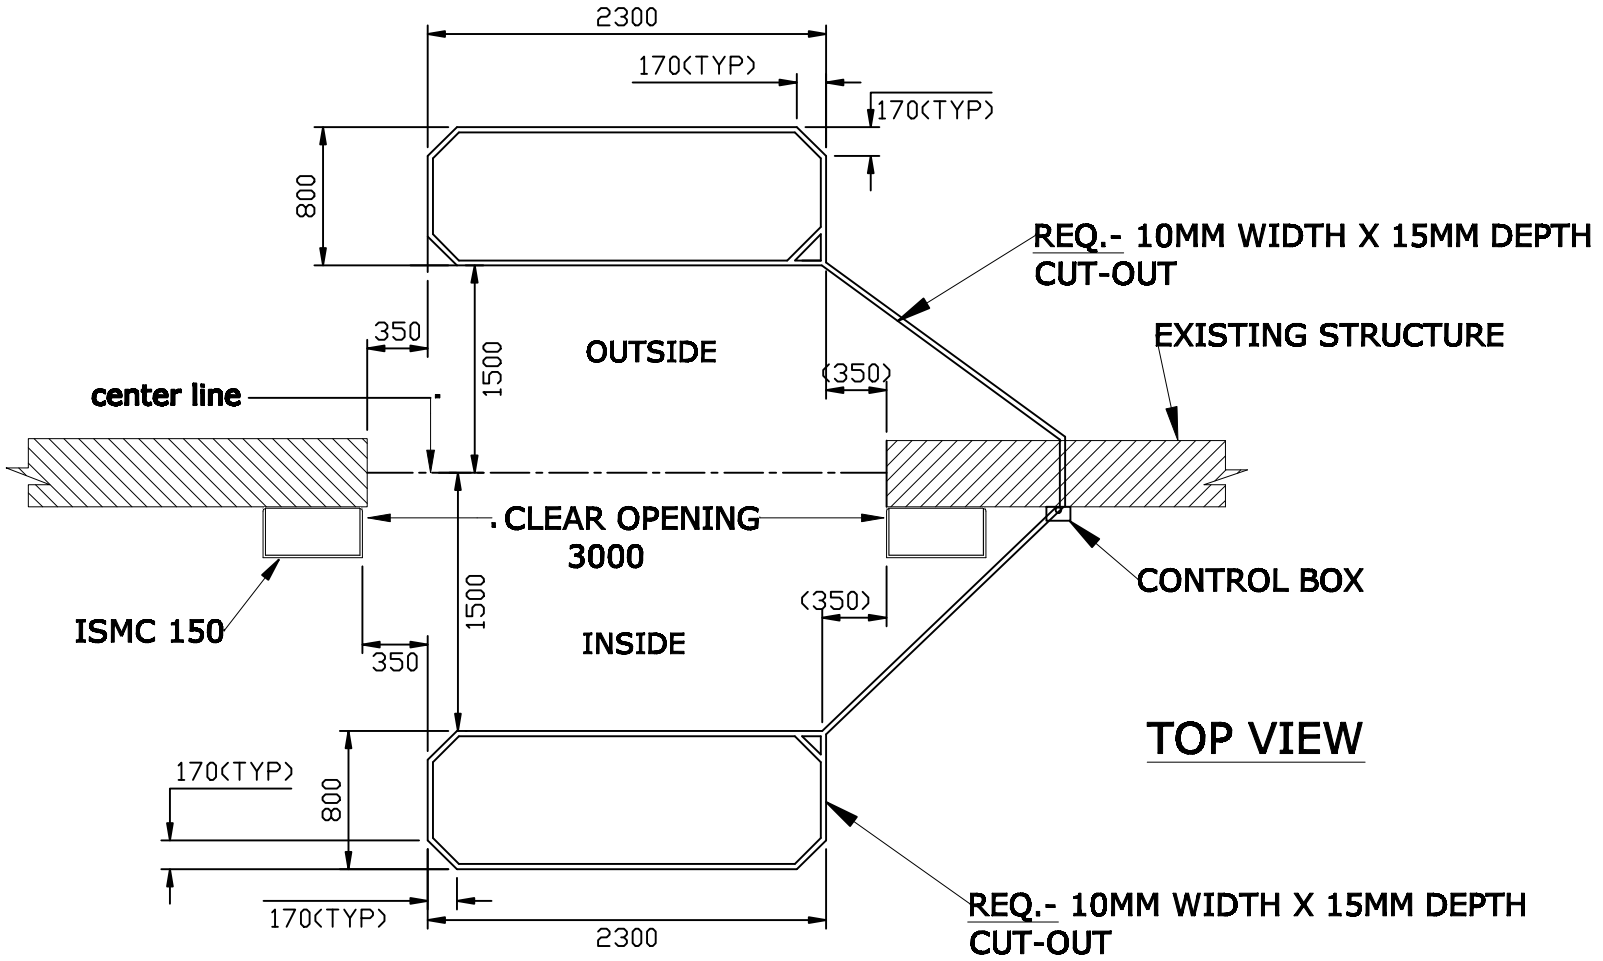


FLOOR CUT-OUT FOR LOOP DETECTOR FOR HIGH SPEED DOOR

This drawing & designing is the property of NIHVA TECHNOLOGIES. Not be sold or copy to any other concern.

TITLE: FLOOR CUT-OUT FOR LOOP DETECTOR FOR HIGH SPEED DOOR	ALL DIMENSION ARE IN mm		NIHVA TECHNOLOGIES PVT. LTD.
	SIGN	DATE	
DRAWN	ABHIJIT	11/07/15	CLIENT -FERRERO
CHECK	ANIL	11/07/15	PROJECT-FERRERO
ENG			SITE -BARAMATI
APPRD.			DWG. NO. - NVA/15-16/055
MFG			SCALE: 01 / WT: / SHEET: 01
Ref. No.			If any queries contact : projects@nihva.com
CLIENT APPROVAL			

NIHVA TECHNOLOGY PVT. LTD. PUNE
Tel : 020 66304033
Email:- info@nihva.com
Website:- www.nihva.com