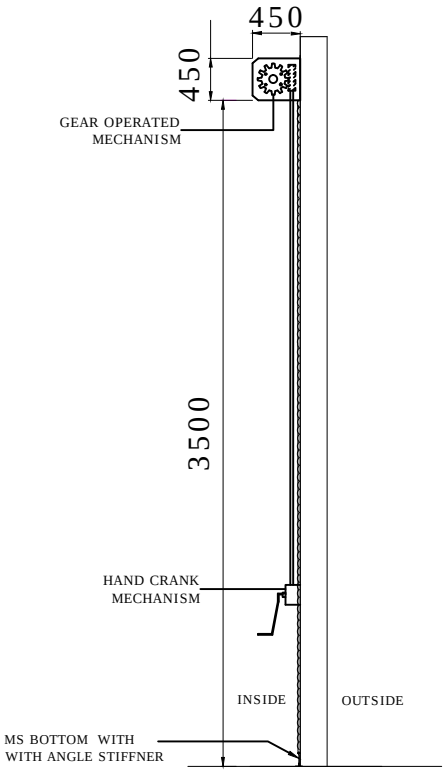


SIDE VIEW

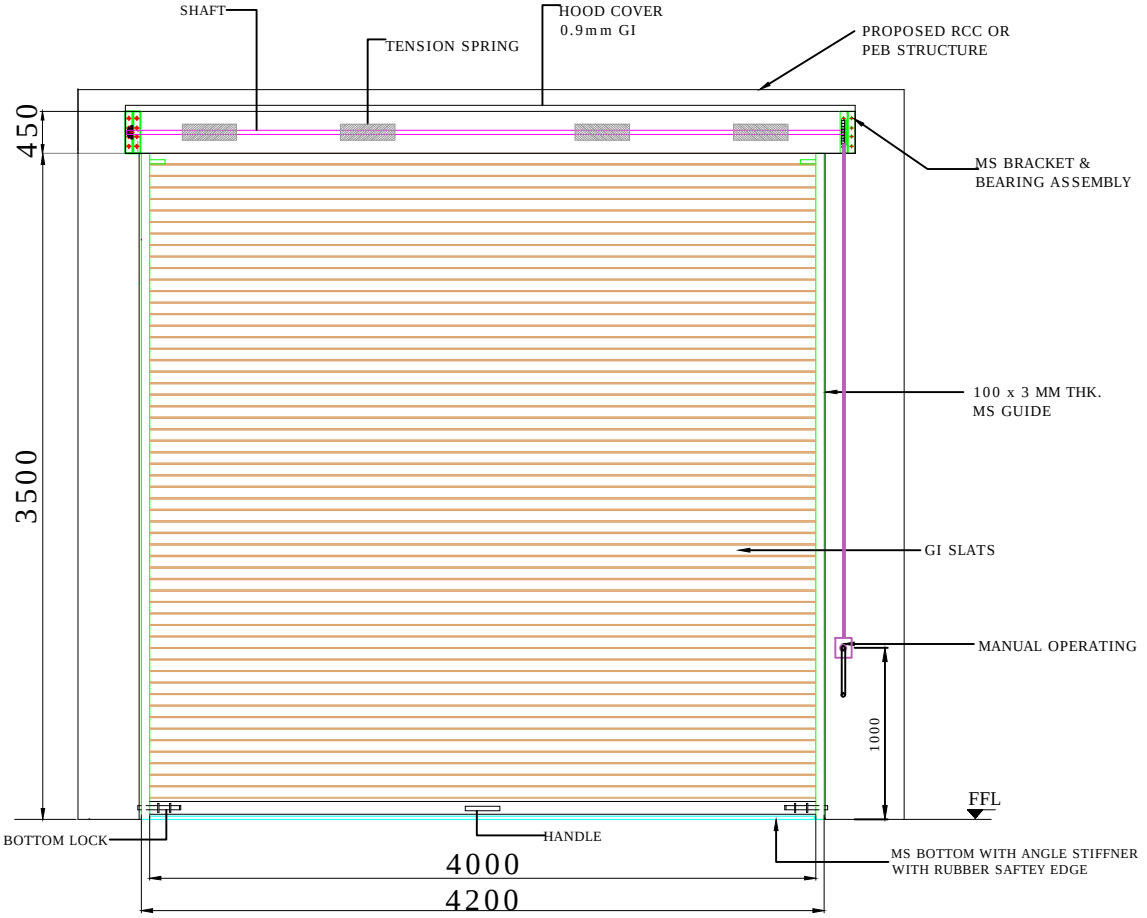


INSIDE ELEVATION

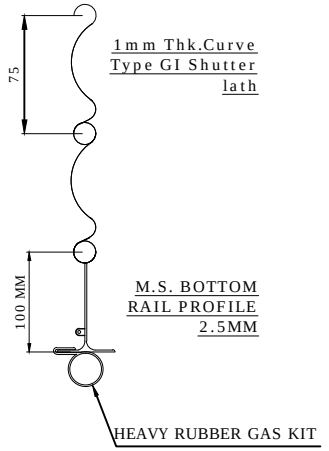


M.S. BOTTOM RAIL PROFILE 2.5MM

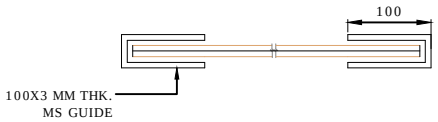

PLAN

NOTE:-
1. PAINTING WILL BE IN CLIENT'S SCOPE.
2. REQUIRED STRUCTURE WILL BE IN CLIENT SCOPE.

| CLEAR WIDTH (CW) | CLEAR HEIGHT (CH) | QUANTITY |
|---|---|---|
| 4000 | 3500 | 05 |

This drawing & designing is the property of NIHVA TECHNOLOGIES. Not to be sold or copied to any other concern.

TITLE: MANUAL ROLLING SHUTTER

| | NAME | DATE | SIGN |
|---|---|---|---|
| DRAWN | SURAJ | 13/02/18 | |
| CHECK | OMKAR | 13/02/18 | |
| APPROVAL | SHEKHAR | 13/02/18 | |

If any queries contact : design@nihva.com

ALL DIMENSION ARE IN mm

NIHVA TECHNOLOGIES PVT. LTD.
NIHVA TECHNOLOGIES PVT. LTD. PUNE
Tel : 020 66304033
Email:- info@nihva.com
Website:- www.nihva.com

CLIENT - MITTAL PRECISION HITECH STEEL PVT.LTD

PROJECT -

SITE - CHAKAN,PUNE

DWG. NO. : NIHVA/17-18/0359 | REV- 0

SCALE: NTS | WT: | SHEET: 01 OF 01