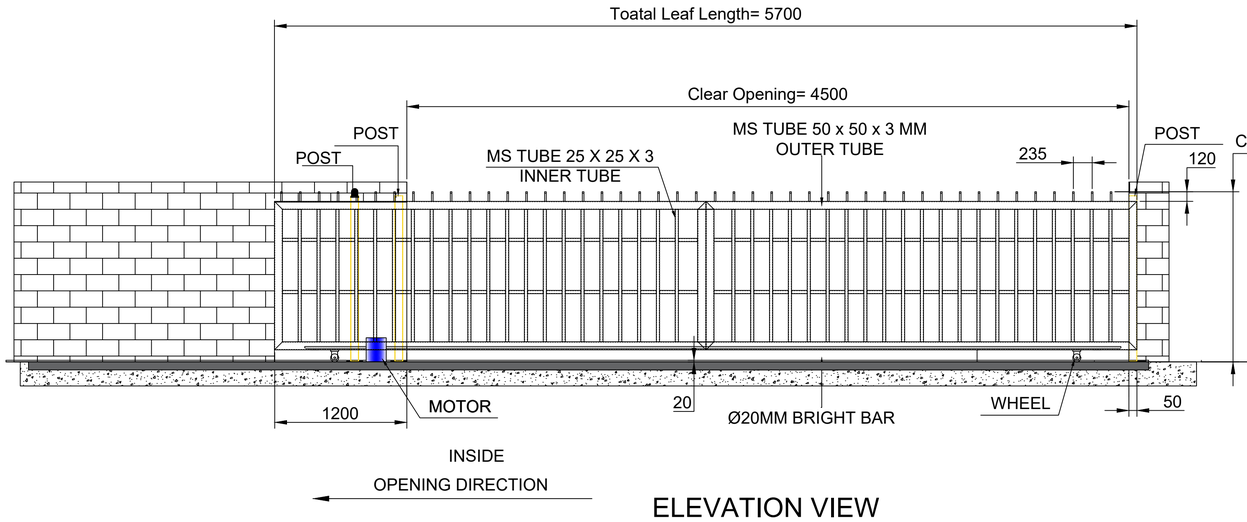
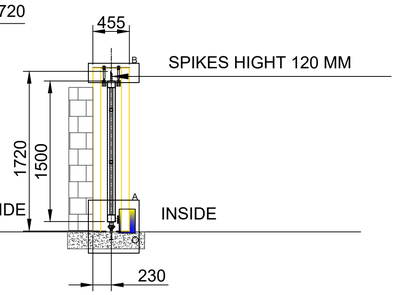
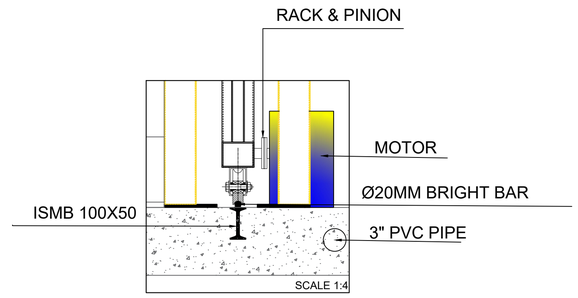


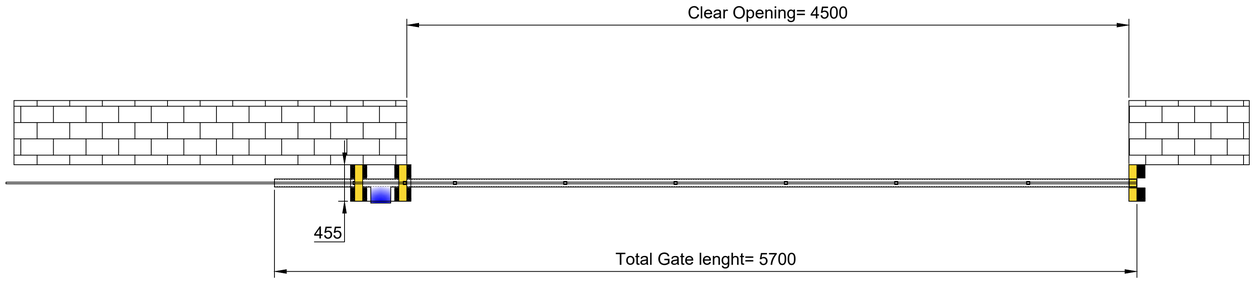

ELEVATION VIEW



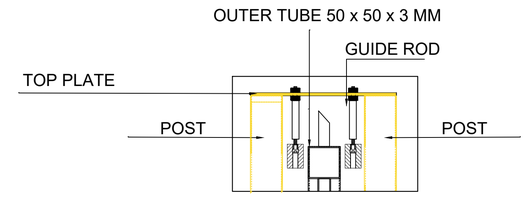

SIDE VIEW




DETAIL A




PLAN




DETAIL B
SCALE 1:4

Technical Specs of Motorized Sliding Gate

1. Opening length - 4500mm
2. Gate Height - 1720mm
3. Parking length required - 5700+100 mm
4. Outer tube size - MS SHS 50 x 50 x 3 mm
5. Inner tube size - MS SHS 25 x 25 x 3 mm
6. Bottom Rail - Bright bar Ø20mm
7. Post size - MS SHS 50 x 50 x 3 mm

Note-

1. All dimension are in mm.
2. All civil work is under client scope.
3. 3" PVC pipe in the foundation to be provided by client.
4. Power supply single phase 230v, 50hz.is in client scope
5. Cable for power supply 2.5 sqmm 3 core
6. Cable for photocell - 1.5 sqmm 4 core

| Rev No. | Revision | Date | Revised By |
|---|---|---|---|
| CAD PATH:- | | | |

This drawing & design is the property of NIHVA TECHNOLOGIES. Not to be sold or copied to any other concern.

TITLE:-
MOTORISED SLIDING GATE

NIHVA TECHNOLOGIES PVT. LTD.

NIHVA TECHNOLOGIES PVT. LTD. PUNE
Tel : 020 66304033
Email:- info@nihva.com
Website:- www.nihva.com

| | NAME | DATE | SIGN |
|---|---|---|---|
| DRAWN | M.SUTAR | 04-08-2022 | |
| CHECK | M.SUTAR | 04-08-2022 | |
| APPRD. | A.KURHADE | 04-08-2022 | |

CLIENT - GMR GOA INTERNATIONAL AIRPORT LIMITED
LOCATION - GOA
PRODUCT - MOTORISED SLIDING GATE
If any queries contact : design@nihva.com
DWG NO:- NIHVA/22-23/CLT/0099 | REV- 0
ALL DIMENSION ARE IN mm
SCALE: NTS | SCALE:-- 1:1 | SHEET: 01 OF 01