


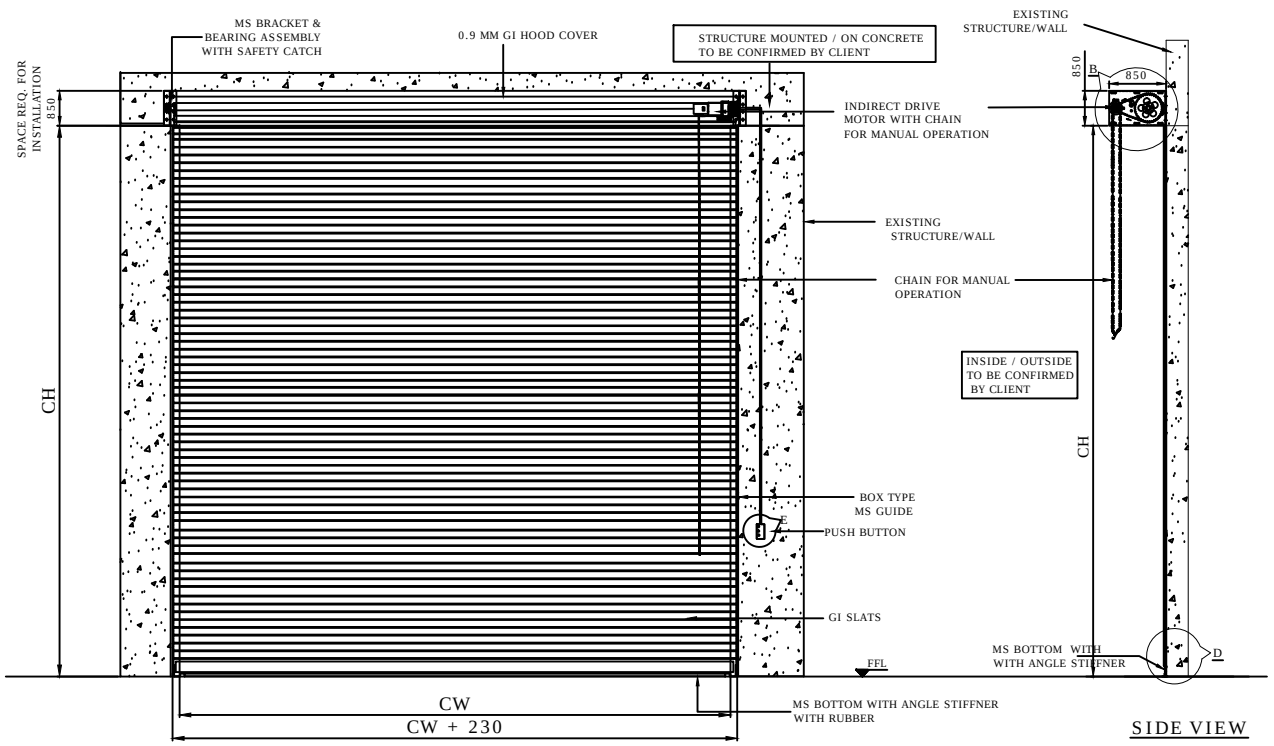


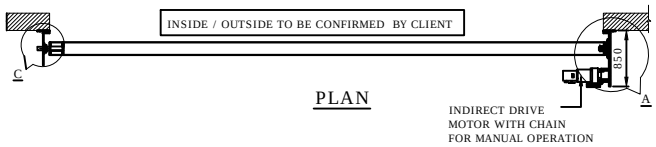


PLAN

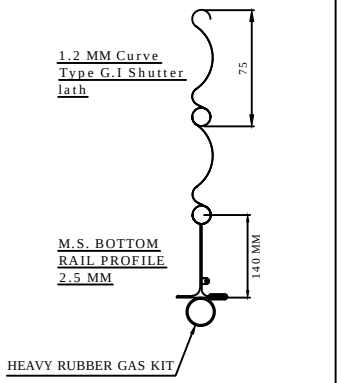


DETAILS : D

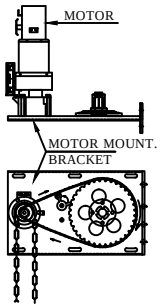

DETAILS : A & B

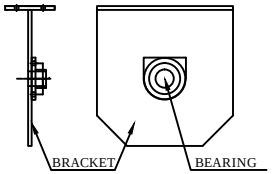

DETAILS : C

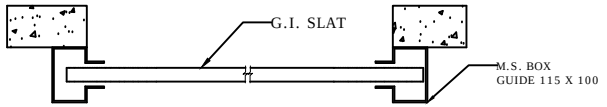

RAL CODE	SHADE	COLOUR
RAL 9001	CREAM	
RAL 9002	GREY WHITE	
RAL 9010	PURE WHITE	
RAL 5002	ULTRAMARINE BLUE	
RAL 7035	LIGHT GREY	
RAL 7001	SILVER GREY	

SR NO	CLEAR WIDTH(CW)	CLEAR HEIGHT(CH)	QTY	RAL CODE (POWDER COATING)
2	6000 MM	6200 MM	2 NOS	TO BE CONFIRMED BY CLIENT
1	6000 MM	8200 MM	4 NOS	TO BE CONFIRMED BY CLIENT

NOTES-

(1) KINDLY REFER PROVIDED STANDARD RAL SHADE TABLE & PROVIDE CONFIRMATION OF RAL CODE FOR POWDER COATING. IF OTHER THAN SPECIFIED , KINDLY MENTION .
(2) LOCATION OF MOTORIZED ROLLING SHUTTER TO BE CONFIRMED BY CLIENT .
(3) MOUNTING ON CONCRETE/PEB WALL OR EXISTING STRUCTURE TO BE CONFIRMED BY CLIENT .
(4) MS STRUCTURE WILL BE REQUIRED IN CASE OF MOUNTING ON PEB WALL & DRAWING WILL BE SHARED AFTER CONFIRMATION OF INSTALLATION .
(5) IF REQUIRED MS STRUCTURE , FITTING & STRUCTURE WILL BE IN CLIENT SCOPE.
(6) ALL REQUIRED CIVIL WORK IN CLIENT SCOPE .
(7) IF REQUIRED M.S. STRUCTURE, SHUTTER WILL BE ONLY INSTALLED AFTER READINESS OF STRUCTURE AS PER DRAWING PROVIDED.

This drawing & design is the property of NIHVA TECHNOLOGIES. Not to be sold or copied to any other concern.

TITLE: MOTORIZED ROLLING SHUTTER

	NAME	SIGN	DATE
DRAWN	SIDDHESHWAR		28.11.2020
CHECK	SIDDHESHWAR		28.11.2020
APPRD.			

If any queries contact : projectsupport@nihva.com

ALL DIMENSION ARE IN mm

NIHVA TECHNOLOGIES PVT. LTD.
NIHVA TECHNOLOGIES PVT. LTD. PUNE
Tel : 020 66304033
Email:- info@nihva.com
Website:- www.nihva.com

CLIENT - GS PEB & CIVIL WORKS PVT LTD
PROJECT - SANY HEAVY INDUSTRY INDIA PVT LTD
SITE LOCATION - ALANDIPHATA , PUNE
DWG. NO. : NIHVA/20-21/0069 | REV- R00
SCALE: NTS | WT: | SHEET: