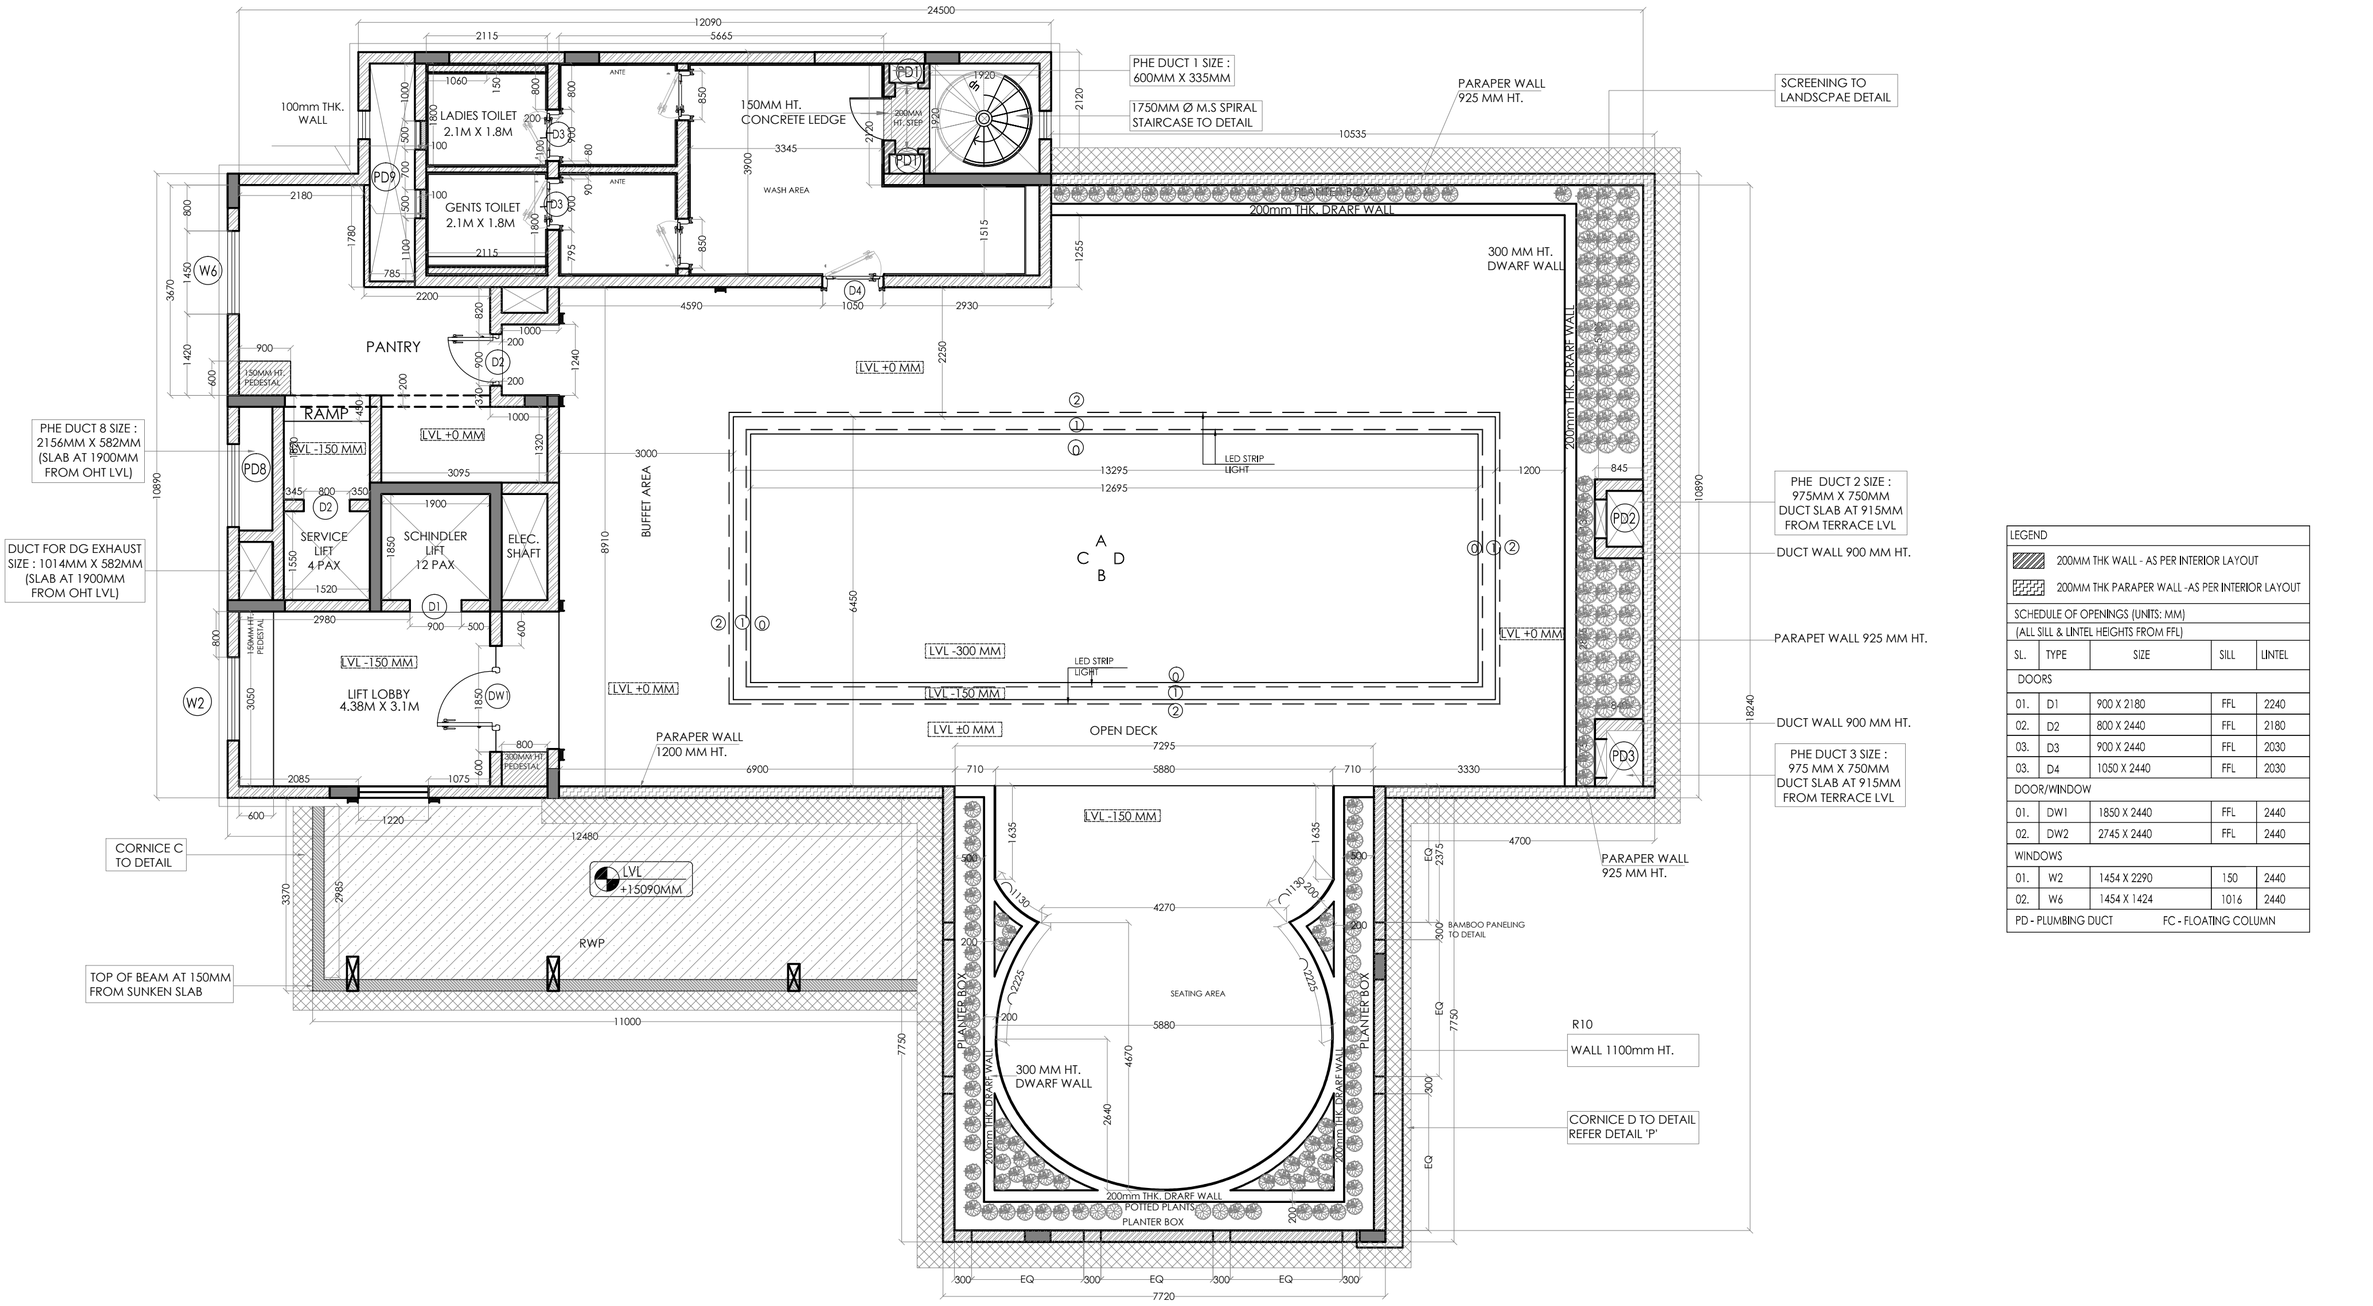


LEGEND				
200MM THK WALL - AS PER INTERIOR LAYOUT				
200MM THK PARAPER WALL -AS PER INTERIOR LAYOUT				
SCHEDULE OF OPENINGS (UNITS: MM)				
(ALL SILL & LINTEL HEIGHTS FROM FFL)				
SL.	TYPE	SIZE	SILL	LINTEL
DOORS				
01.	D1	900 X 2180	FFL	2240
02.	D2	800 X 2440	FFL	2180
03.	D3	900 X 2440	FFL	2030
03.	D4	1050 X 2440	FFL	2030
DOOR/WINDOW				
01.	DW1	1850 X 2440	FFL	2440
02.	DW2	2745 X 2440	FFL	2440
WINDOWS				
01.	W2	1454 X 2290	150	2440
02.	W6	1454 X 1424	1016	2440
PD - PLUMBING DUCT		FC - FLOATING COLUMN		

CIVIL LAYOUT
TERRACE FLOOR