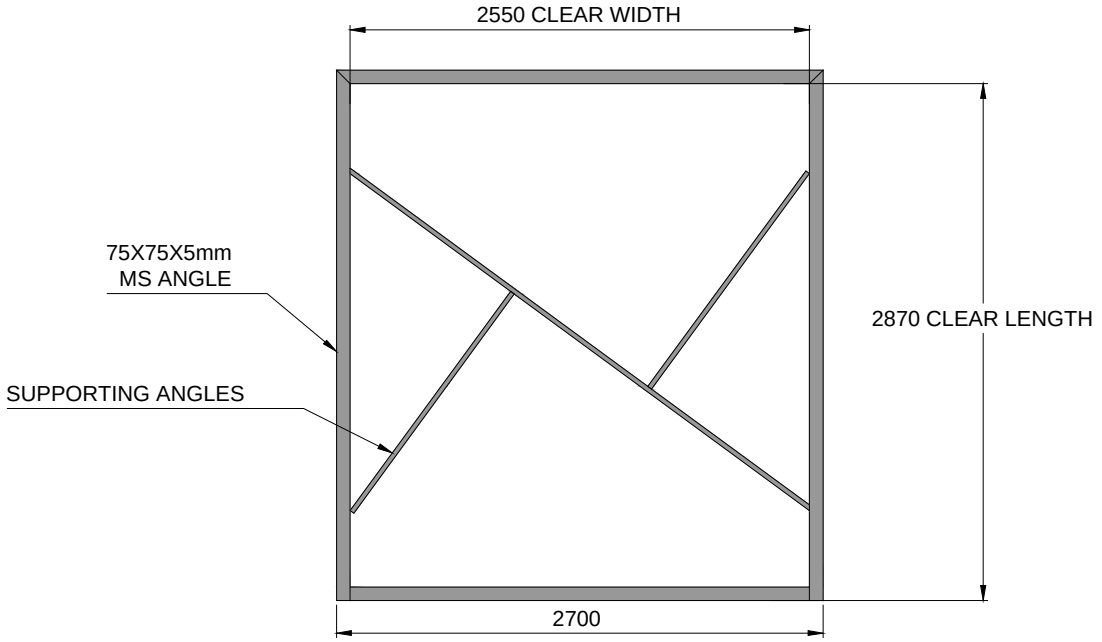

PLAN

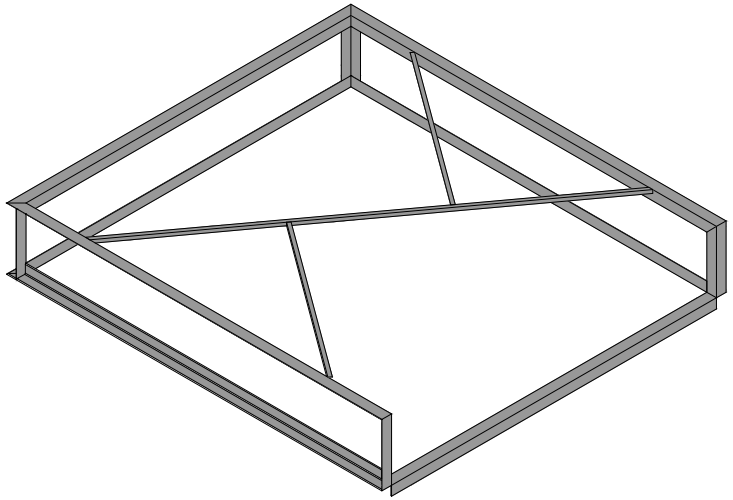

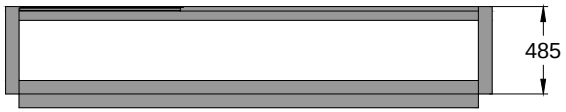

ELEVATION

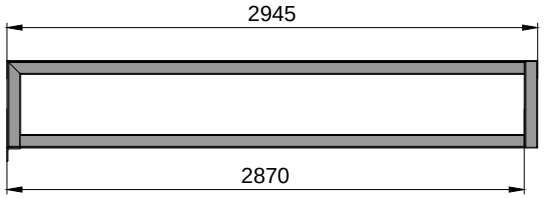

SIDE VIEW

NOTE- ONE COAT OF RED OXIDE PRIMER WILL BE GIVEN TO THE PIT.

This drawing & design is the property of NIHVA TECHNOLOGIES. Not to be sold or copied to any other concern.

TITLE: DOCK LEVELER FABRICATED PIT		NIHVA TECHNOLOGIES PVT. LTD. PUNE Tel : 020 66304033 Email:- info@nihva.com Website:- www.nihva.com
	SIGN	DATE
DRAWN	OMKAR	22/04/17
CHECK	SAGAR P.	22/04/17
REV.		
APPROVAL		
If any queries contact : projects@nihva.com		CLIENT - BAJAJ AUTO LIMITED
		PROJECT -
		SITE - AURANGABAD
		DWG. NO. : NIHVA/17-18/0023
ALL DIMENSION ARE IN mm		SCALE: NTS / WT: / SHEET: 01 OF 01