
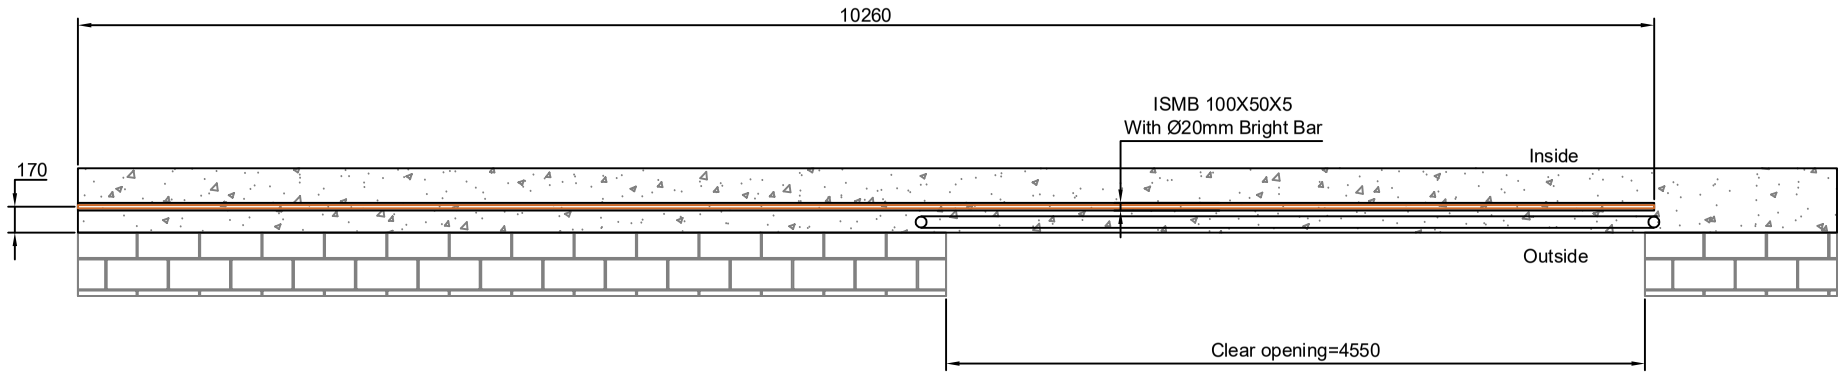


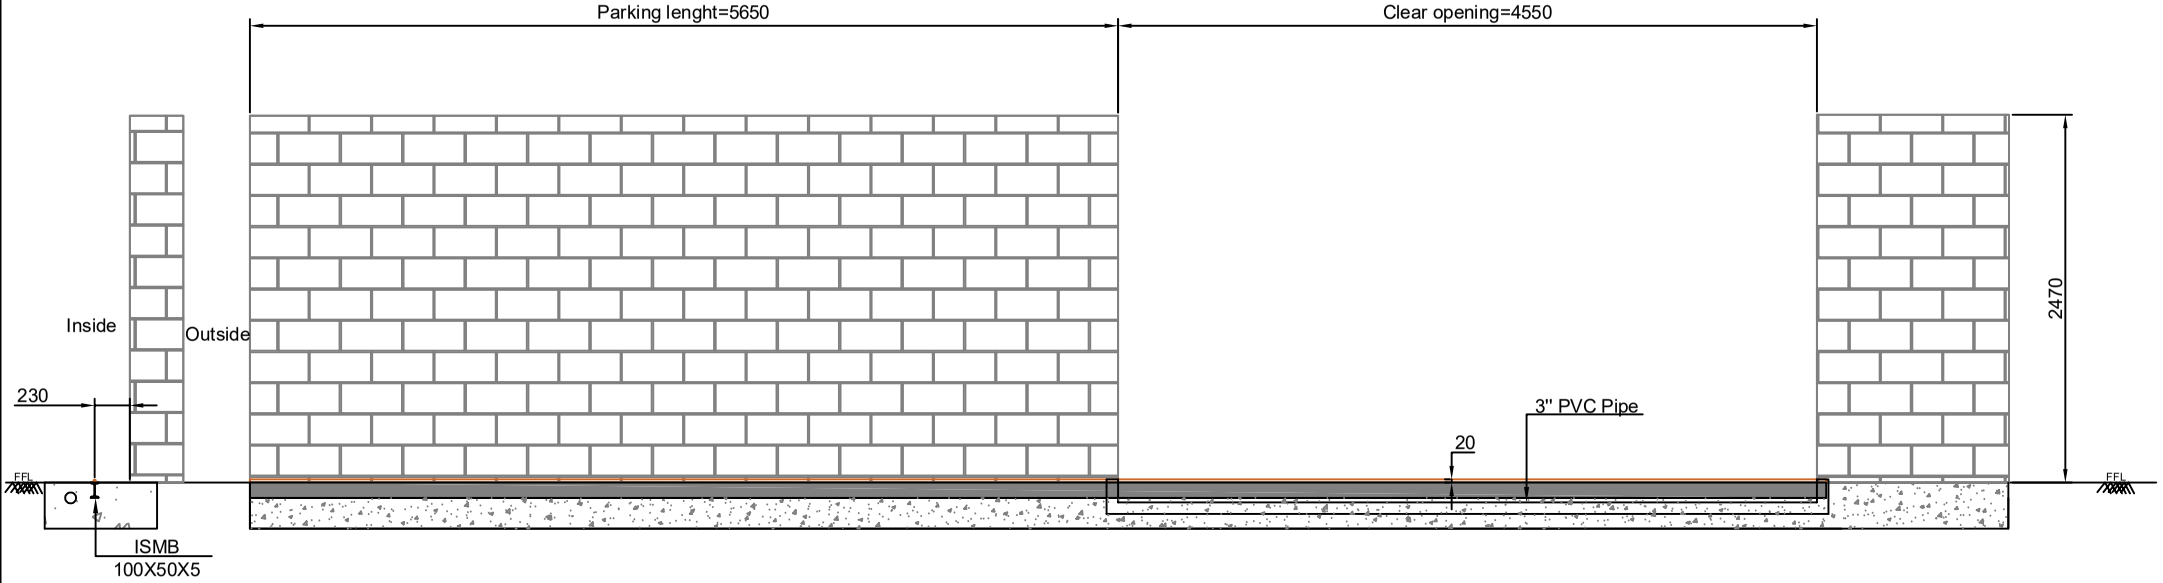

Note:-

1.All Dimension are in MM.

2. Required all civil work is in Client Scope.

3.Installation and Fabrication tolerance will be ±20mm.

4.Required Parking will be 5750.

Rev No.	Revision	Date	Revised By

This drawing & design is the property of NIHVA TECHNOLOGIES. Not to be sold or copied to any other concern.

TITLE:-
Sliding Gate with Wicket Gate_FDN

NIHVA
NIHVA TECHNOLOGIES PVT. LTD.

NIHVA TECHNOLOGIES PVT. LTD. PUNE
Tel : 020 66304033
Email:- info@nihva.com
Website:- www.nihva.com

	NAME	DATE	SIGN
DRAWN	SUJATA	26/07/2022	
CHECK	M.S	26/07/2022	
APPRD.	A.K	26/07/2022	

If any queries contact : design@nihva.com

ALL DIMENSION ARE IN mm

CLIENT - Rohit Nair

LOCATION - Undri

PRODUCT - Sliding Gate | QTY-

DWG NO:- NIHVA/22-23/CLT/0095 | REV-00

SCALE: NTS | SCALE:-- 1:1 | SHEET: 01 OF 01