

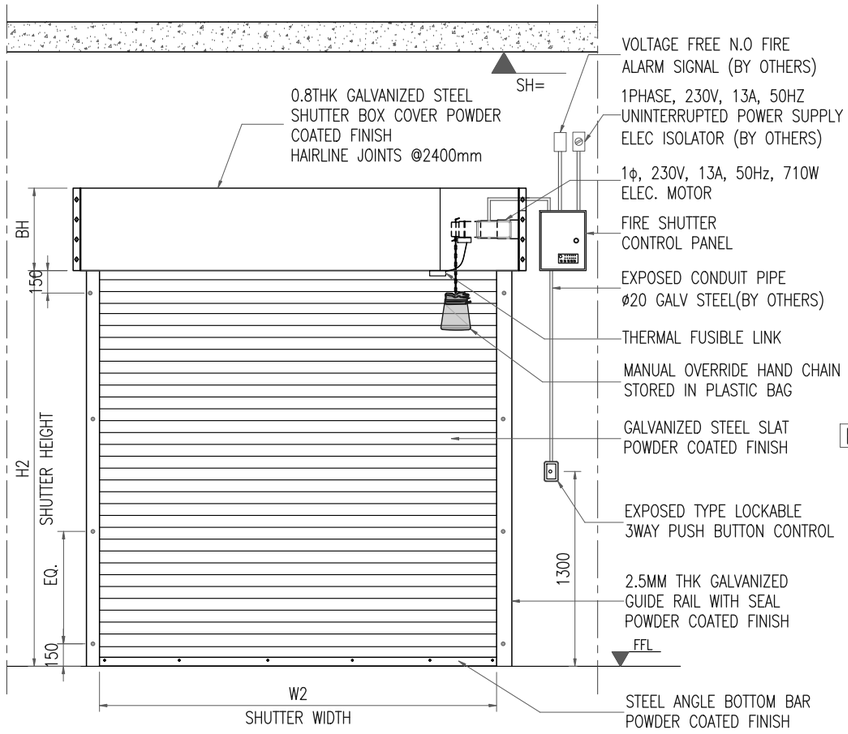


A / - INTERIOR ELEVATION
SCALE: 1:40

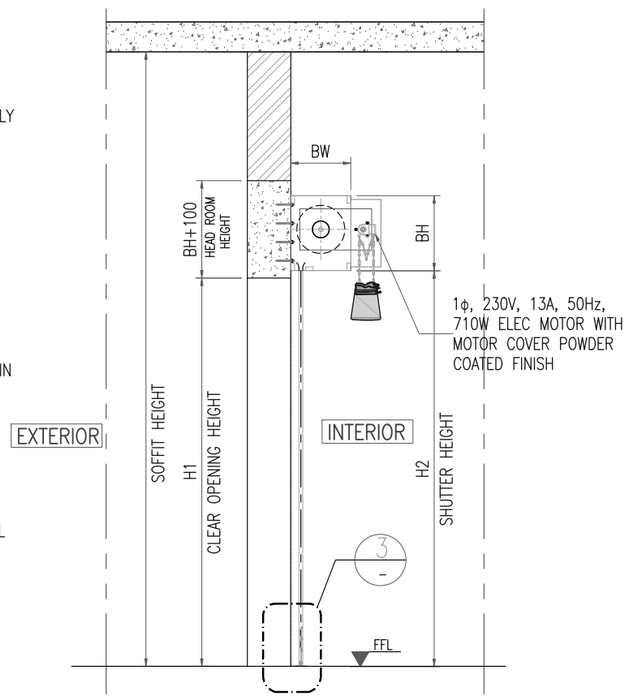


A1 / - SECTION
SCALE: 1:40

2HRS FIRE RATED ROLLER SHUTTER – SCHEDULE										
			OPENING SIZE		SHUTTER SIZE		HEAD BOX SIZE		MOTOR LOCATION	SHUTTER FINISH
S.NO	SHUTTER REF.	QTY	W1	H1	W2	H2	BW	BH		
1	FRS-1	1	2700	4000	2750	4050	500	600	TBC	TBC
2	FRS-2	1	2700	4000	2750	4050	500	600	TBC	TBC
3	FRS-3	1	2700	4000	2750	4050	500	600	TBC	TBC

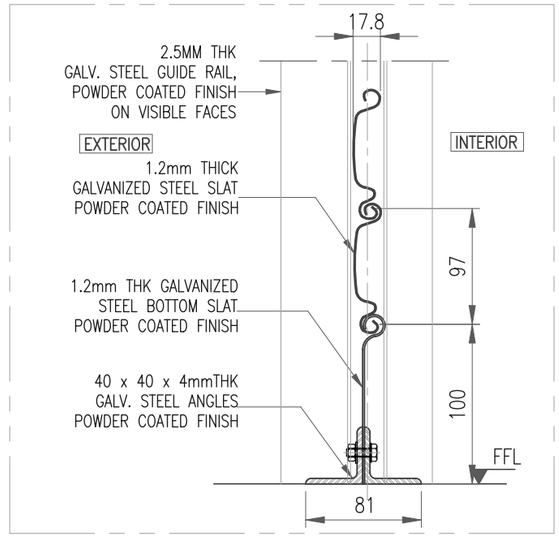


3 / - ENLARGED VIEW
SCALE: 1:4

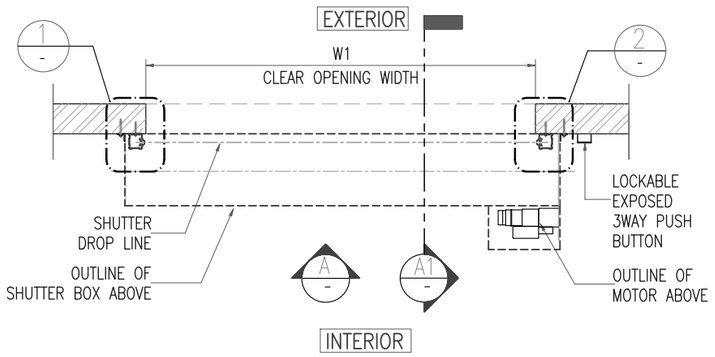

PLAN– 2HRS SINGLE SKIN ROLLER SHUTTER
SCALE: 1:40

SPECIFICATIONS (2HRS FIRE RATED SHUTTER) :-

SLAT	1.2mm THK GALVANIZED STEEL SINGLE SKIN SLAT, POWDER COATED FINISH
SIDE GUIDE	2.5mmTHK GALV. STEEL 'G' TYPE GUIDE POWDER COATED FINISH
END PLATE	MS PLATE, GREY PRIMER COATED
BOTTOM ANGLE	4mmTHK x 40 x 40 STEEL ANGLE BOTTOM BAR, POWDER COATED FINISH
SHUTTER BOX COVER	0.8mmTHK GALVANIZED STEEL, POWDER COATED FINISH
MOTOR COVER	0.8mmTHK GALVANIZED STEEL, POWDER COATED FINISH
MODE OF OPERATION	ELECTRICAL
POWER SUPPLY	1 PHASE, 230V, 13A, 50Hz ISOLATOR
FIRE ALARM SIGNAL	VOLTAGE FREE NORMALLY OPEN SIGNAL
AUTO CLOSING DEVICE	1) THERMAL FUSIBLE LINK
	2) FIRE ALARM SIGNAL
ACCESSORIES	1) 3 WAY PUSH BUTTON
	2) MANUAL OVERRIDE CHAIN

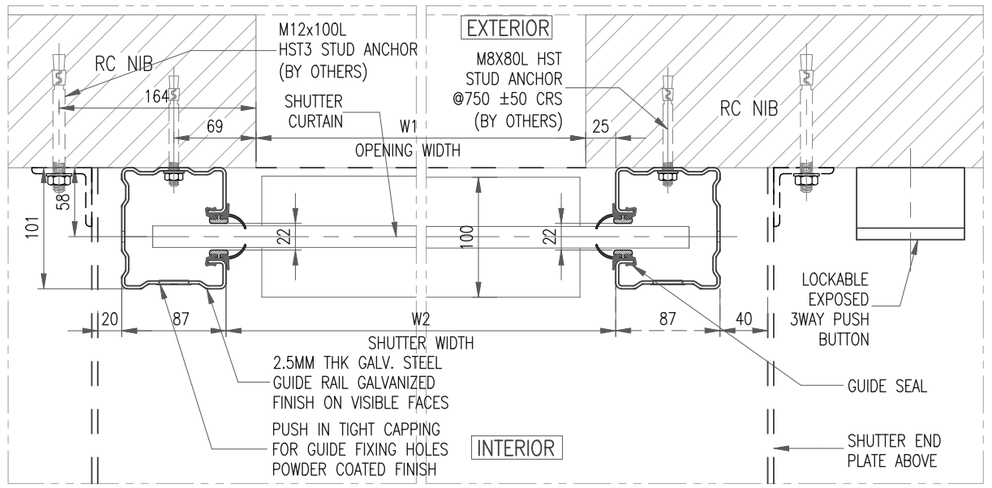

1 / - ENLARGED VIEW
SCALE: 1:5

2 / - ENLARGED VIEW
SCALE: 1:5

COLOR OF POWDER COATING FINISH : TBC	
PARTS	FINISH
GALV. STEEL SLAT	POWDER COATED FINISH
BOTTOM BAR	POWDER COATED FINISH
GALV. STEEL GUIDE RAIL	POWDER COATED FINISH
BOX COVER,	POWDER COATED FINISH

NOTE :
ALL DIMENSIONS ARE IN MILLIMETERS UNLESS OTHERWISE STATED.

Rev.	Date	By	Description	Checked	Approved
0	30.01.26	PS	FOR APPROVAL	SK	

ferco FERCO SHUTTERS AND SEATING SYSTEMS PRIVATE LIMITED
Survey No.8/1A2B,8/2A2, Industrial Shed, Parivakkam Road, Senneerkuppam, Poonamallee, Chennai 600056.

Contractor :
M/S. NIHVA TECHNOLOGIES
PUNE

Project Title :
SUPPLY OF 2HRS FIRE SHUTTER

Drawing Title :
2HRS FIRE RATED ROLLER SHUTTER PLAN,ELEVATION,SECTION & DETAILS

Designed	Checked	Approved
PS	SK	
Scale: As shown	Drawn: PS	Date: 30.01.2026

Drawing No. : FER-NHT-FRS-SD-002 | Rev. 0 | Sheet 2 of 3
CAD File Name : FER-NHT-FRS-SD-001_0.dwg | A3
Date Printed: 30-Jan-26

File Path: \\design1\Shared-Design\Projects dwgs - 2025\1.QUOTE STAGE PROJECTS\F25-26-099 - Nihva technologies - FRS - S\Shop Drawing