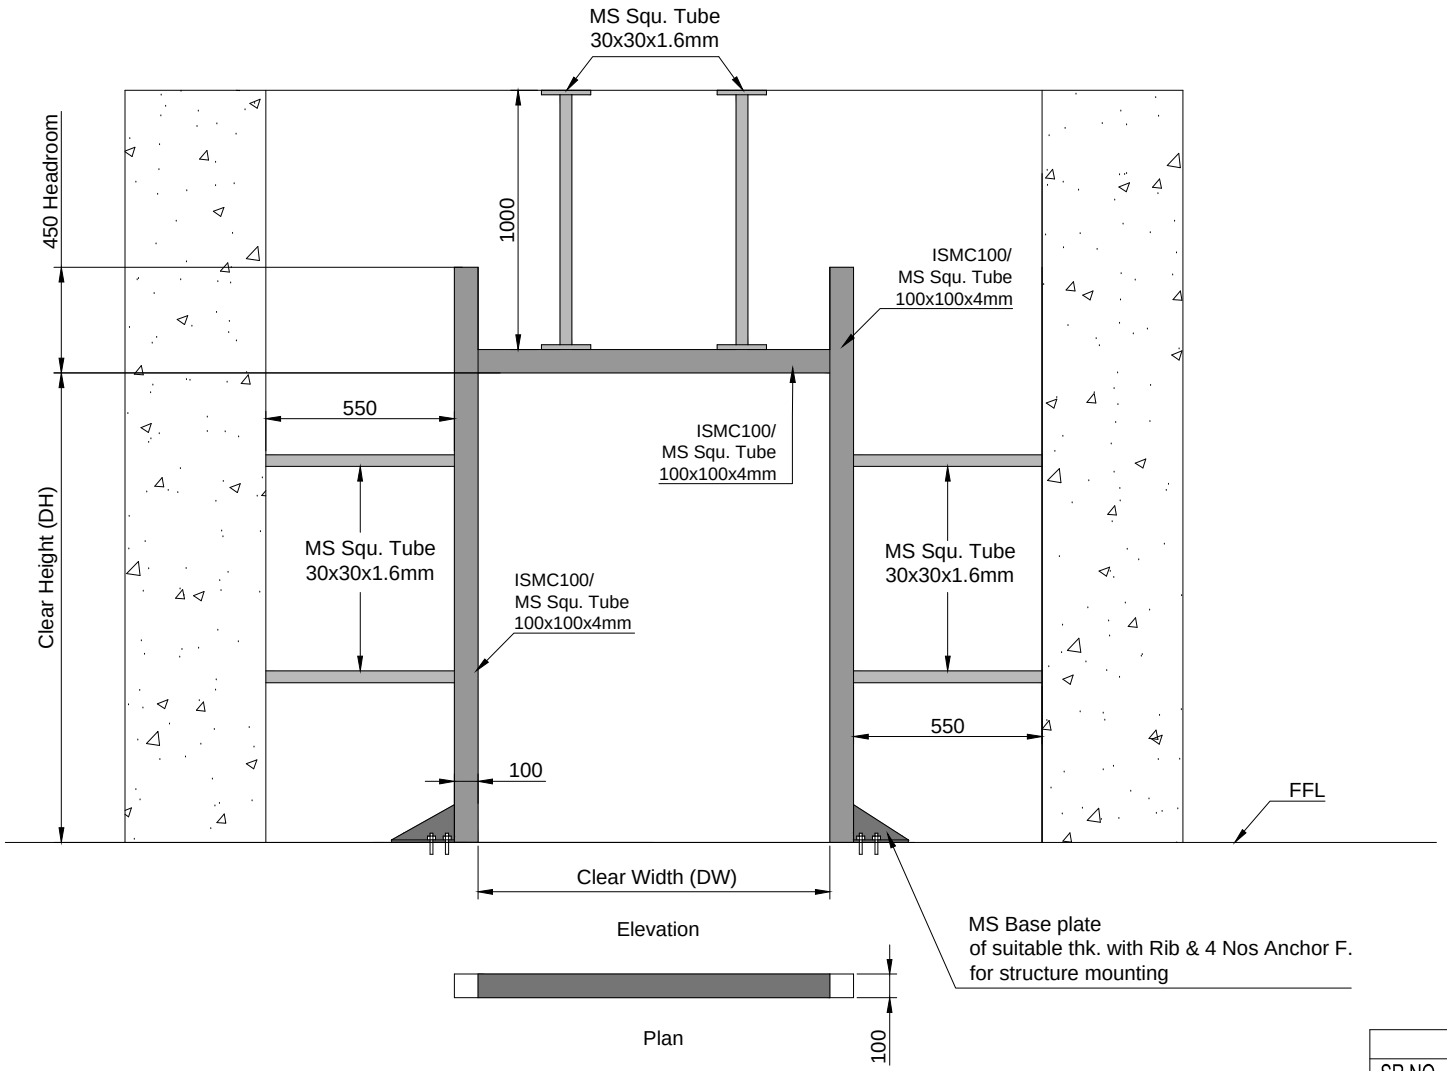

DOOR DIMENSION				
SR NO	DW	DH	MOTOR LOCATION	QUANTITY
1	2200	2100	RIGHT HAND SIDE	01

This drawing & designing is the property of NIHVA TECHNOLOGIES. Not to be sold or copied to any other concern.

TITLE: STRUCTURE FOR HSD HS9020G

NIHVA TECHNOLOGIES PVT. LTD. PUNE
Tel : 020 66304033
Email:- info@nihva.com
Website:- www.nihva.com

	NAME	SIGN	DATE
DRAWN	SURAJ		16/07/18
CHECK	PRADEEP		16/07/18
APPROVAL	R.D		16/07/18

If any queries contact : design@nihva.com

ALL DIMENSION ARE IN mm

CLIENT - FIBRO INDIA

PROJECT -

SITE - CHAKAN.

DWG. NO. : NIHVA/18-19/0086 | REV- 02

SCALE: NTS | WT: | SHEET: 01 OF 01

Note-
1. All Civil work will be in clients scope.