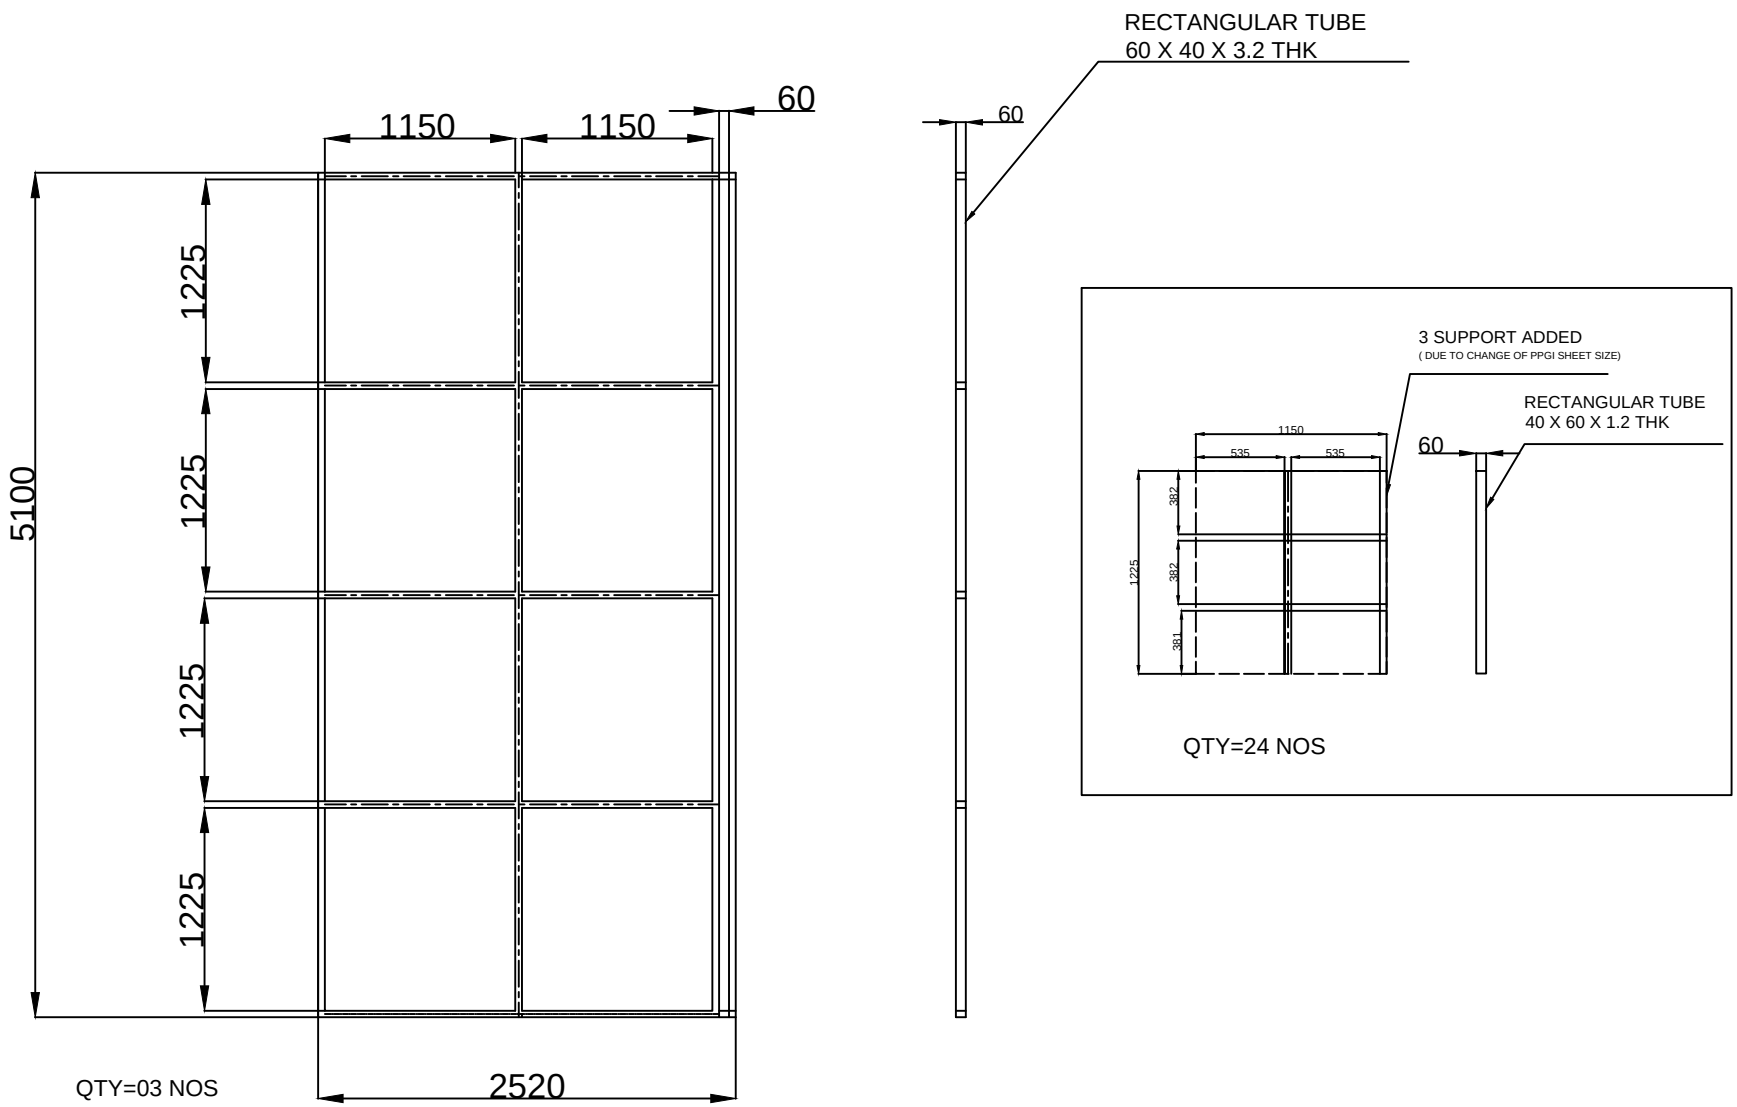

CRM DOOR 11

100 mm added in frame size

	Date	Revised By

This drawing & design is the property of NIHVA TECHNOLOGIES. Not to be sold or copied to any other concern.

TITLE:- 3 LEAF RH
CRM DOOR 11

	NAME	DATE	SIGN
DRAWN	KISHAN	03/05/2022	
CHECK	M.SUTAR	03/05/2022	
APPRD.			

If any queries contact : design@nihva.com

ALL DIMENSION ARE IN mm

NIHVA TECHNOLOGIES PVT. LTD.
NIHVA TECHNOLOGIES PVT. LTD. PUNE
Tel : 020 66304033
Email:- info@nihva.com
Website:- www.nihva.com

CLIENT - LESTECH

LOCATION - POSCO MANGAON

PRODUCT - SLIDING DOOR

DWG NO:-NIHVA/22-23/MFG/0019 | REV- 0

SCALE: NTS | SCALE:-- 1:1 | SHEET: 01 OF 01