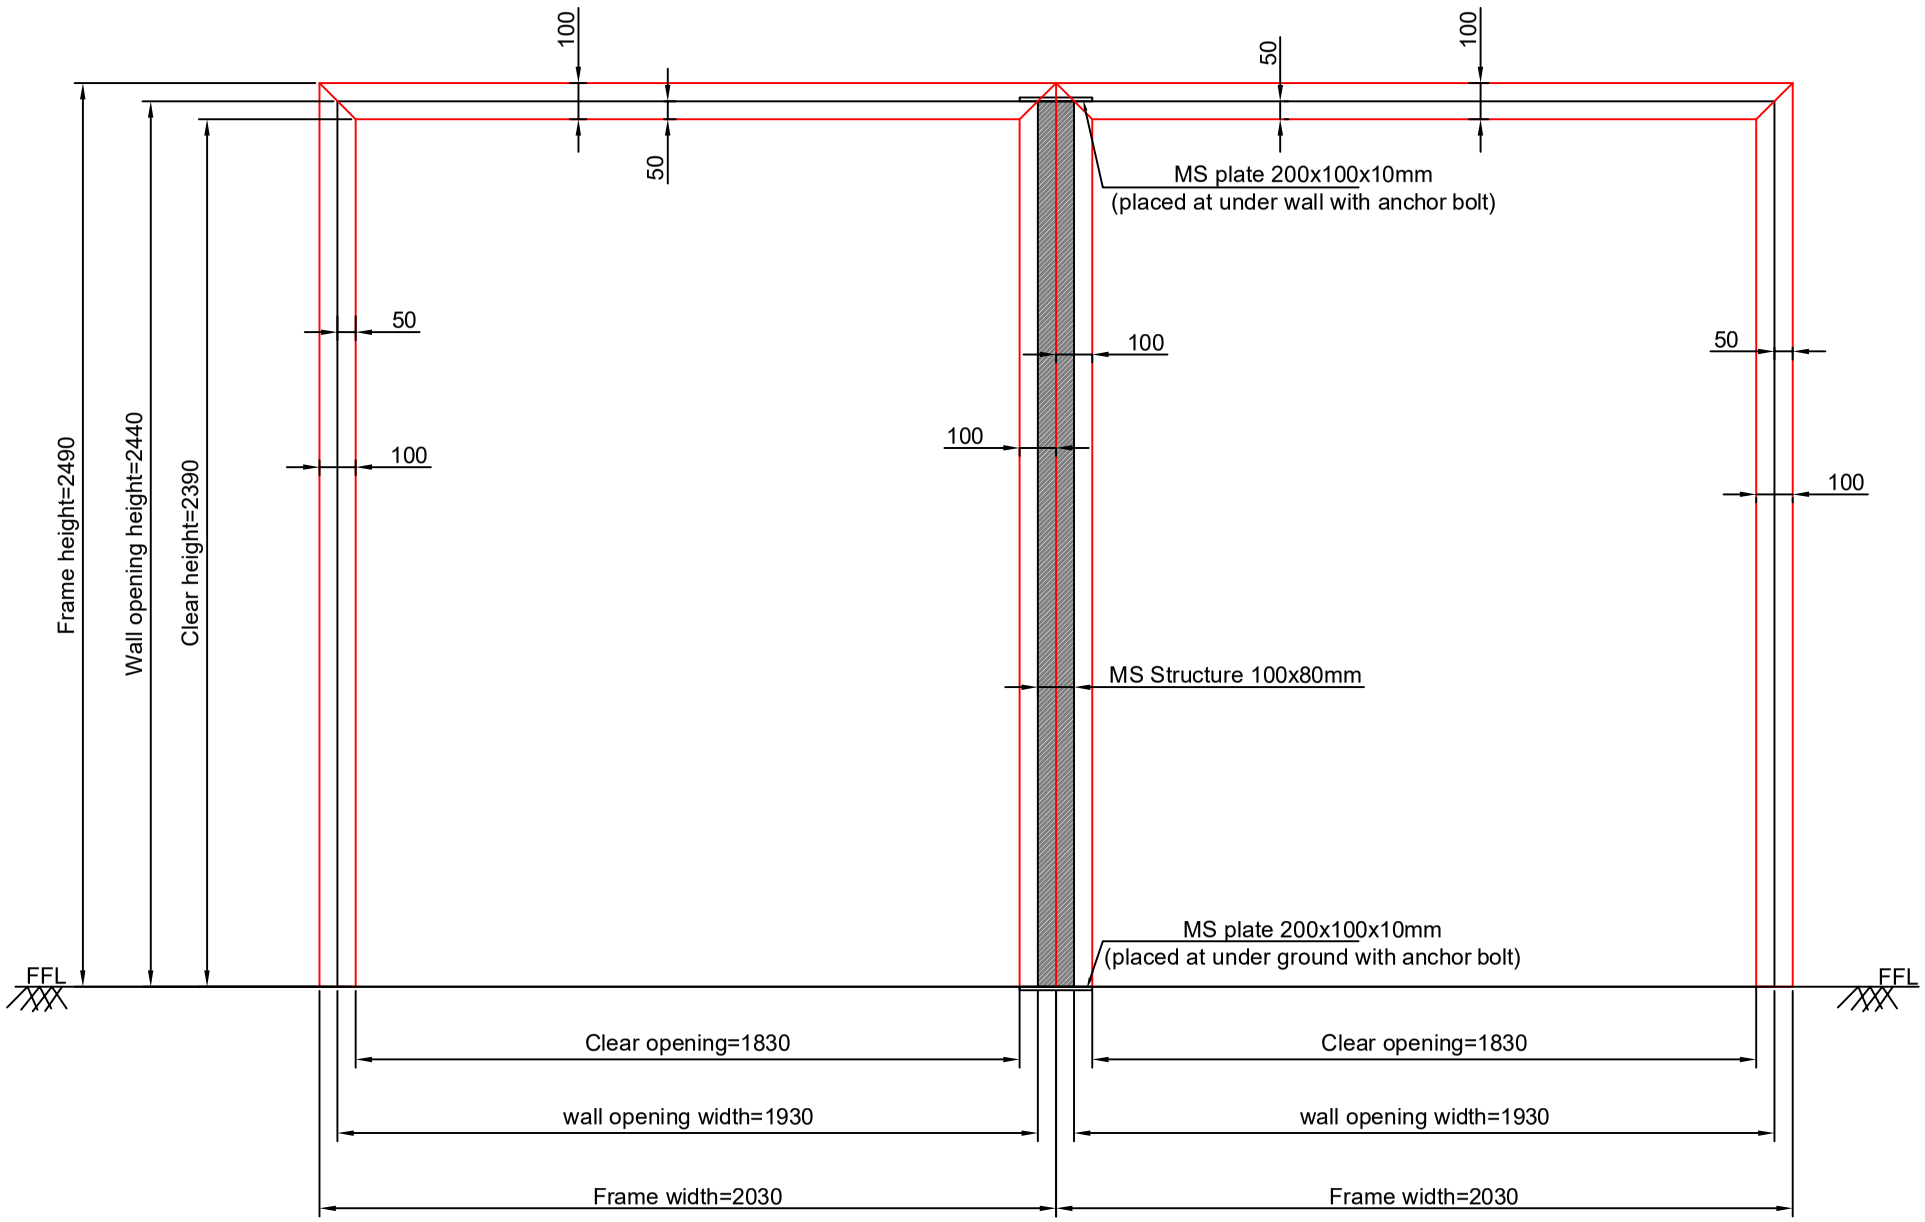



Note:-

1.All dimension are in MM

2.All Civil work and Required structure is in client scope

3.Required100x80mm MS structure

| Rev No. | Revision | Date | Revised By |
|---|---|---|---|
| | | | |

This drawing & design is the property of NIHVA TECHNOLOGIES. Not to be sold or copied to any other concern.

TITLE:- NIHVA Make NFF3 Flip Flap Door Structure

| | NAME | DATE | SIGN |
|---|---|---|---|
| DRAWN | SUJATA | 25-03-2022 | |
| CHECK | G.P | 25-03-2022 | |
| APPRD. | P.J | 25-03-2022 | |

If any queries contact : design@nihva.com

ALL DIMENSION ARE IN mm

NIHVA TECHNOLOGIES PVT. LTD.

NIHVA TECHNOLOGIES PVT. LTD. PUNE
Tel : 020 66304033
Email:- info@nihva.com
Website:- www.nihva.com

CLIENT - RBCC

LOCATION - PUNE

PRODUCT - FLIP FLAP DOOR

DWG NO:-NIHVA/21-22/CLT/0374 | REV- 0

SCALE: NTS | SCALE:-- 1:1 | SHEET: 01 OF 01