




PLAN

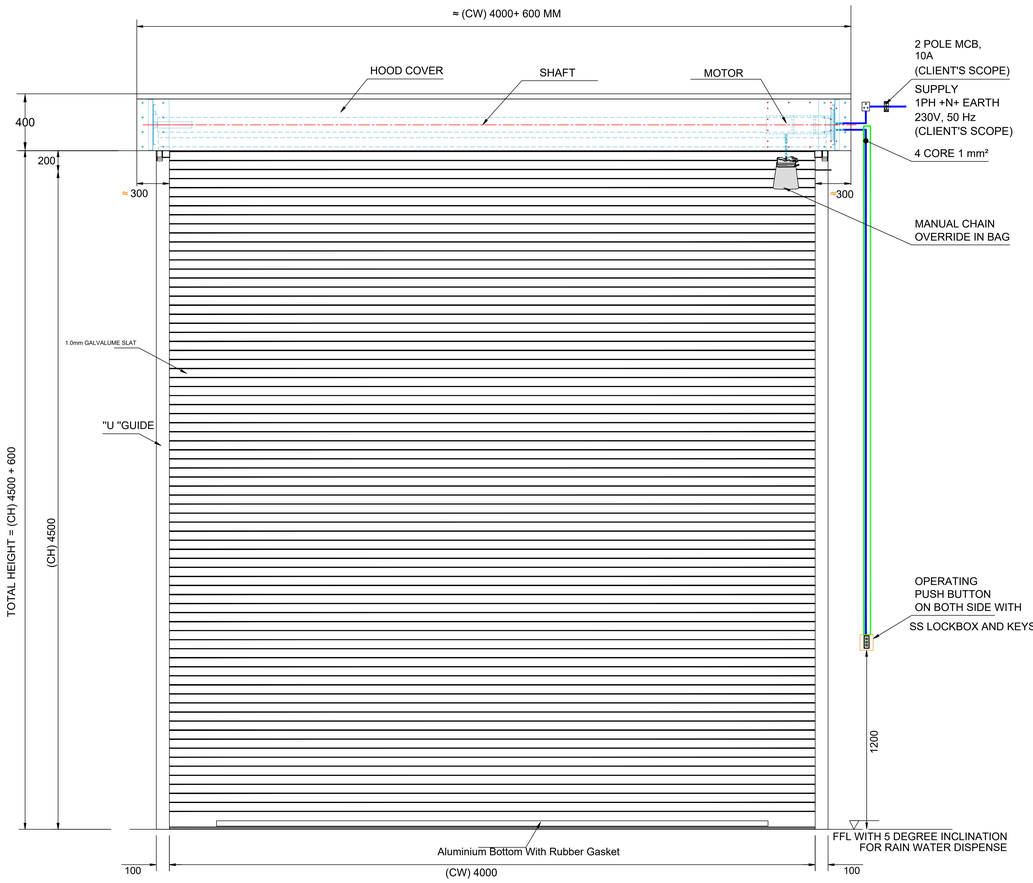

INSIDE ELEVATION

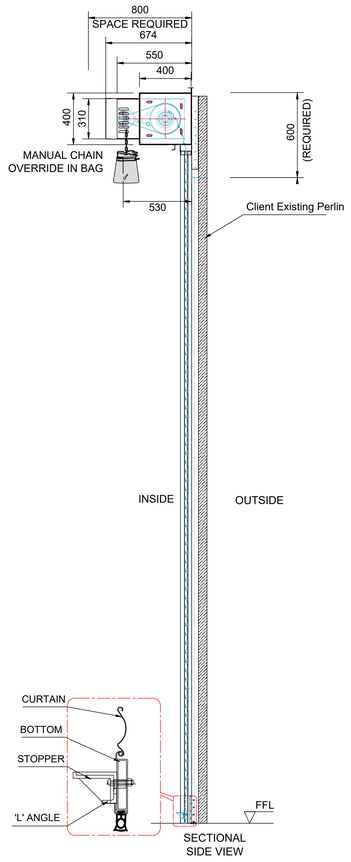

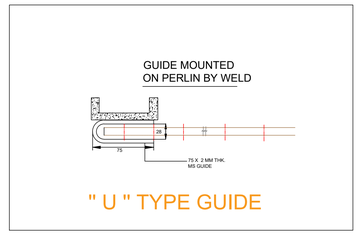

TECHNICAL SPECIFICATION:-

SR.	SPECIFICATION	DETAILS
1.	Description & Drive	Motorised Rolling Shutter (Indirect Drive) with Manual Chain Arrangment
2.	Location Area	Inside
3.	Mounting Surface	Side Brackets: M.S Structure (Client Scope)
4.	Slat	Curved 75 mm Galvalume Slat - 1.0 mm Thk.
5.	Bottom Profile	Aluminium Bottom With Rubber Gasket
6.	Guide Profile	M.S." U " Shape profile 75 x 2 mm Thk.
7.	Hood Cover & Motor Cover	Made of GI Sheet Thickness 0.9 mm
8.	Accessories	Push Button On One SIde

Surafce Finish & Painting Primer & Duco Paint (Matt Finish)

Color Shed-Phirozi 0121 (Light Blue)

Nyloflet seals fitted on shutter skin for friction less movement

Also provide for all materials used in Rolling Shutter during Dispatch

SHUTTER SIZES :-

SR.	CLEAR WIDTH	CLEAR HEIGHT	QTY.
01	4000	4500	01

This drawing & designing is the property of NIHVA TECHNOLOGIES. Not to be sold or copied to any other concern.

TITLE :-
MOTORISED ROLLING SHUTTER

	NAME	DATE	
DRAWN	S.J.	29/02/2024	
CHECK	A.K.	29/02/2024	PROJECT -ROLLING SHUTTER
APPROVAL	V.T.	29/02/2024	FORMAT NO - NIHVA-DD-F-03
			DWG. NO. : NIHVA/23-24/XX — REV-01
			SCALE: NTS — WT: — SHEET: 01 OF 01

ALL DIMENSION ARE IN mm