
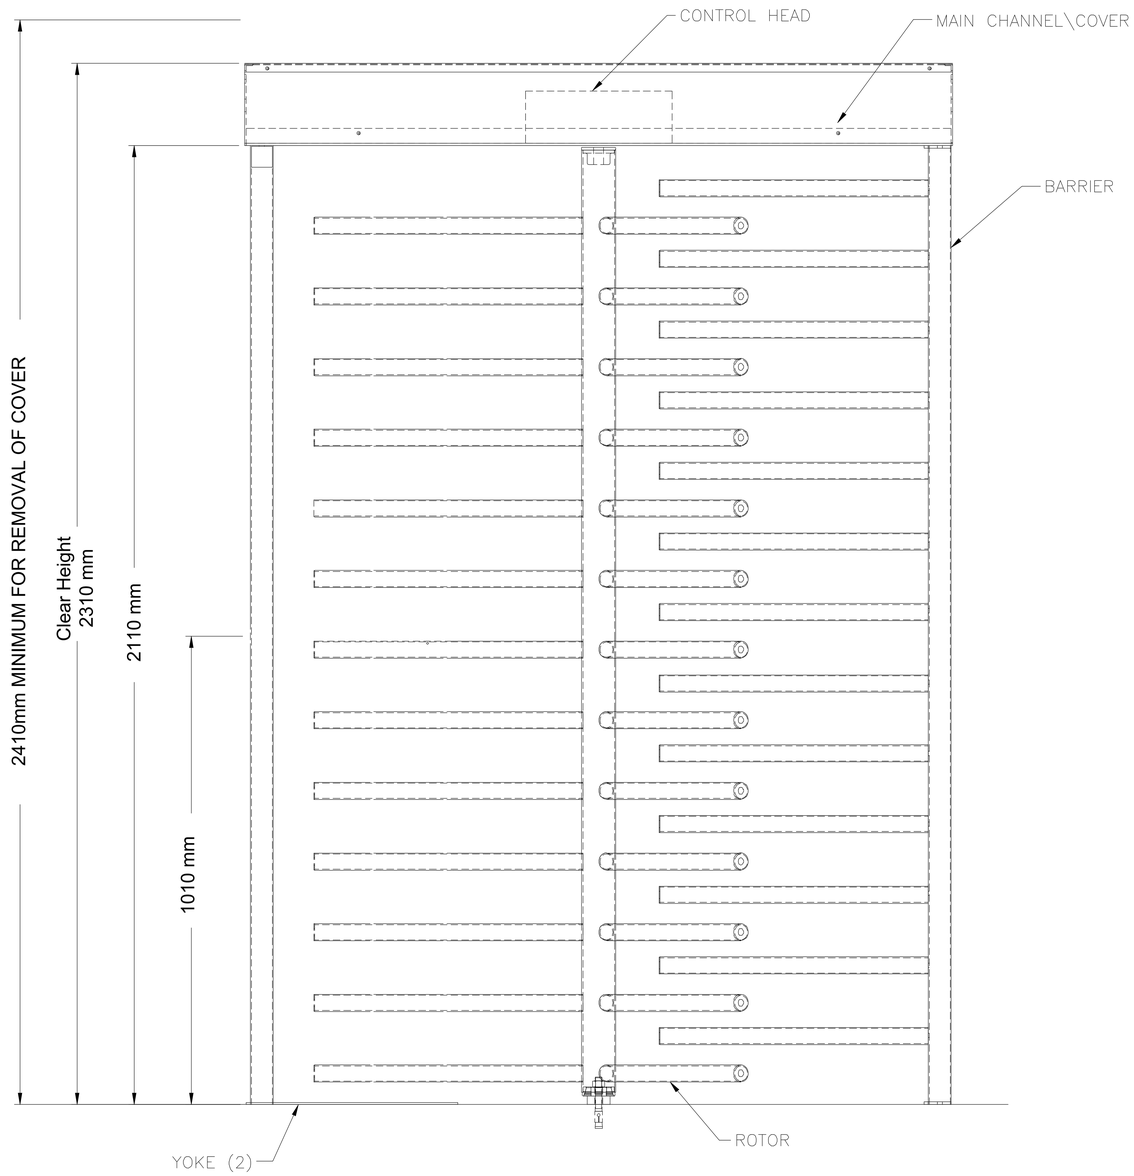


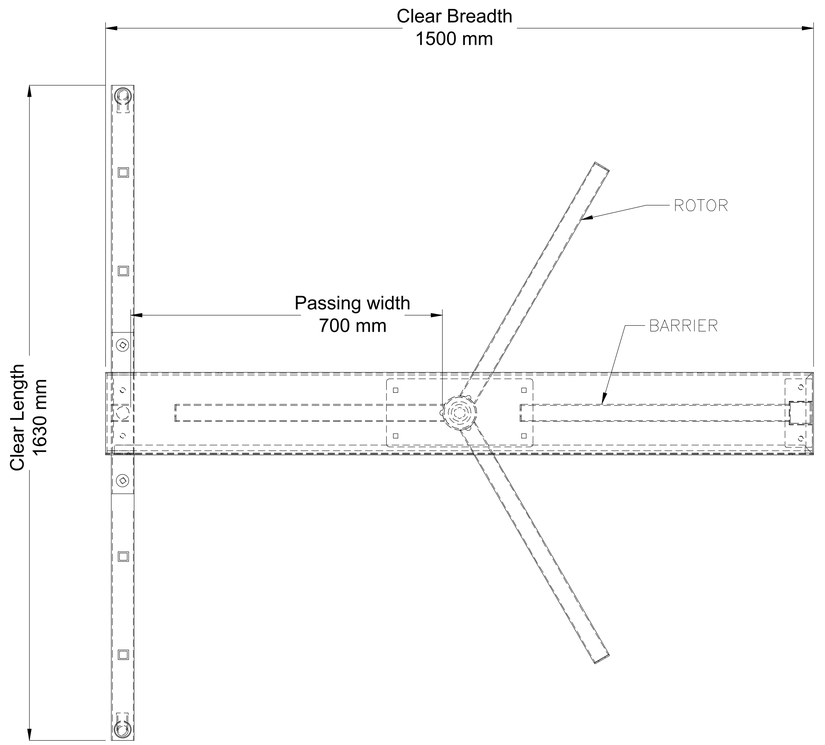

TECHNICAL SPEC :-

Sr.No	Description	Specification
1	Pass rate	35 persons/min
2	Operation	Single / Bi-directional
3	Mechanism	Electro-Mechanical
4	Locking	25° From previous rest position

REV.	Description	Date
1	Safety guard curved to flat	16-08-2024

Sr.No	L	B	H
1	1630	1500	2310

This drawing & design is the property of NIHVA TECHNOLOGIES. Not to be sold or copied to any other concern.

TITLE:- TURNSTILE

	NAME	DATE	SIGN
DRAWN	S.J	24/06/2024	
CHECK	B.B	24/06/2024	
APPRD.	V.T	24/06/2024	

NIHVA TECHNOLOGIES PVT. LTD.
NIHVA TECHNOLOGIES PVT. LTD. PUNE
Tel : 020 66304033
Email:- info@nihva.com
Website:- www.nihva.com

CLIENT - ALFA LAVAL
LOCATION - SATARA
PRODUCT -

If any queries contact : design@nihva.com
DWG NO:-NIHVA/24-25/AL/24060001 REV- 01
ALL DIMENSION ARE IN mm
SCALE: NTS SCALE:-- 1:1 SHEET: 01 OF 01