




DRAWING

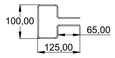

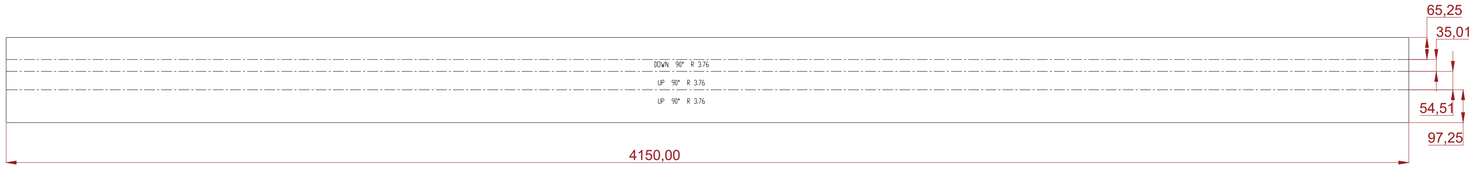

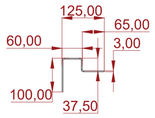

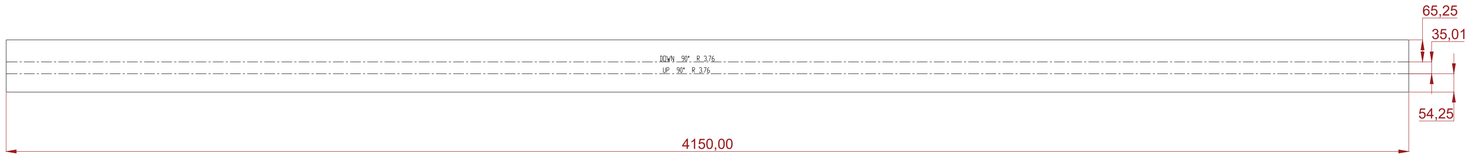

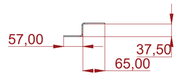

material - ms
Thickness- 3 mm
QTY-12NOS

ARCEDGES _ Shutter Size W3000 x H4000 - 4nos
Name - T shape Guide (100X125x3 mm)
Material - MS
Thk - 3 mm
QTY - 08 NOS

TECHNICAL SPECIFICATION:-

SPECIFICATION	DETAILS
DESCRIPTION & DRIVE	GEAR OPERATED SHUTTER
LOCATION AREA	INSIDE AREA / OUTSIDE AREA
MOUNTING SURFACE	SIDE BRACKETS: ON CONCRETE
SLAT	75 MM WIDE - 1.2 MM THICK GI
BOTTOM PROFILE	M.S. PLATE 100X3.15 MM THICK WITH ANGLE 35X35X5 MM THK
GUIDE PROFILE	M.S."T" SHAPE -100X125X3 MM THK .
HOOD COVER	MADE OF GI SHEET THICKNESS 0.9 MM.
MATERIAL FINISH	SYNTHETIC ENAMEL PAINT

SHUTTER SIZES :- (FOR UTILITY BUILDING)

SR NO	(CW) CLEAR WIDTH	(CH) CLEAR HEIGHT	QUANTITY
1	3000	4000	04 NOS

RIVISION.	DATE
REV 01 : SLAT THICKNESS CHANGE 1MM TO 1.2MM BOTTOM PLATE THICKNESS CHANGE 2.5MM TO 3.15MM ANGLE STIFFENER CHANGE 35X35X3 MM TO 35X35X5 MM	03-12-2025

NOTE-
1. ALL CIVIL WORK WILL BE CLIENT'S SCOPE.
2.IF STRUCTURE REQUIRED FOR SHUTTER IS IN CLIENT'S SCOPE.

NOTE :
GALVANISATION SHALL BE MIN 230 g/SQ.M
HANDLE SHOULD BOTH SIDE

SPECIAL INSTRUCTION'S :

TITLE - DOOR AUTOMATION

DWG NO - NTPL- 300-PM-01

NIHVA TECHNOLOGIES PVT.LTD.PUNE
Website - www.nihva.com

	NAME	SIGNATURE	DATE	PRODUCT - GEAR OPERATED SHUTTER	
DRAWN	V.W.		08-12-2025	PROJECT NO - NTPL- 300	REVISION - 01
CHK'D	B.S.		10-12-2025	SITE LOCATION-GUJARAT	WEIGHT - 31 kg
APPV'D	V.T.		10-12-2025	MATERIAL - MS	QTY - 04 NOS
IF ANY QUERIES CONTACT - Design@nihva.com				PROJECTION METHOD	SCALE :
ALL DIMENSIONS ARE IN 'MM'			A2		SHEET 1 OF 1