



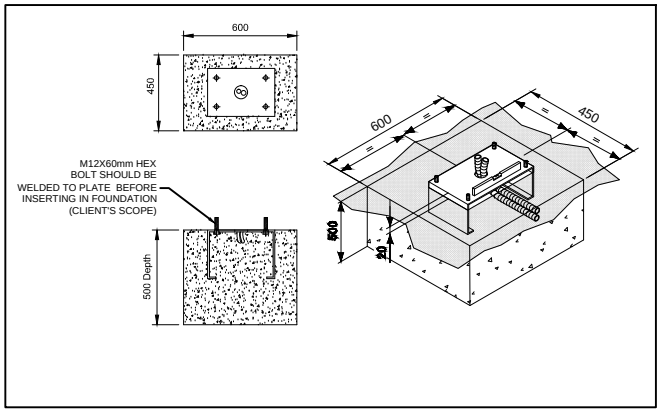

FOUNDATION DETAILS (IN CLIENT'S SCOPE)

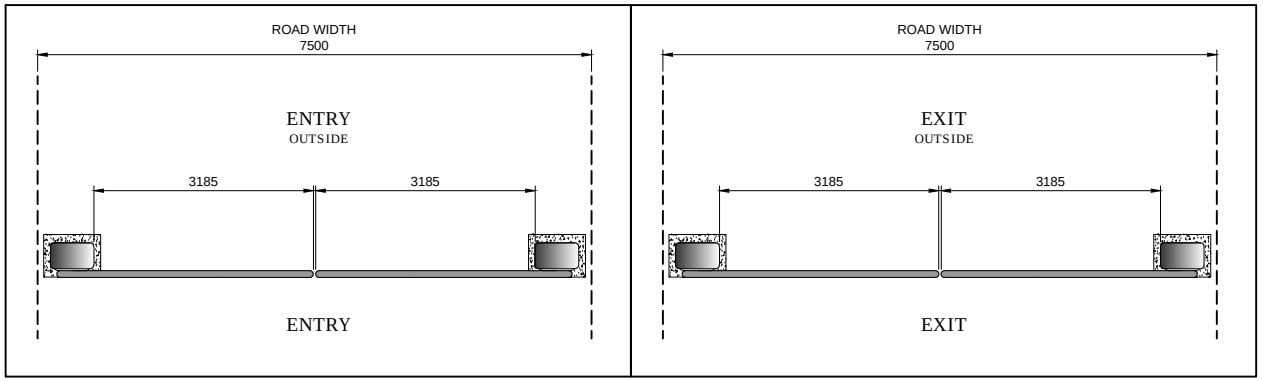

QTY : 4 NOS

REV NO	DATE	DRAWN	REMARK
R02	09.06.20	P.A	1. DIMENSION CHANGE

TOLERANCE - ±10mm

This drawing & design is the property of NIHVA TECHNOLOGIES. Not to be sold or copied to any other concern.

TITLE: BOOM BARRIER

NIHVA TECHNOLOGIES PVT. LTD. PUNE
Tel : 020 66304033
Email:- info@nihva.com
Website:- www.nihva.com

	NAME	SIGN	DATE
DRAWN	P.A		14.04.2020
CHECK	G.J		14.04.2020
APPROVAL			

CLIENT - SERUM BIO-PHARMA PARK
PROJECT -
SITE LOCATION - HADPSAR, PUNE
DWG. NO. : NIHVA/20-21/0003/R01 | REV-R01
If any queries contact : projects@nihva.com | SCALE: NTS | WT: | SHEET: 01 OF 01
ALL DIMENSION ARE IN mm