

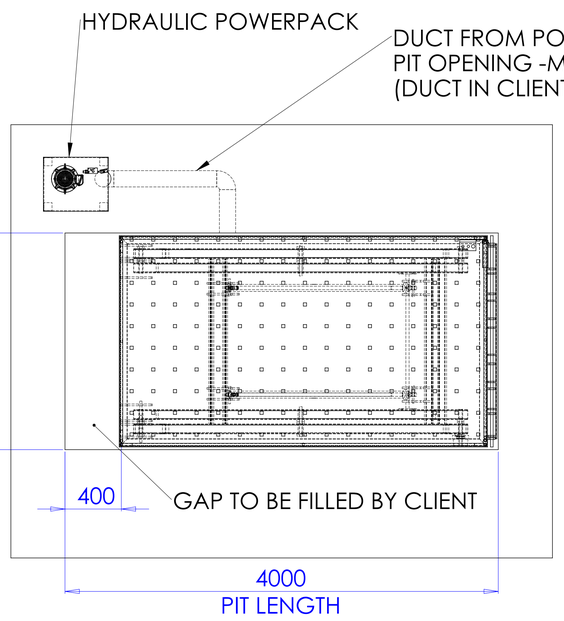



INSTALLATION LAYOUT TOP VIEW

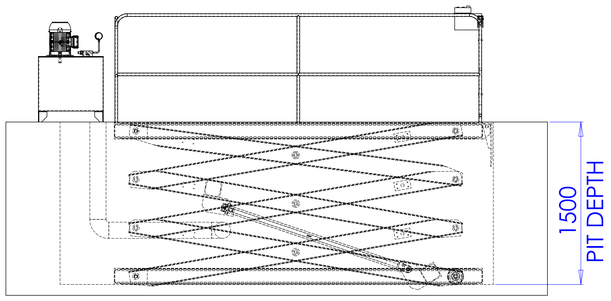



INSTALLATION LAYOUT FRONT VIEW

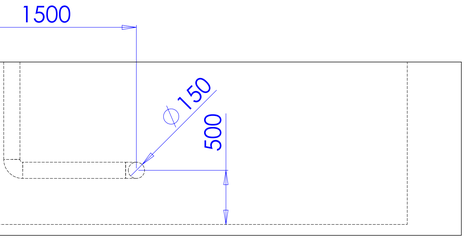


PIT DUCT OPENING

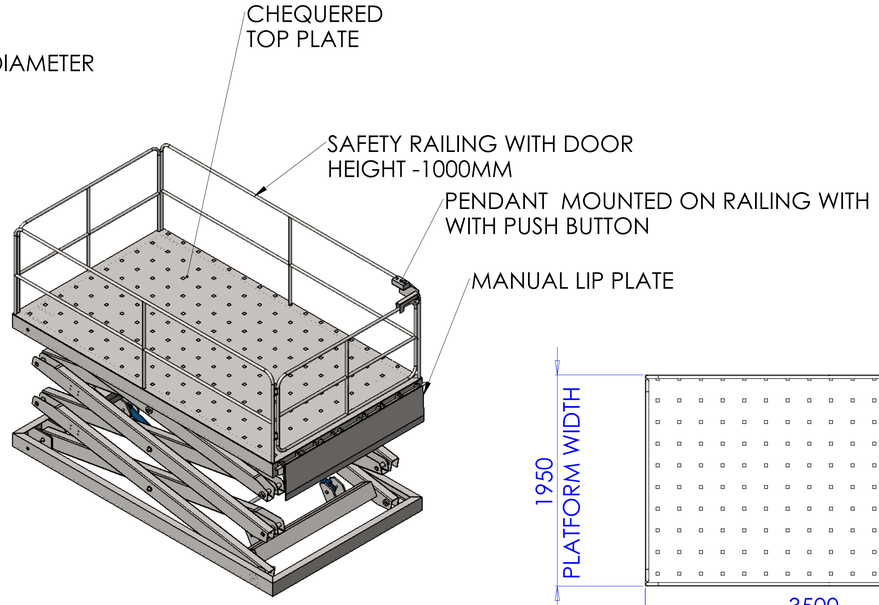

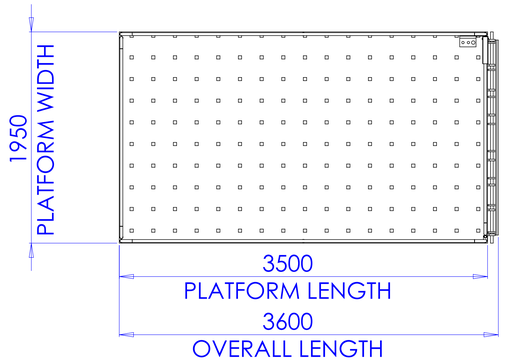

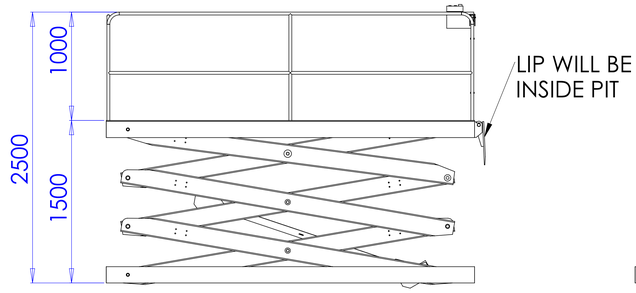

CLOSE HEIGHT-1500 MM.....AS PER SITE CONDITION
POSSIBLE MINIMUM HEIGHT - 1000MM

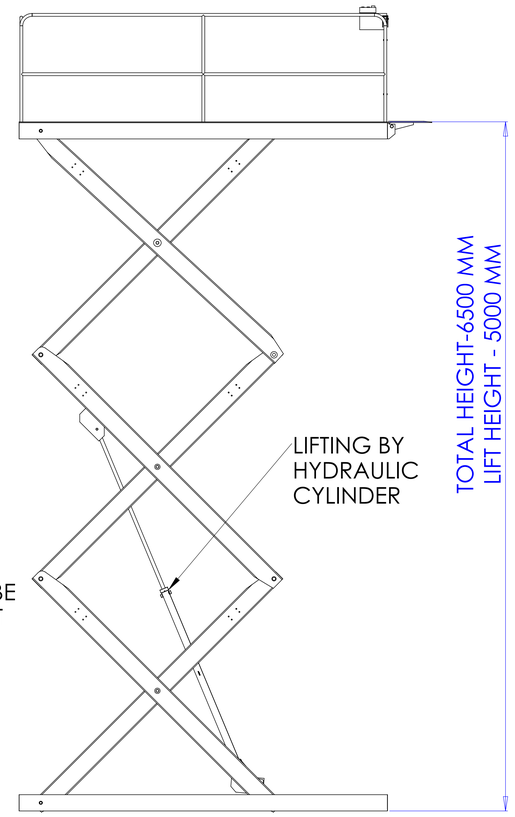

LIFT HEIGHT-5000MM

SPECIFICATIONS OF PIT MOUNTED SCISSOR LIFT -

- PLATFORM SIZE-3500mm(L)X1950mm(W)
- PIT SIZE - 4000mm(L)x2000mm(W)x1500mm(H).....AS PER SITE VISIT
- CLOSE HEIGHT -1500 MM
- MINIMUM POSSIBLE CLOSE HEIGHT - 1000 MM
- TOTAL HEIGHT FROM PIT BOTTOM - 6500 MM
- LIFT HEIGHT EXCLUDING CLOSE HEIGHT -5000 MM
- LIFTING BY HYDRAULIC CYLINDERS 2 NOS
- HYDRAULIC POWERPACK - 3 PHASE AC , 440V
- MOTOR CAPACITY - 3 PHASE AC , 3 HP
- SAFETY RAILING WITH DOOR, RAILING HEIGHT - 1000 MM
- PENDANT MOUNTED ON RAILING WITH EMERGENCY STOP BUTTON
- MAXIMUM HEIGHT & LOWER HEIGHT CUTOFF LIMIT SWITCH
- LIMIT SWITCH INTERLOCK WITH SCISSOR LIFT DOOR & BUILDING DOOR
- ELECTRICAL CONTROL PANEL PROVIDED WITH LENGTH 5 METER CABLE STANDARD
- POWERPACK TO BE POSITIONED NEAR TO SCISSOR LIFT & PROVIDED WITH HOSES OF 2.5 METER LENGTH FROM PIT OPENING
- MANUAL LIP PLATE 1 NO WITH LOCKING ARRANGEMENT , LENGTH -400 MM
- SCISSR LIFT FIXING BY ANCHOR WEDGE BOLT
- PROVIDED MAINTENANCE STOPPER FOR SAFETY DURING SERVICE & MAINTENANCE
- PAINT- GOLDEN YELLOW (RAL 1004) AS NIHVA STANDARD , IF OTHER PLEASE INFORM .

UNLESS OTHERWISE SPECIFIED: DIMENSIONS ARE IN MILLIMETERS SURFACE FINISH: TOLERANCES: LINEAR: ANGULAR:

NIHVA We Make Possible

DEBURR AND BREAK SHARP EDGES

DO NOT SCALE DRAWING | REVISION

CLIENT- TENNECO CLEAR AIR PRODUCTS PVT LTD

	NAME	SIGNATURE	DATE
DRAWN	SIDDHESHWAR		16.6.2021
CHK'D			
APPV'D			
MFG			
Q.A			

MATERIAL:

WEIGHT:

TITLE: SCISSOR LIFT 1.5 TON, LH-5METER

DWG NO: NIHVA/21-22/025/SL A0

SCALE:1:20 SHEET 1 OF 1