

PROPOSED PLAN LAYOUT

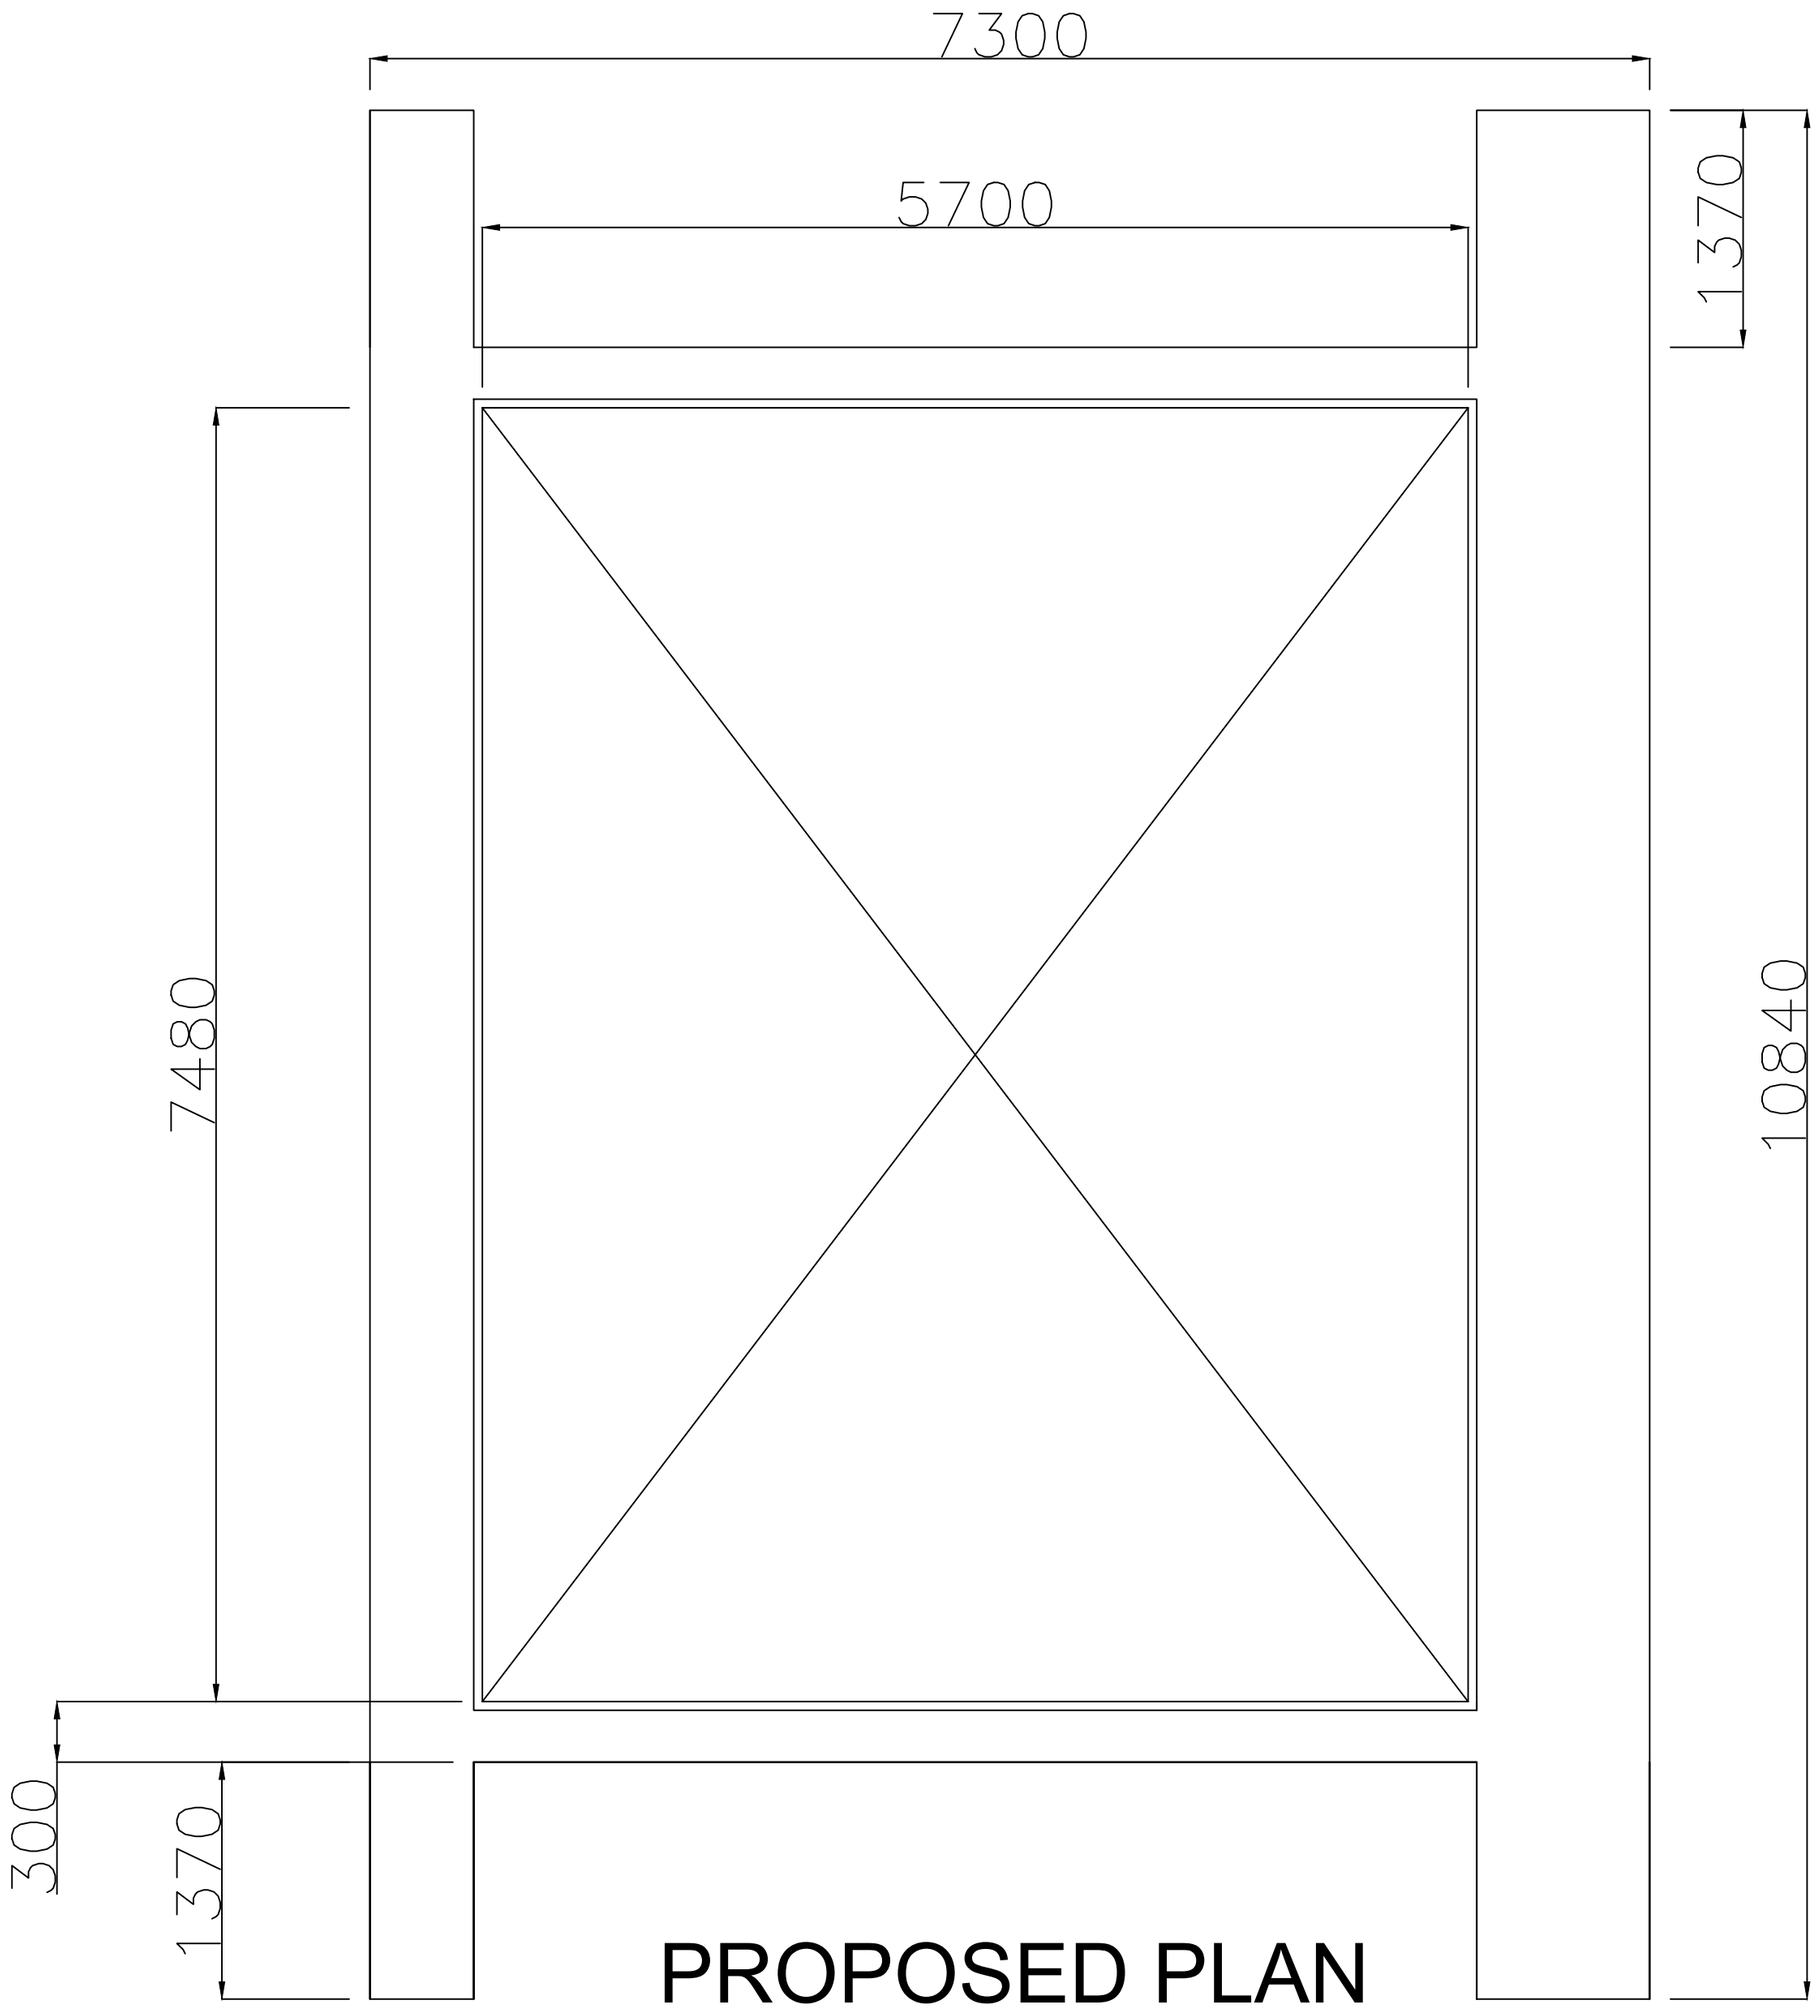

PROPOSED PLAN

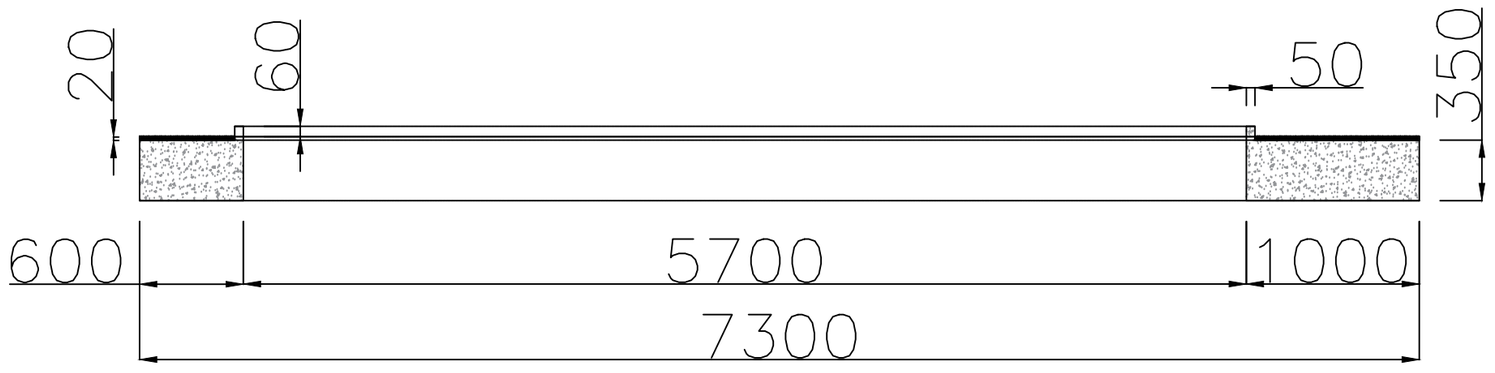

SECTION VIEW

1. THE STRUCTURE AROUND THE CUT OUT SHOULD BE OF CONCRETE FOR FOR PROPER FASTENING OF ROOF.
2. TOP SURFACE SHOULD BE OF GRANITE 20MM FOR SMOOTH FUNCTIONING OF ROOF.
3. ROOF EXTENSION IS SHOWN FOR ONLY REFERENCE. IT CAN BE MODIFIED AS PER THE WORK UNDERTAKEN.
4. GRADIENT OF 50MM NEED TO BE PROVIDED ALONG THE OUTER LENGTH TO AVOID WATER STAGNANCY IN GUIDE RAIL.
5. AL PROFILE - POWDER COATED 60X63 MM
6. GASKET - EPDM
7. MOTOR - ITALIAN/GERMAN MAKE
8. ALL DIMENSION IN MM.
9. ALL CIVIL WORK IS IN CLIENT SCOPE.

This drawing & design is the property of NIHVA TECHNOLOGIES. Not to be sold or copied to any other concern.

TITLE: ROOF MOVEMENT LAYOUT			NIHVA TECHNOLOGIES PVT. LTD.
	NAME	SIGN	DATE
DRAWN	RAMESHWAR		26.11.22
CHECK	MAHESH .S		28.11.22
APPRD.	V.T.		28.11.22
CLIENT - MR. ABDULLAH			
LOCATION - KERALA			
PRODUCT - GROUND MOUNTED RETRACTABLE ROOF			
If any queries contact : projectsautomation@nihva.com			NIHVA\22-23 / REV- 0
ALL DIMENSION ARE IN mm			SCALE: NTS / SHEET: 01 OF 01