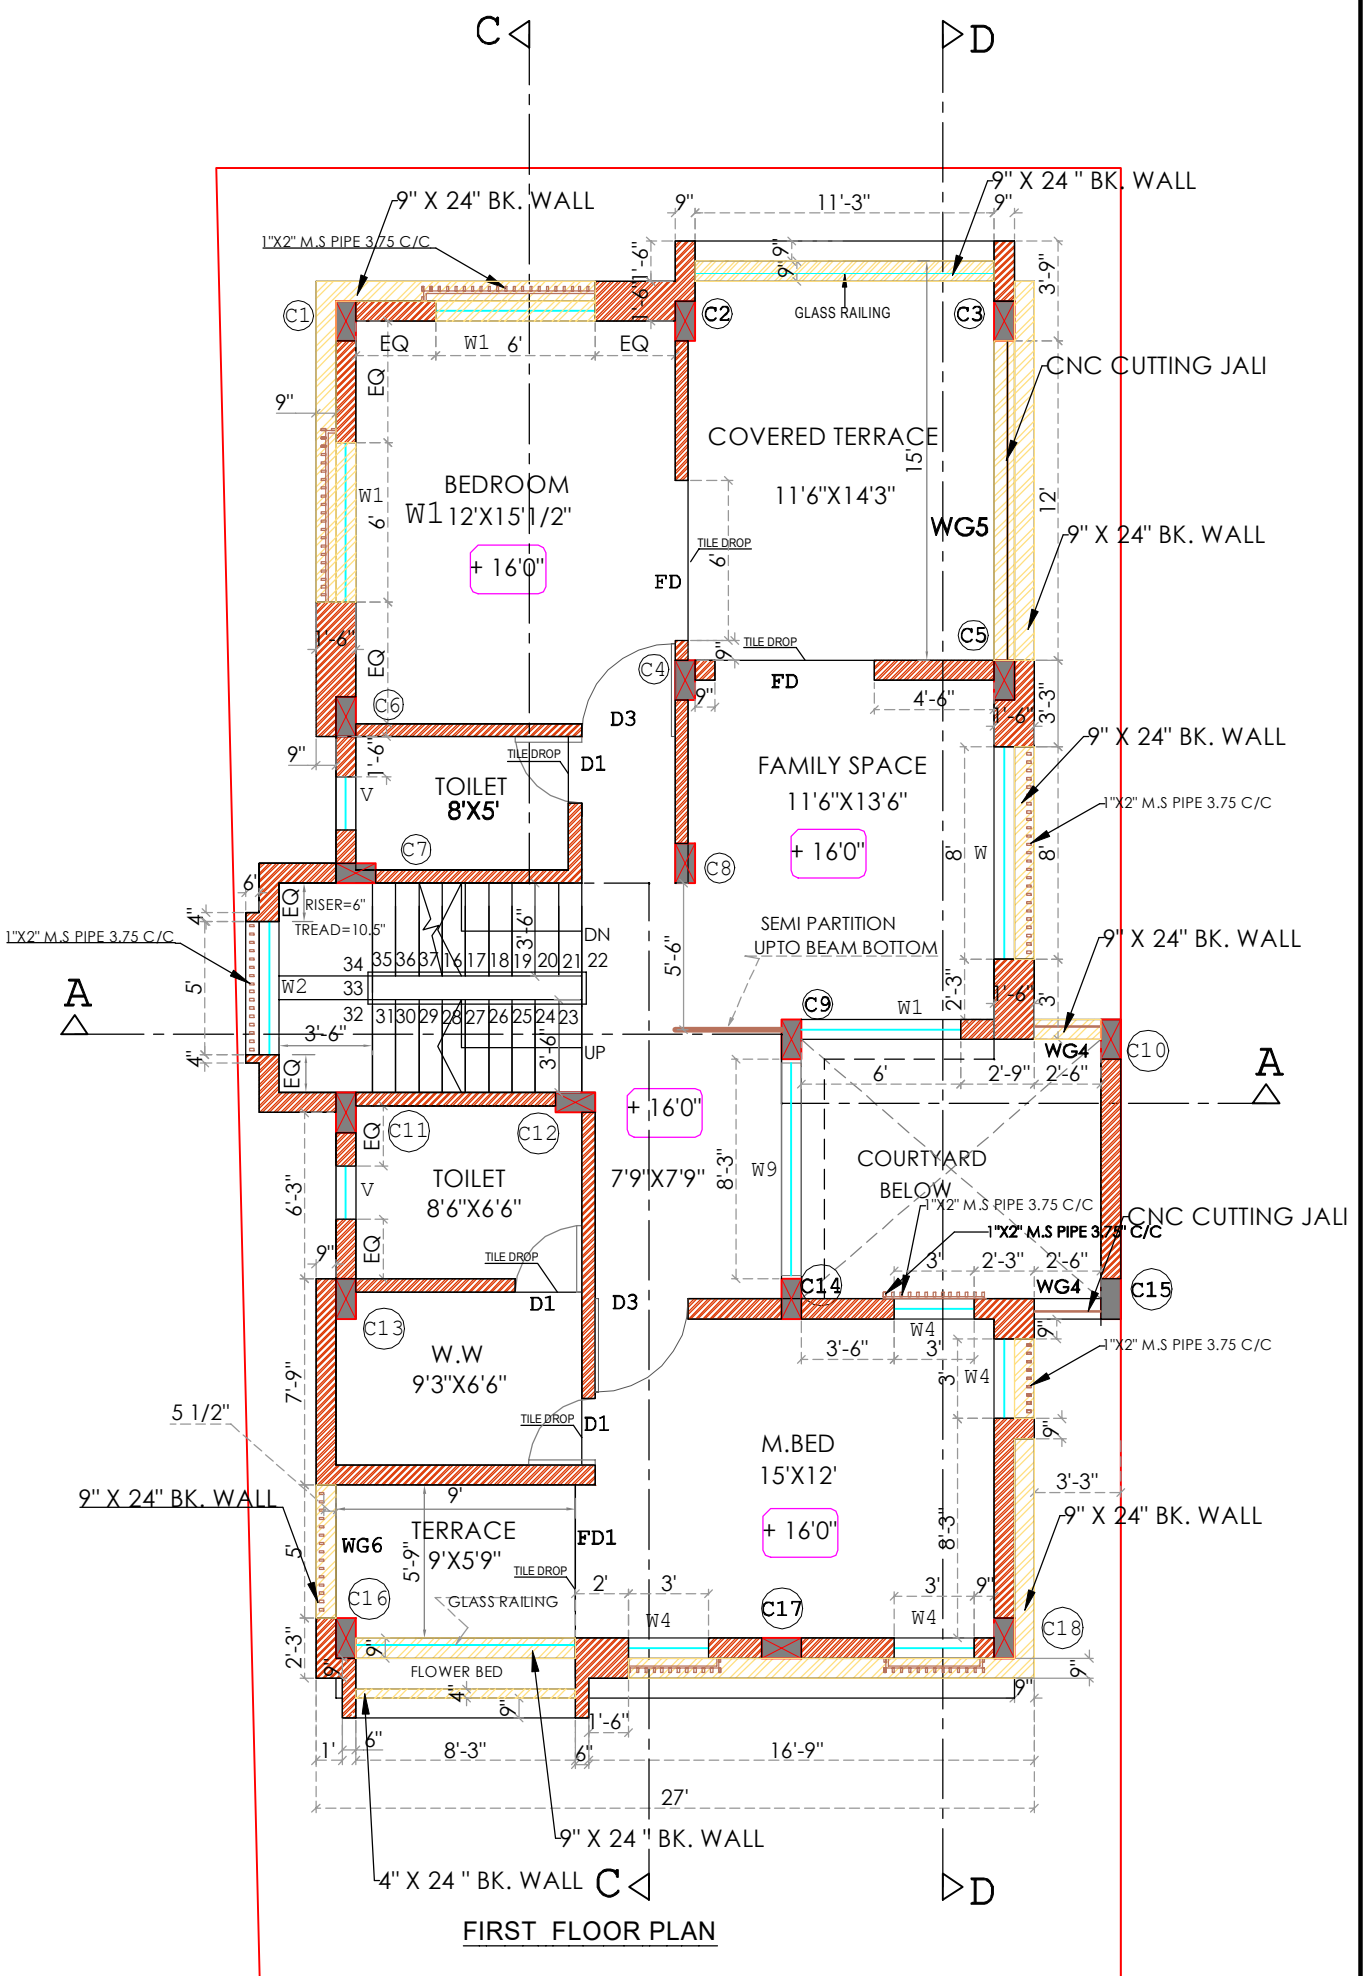


FIRST FLOOR PLAN

BRICK WORK DRAWING FOR FIRST FLOOR

WORKING DWG. NO. - 3

PROPOSED BUNGALOW AT-MAYANI, DIST.-SATARA

FOR DR. DESHMUKH

NORTH

SCALE:

DATE- 02-03-2023

M V ASSOCIATES

ARCHITECTS, CIVIL ENGINEERS & CONSULTANTS

13,GAJANAN NAGAR,GORAKHPUR,PIRWADI, SATARA - 415003.

CELL: +91-9422039823,9822039823

E-mail : mvassociatessatara@gmail.com