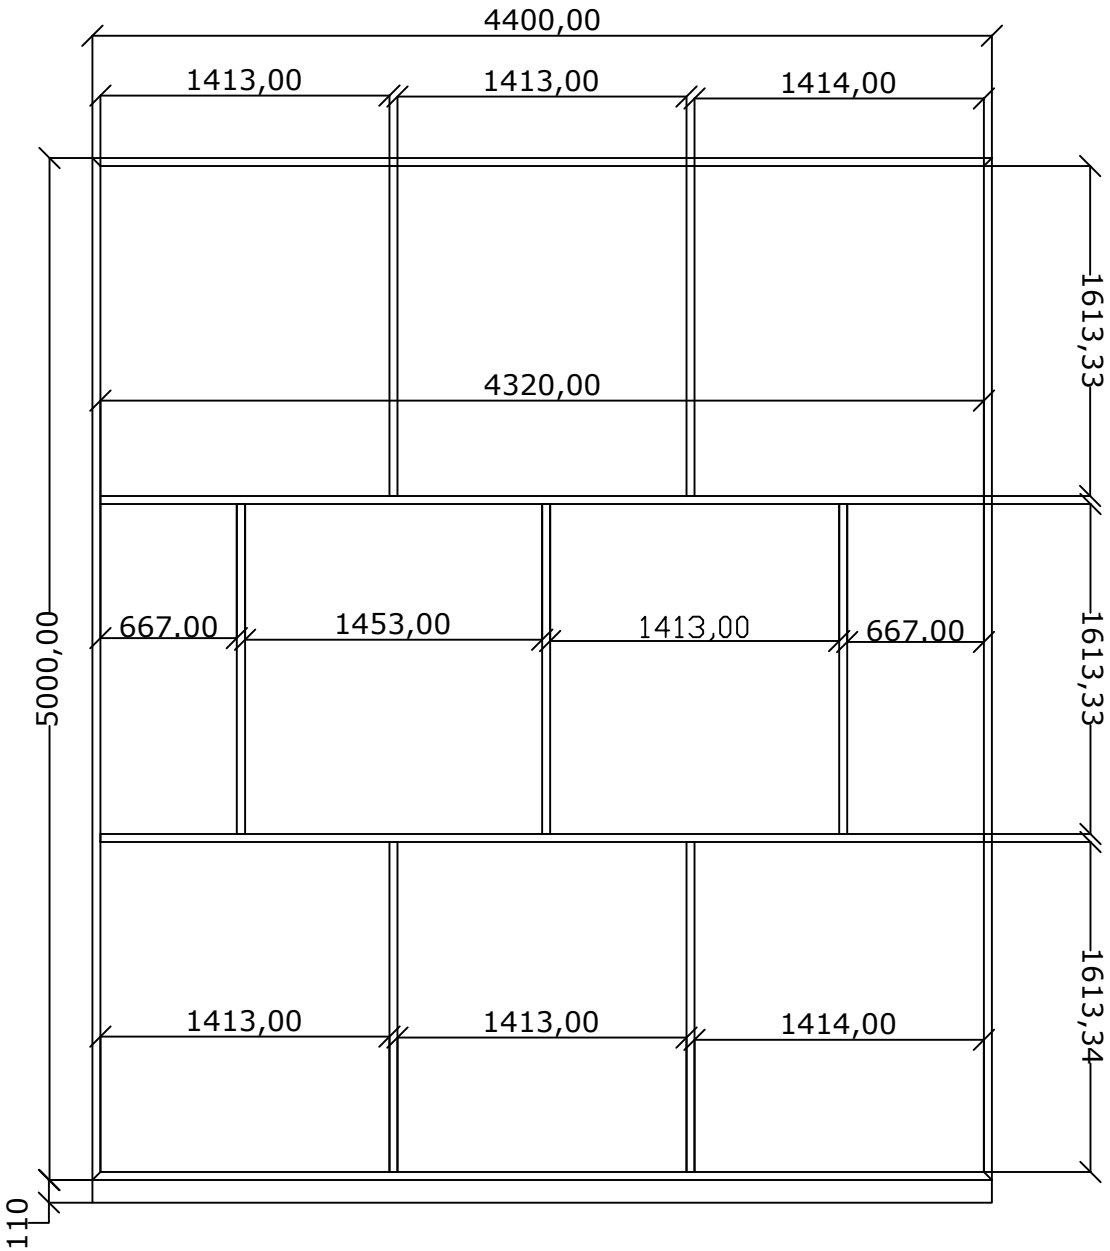


SR.NO	DESCRIPTION	LENGTH IN mm	QTY.
1.	MS REQ. TUBE (40X80X3mm)	4400	02
2.	MS REQ. TUBE (40X80X3mm)	5000	02
3.	MS REQ. TUBE (40X80X3mm)	4320	02
4.	MS REQ. TUBE (40X80X2mm)	1614	07
5.	FLAT SLAT	1614	245
6.	CLADDING SHEET (150X4400X1.6mm)	–	01
7.	BOTTOM WHEEL (Ø100)	–	02
8.	HANDLE	–	01
9.	TOWER BOLT	–	01

SR.NO	DESCRIPTION	SIZE	LOCTION	QTY.
01	LEAF NO - 03	4400mm X 5000mm	W2:W3	02
02	LEAF NO - 04	4400mm X 5000mm	W3:W4	02
03	LEAF NO - 05	4400mm X 5000mm	W4:W5	02
04	LEAF NO - 07	4400mm X 5000mm	W6:W7	02
05	LEAF NO - 08	4400mm X 5000mm	W7:W8	02

Note :-

1. All Dimension are in mm
2. This drawing is only for understanding purpose

This drawing & designing is the property of NIHVA TECHNOLOGIES. Not to be sold or copied to any other concern.

TITLE :- SLIDING LEAF

NIHVA TECHNOLOGIES PVT. LTD. PUNE
Tel : 020 66304033
Email:- info@nihva.com
Website:- www.nihva.com

	NAME	DATE
DRAWN	S.J.	05/12/2024
CHECK & APPROVAL	V.T.	05/12/2024

CLIENT - PANCHSHIL
PROJECT - MANUAL SLIDING SCREEN
FORMAT NO - NIHVA-DD-F-03
DWG. NO. : NIHVA/24-25/00XX | REV-01
SCALE: NTS | WT: | SHEET: 01 OF 01
ALL DIMENSION ARE IN mm
If any queries contact : design@nihva.com