




MODEL : SKB-A7
SHUTTER SLAT
THICKNESS 1.0mm

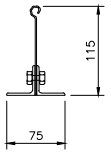

MODEL : SKB-T120
FIRE RATED BOTTOM BAR

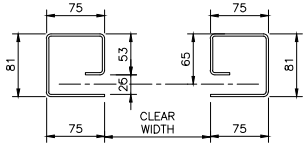


MODEL : SKB-G65
THICKNESS 3mm
GALVANISED STEEL GUIDE RAIL

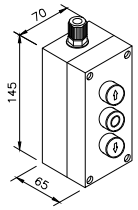


PUSH BUTTON

SHUTTER TYPE	SKB 2 HOURS FIRE RATED ROLLER SHUTTER (BS 476)
SHUTTER SLATS	SKB-A7 SLATS SINGLE SKIN, 1.0MM THICK
SLATS FINISHING	POWDER COATED TO SKB STANDARD RAL 9010 WHITE COLOR
GUIDE RAIL	GALVANIZED STEEL SKB-G65
GUIDE RAIL FINISHING	POWDER COATED TO SKB STANDARD RAL 9010 WHITE COLOR
BOTTOM BAR	SKB-T120 GALVANIZED STEEL WITH L-ANGLE BOTTOM BAR
BOTTOM BAR FINISHING	POWDER COATED TO SKB STANDARD RAL 9010 WHITE COLOR
BOX DESIGN	MILD STEEL SECTION FRAME DESIGN
BOX & CASING COVER	0.8MM GALVANIZED STEEL
FINISHING OF COVER	POWDER COATED TO SKB STANDARD RAL 9010 WHITE COLOR
OPERATION	SKB 500KG MOTORISED WITH MANUAL OVERRIDE CHAIN
MOTOR POWER SOURCE	230 VOLTS, 1 PHASE, 50 Hz.
FIRE MODE	TFL-THERMAL FUSSIBLE LINK WILL AUTO CLOSE BY GRAVITY FORCE
	WHEN ROOM TEMPERATURE RISES UP TO 71 C
	CONTROL BOX (SKB-MFSCB-230V)
	FIRE SIGNAL 24VDC 400mA ARE REQUIRED BY CONTRACTOR
ADDITIONAL ITEM	-


SHUTTER NO.	LOCATION	CLEAR WIDTH	CLEAR HEIGHT	MOTOR POSITION	QTY
FRS-03	-	4900mm	4000 mm	RIGHT	1

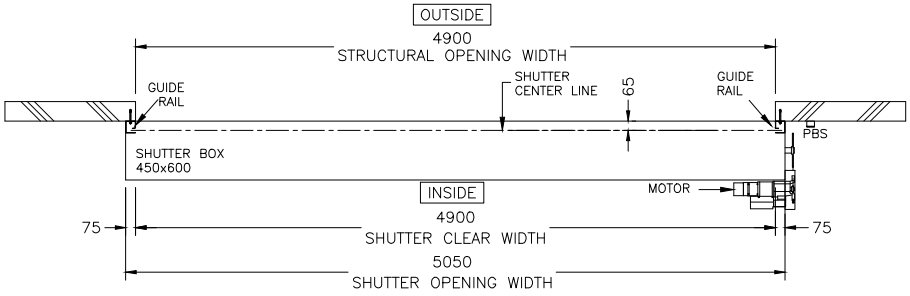


PLAN VIEW

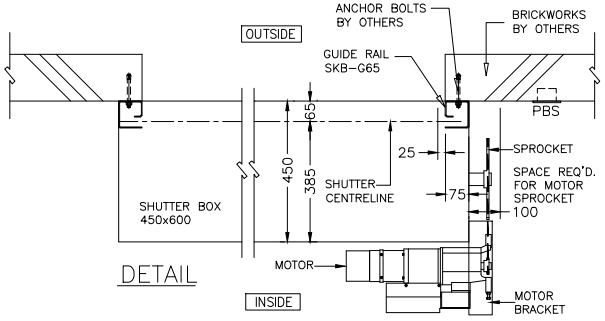


DETAIL

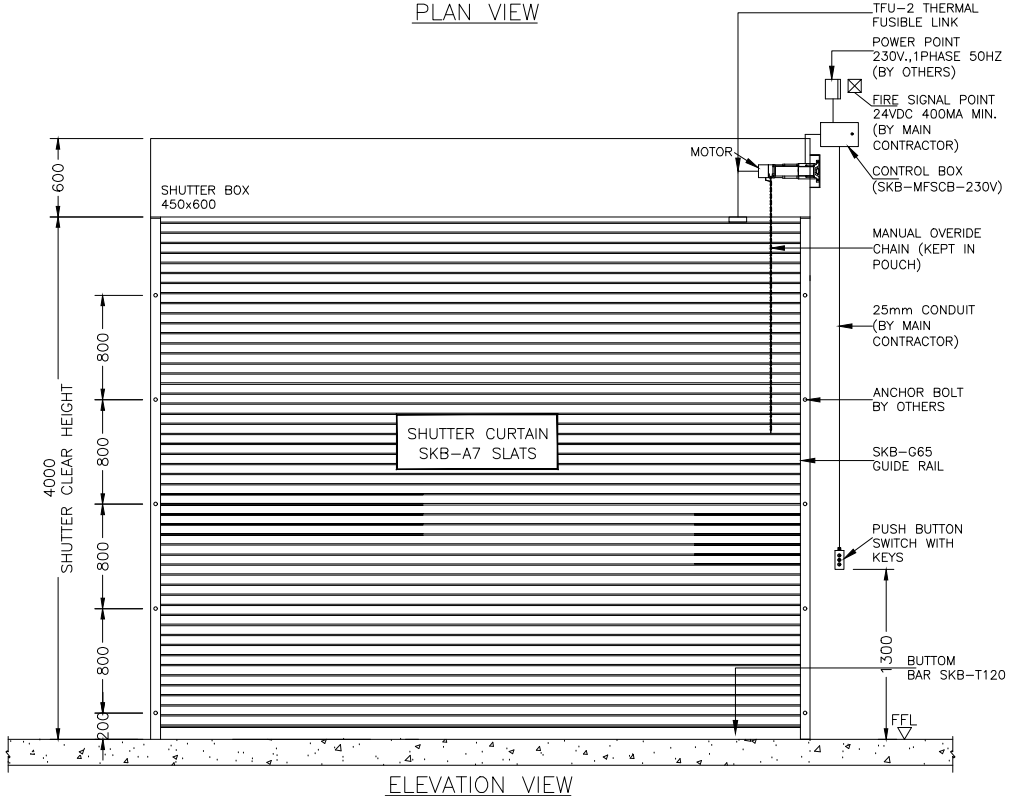

ELEVATION VIEW

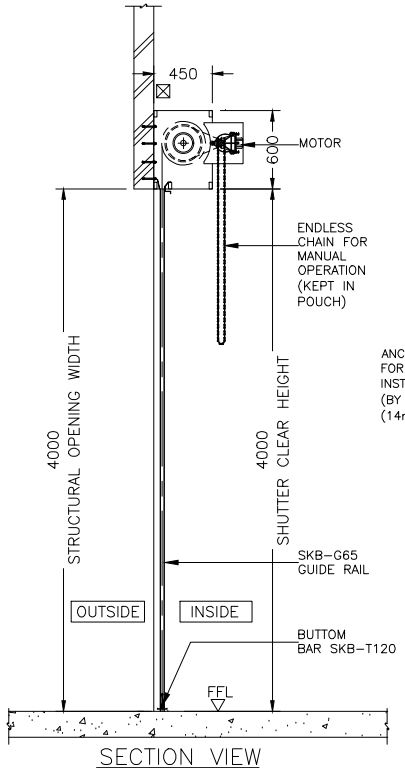

SECTION VIEW

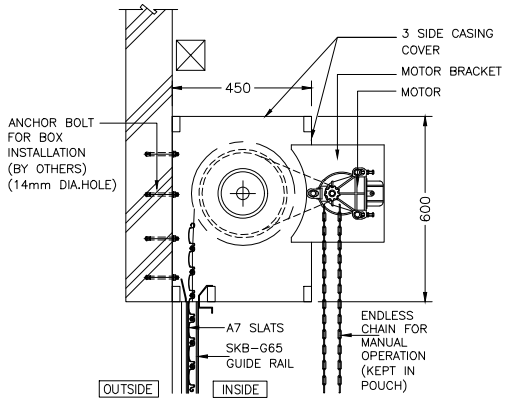

BOX DETAIL

SHOP DRAWING

NO.	DATE:	AMENDMENTS:
V01	19/1/21	CHANGE COLOR RAL & AMEND STRUCTURAL OPENING

DEVELOPER / LANDOWNER:

REV.

ARCHITECTURAL:

CONSULTANT :

MAIN CONTRACTOR :

INSTALLER :

MANUFACTURER:

SKB STORAGE INDUSTRIES SDN.BHD
Lot 22 Jalan Teknologi, Taman Sains
Selangor,Kota Damansara
47810 Petaling Jaya,Selangor Darul Ehsan
Tel:(60) 3 6157 2277 Fax:(60) 3 6157 2211

PROJECT TITLE:

BMW PROJECT

DRAWING TITLE:

SKB 2HRS FIRE RATED A7 SINGLE SKIN ROLLER SHUTTER

DRAWN :ZUL	CHECKED : TM	DRAWING NO. :	REV :
SCALE :N.T.S	DATE :19/01/2021	SKB/NIHATECH/ 2021/01/003	01