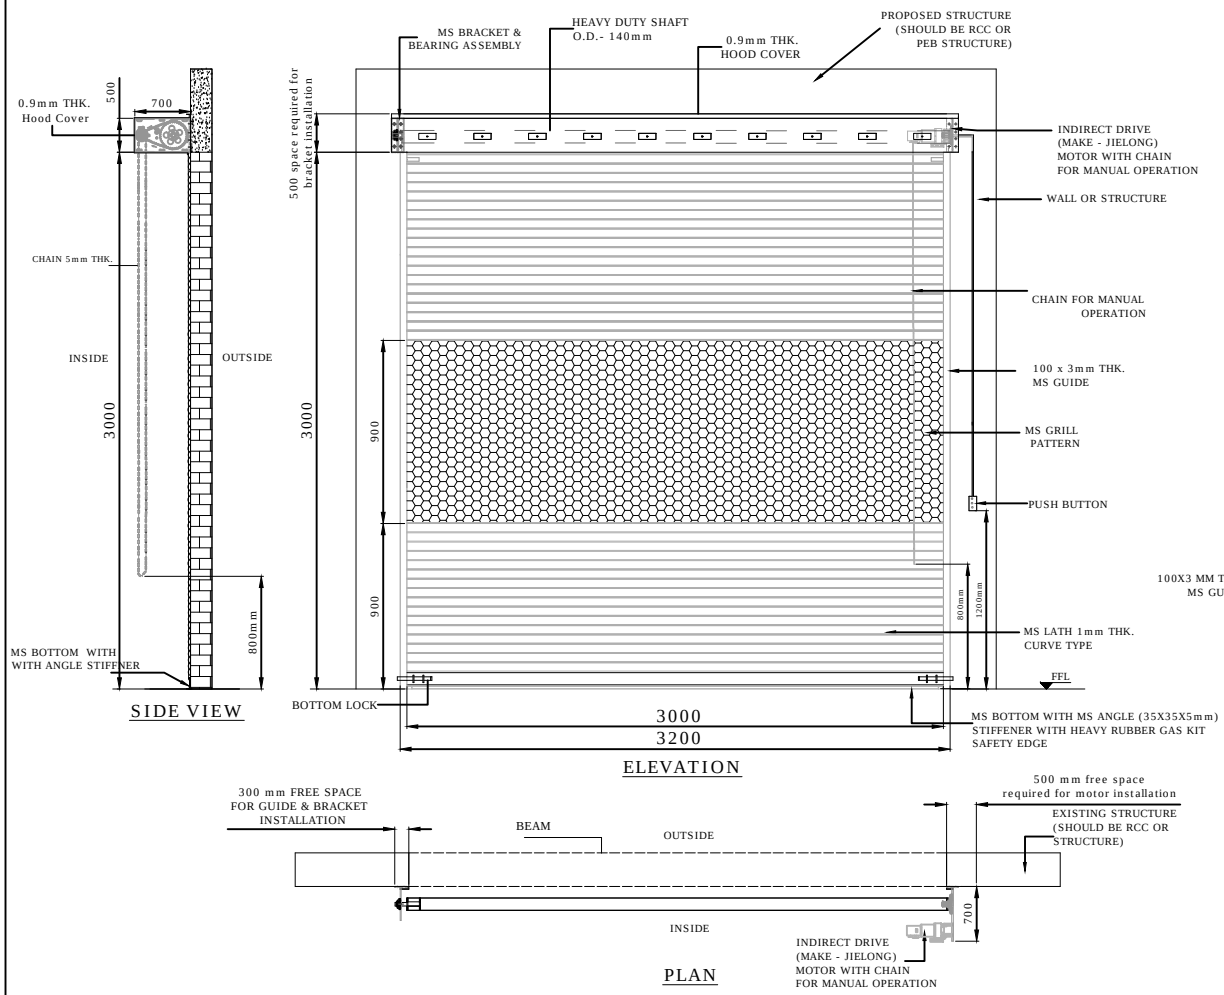


SHUTTER SPEED- APPROX. 0.05m/s

SHUTTER TYPE	CLEAR WIDTH (CW)	CLEAR HEIGHT (CH)	GUIDE SIZE	BRACKET SIZE	SHAFT SIZE (O.D)	QUANTITY	LOCATION
RS1	3000	3000	100X3mm	375X375X5mm	140mm	8	G.F. UTILITY BUILDINGS

R02 - DETAILS ADD IN DRAWING .
R01 - GRILL SIZE CHANGED.

DIMENSION :

CLEAR WIDTH	CLEAR HEIGHT	QUANTITY
3000	3000	08 NOS

NOTE:
1.REQUIRED STRUCTURE FOR ROLLING SHUTTER WILL BE CLIENT'S SCOPE.
2.SINGLE PHASE. 3 CORE 1.5 SQ. CABLE REQUIRE AT SITE(CLIENT'S SCOPE)
3. SHUTTER WILL BE POWDER COATED CLIENT SHOULD CONFIRM RAL COLOR SHADE.
4.POWER SUPPLY LOCATION WILL BE ACTUAL SITE CONDITION.

REV NO	DATE	DESCRIPTION
REV 0	21-11-17	INITIAL DRAWING
REV 1	29-11-17	MORE DETAILS ADDED TO THE DRAWING.
REV 2	13-12-17	MORE DETAILS ADDED TO THE DRAWING.

NIHVA TECHNOLOGIES PVT. LTD.
NIHVA TECHNOLOGIES PVT. LTD. PUNE
Email:- info@nihva.com
Website:- www.nihva.com

TITLE:

MOTORIZED ROLLING SHUTTER 3X3m

CLIENT'S APPROVAL :

CLIENT - SCON PROJECTS

PROJECT - ENZENE BIOSCIENCES LTD.

SITE LOCATION - CHAKAN.

DWG. NO. : NIHVA/17-18/0283 | REV.:-02

SCALE: NTS | WT: | SHEET:1 OF 1

		DATE	SIGN.
DRAWN	SURAJ	13-12-2017	
CHECK	OMKAR	13-12-2017	
APPRD	SHEKHAR	13-12-2017	

If any queries contact : design@nihva.com

NOTE: ALL DIMENSIONS ARE IN mm

THIS DRAWING & DESIGN IS THE PROPERTY OF NIHVA TECHNOLOGIES. NOT TO BE SOLD OR COPIED TO ANY OTHER CONCERN.