




SECTION 'X'-'X'

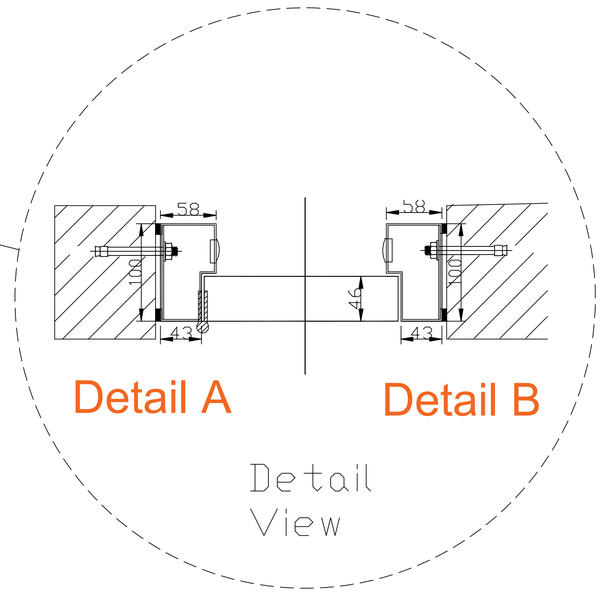

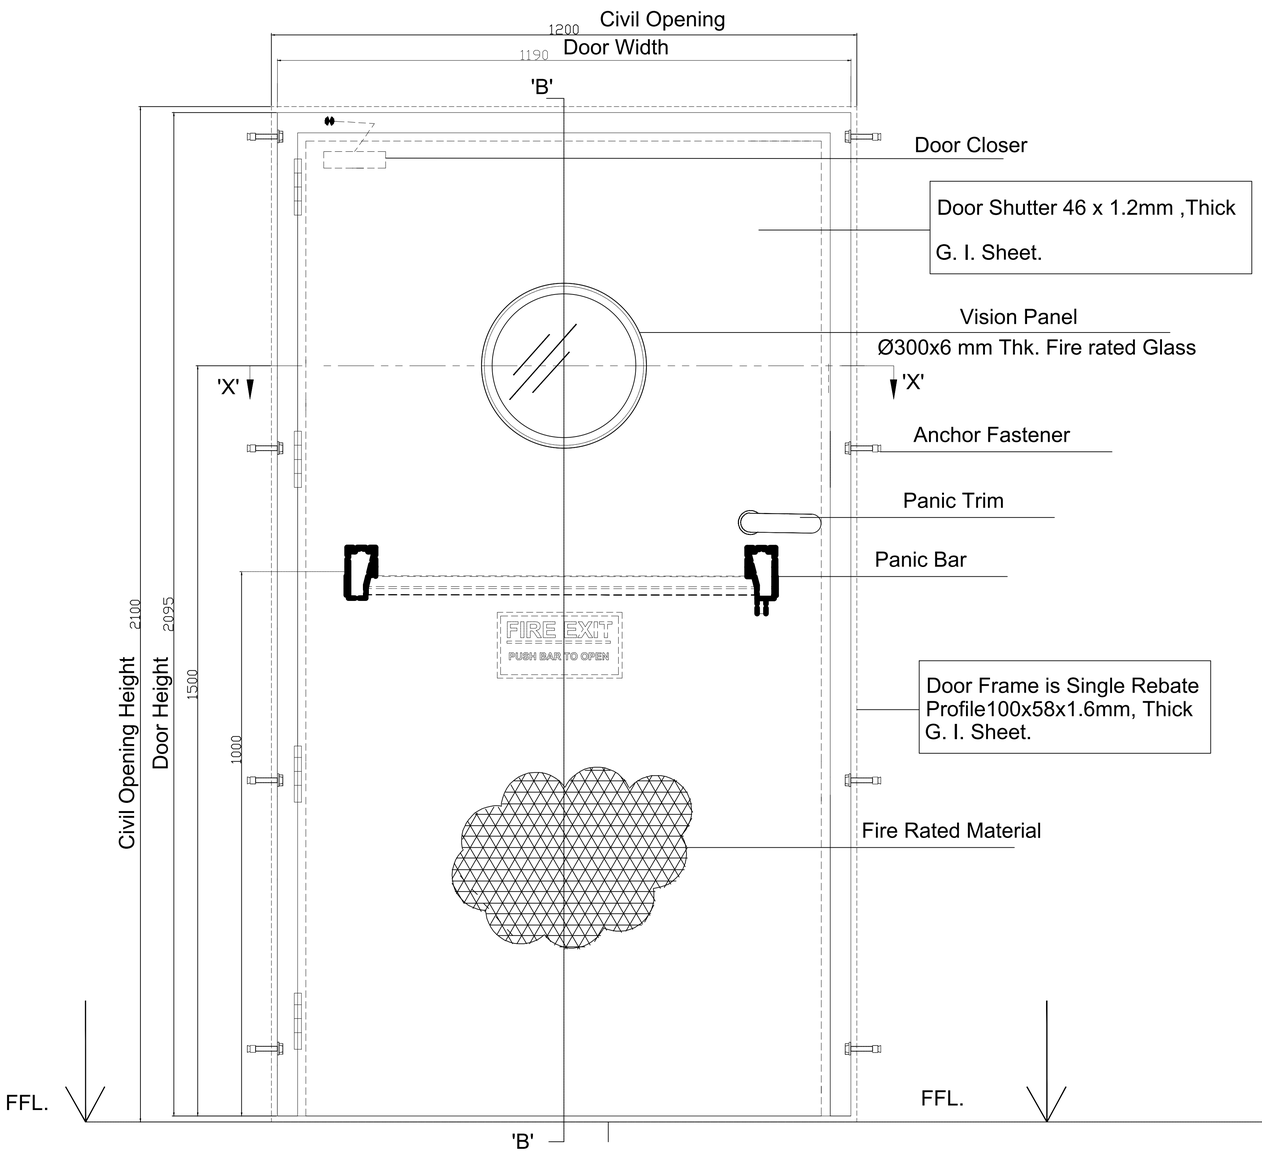

ELEVATION

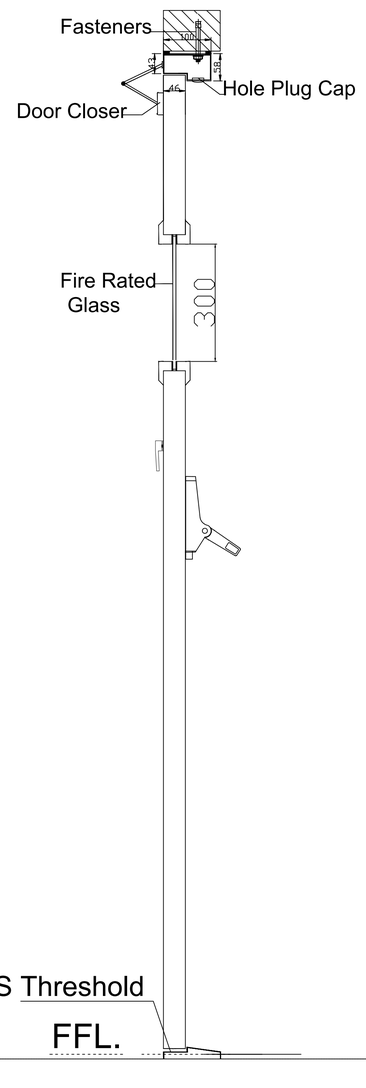

SECTION B-B

TECHNICAL SPECIFICATION :

Sr.	Technical Specification.
01	Door frame - 100X58 mm x1.6mm thick G.I. Sheet
02	Door Shutter - 46 mm x1.2mm thick G.I. Sheet
03	SS Ball Bearing Hinges 4"x3"x3mm
04	Single Leaf Panic Bar (1 Point)
05	External Panic Trim
06	Anchor Fasteners (M10x100mm Dia)
07	Heavy Duty Door Closer (TS 1000)
08	S.S. "D" type handle
09	Vision Window Ø 300 With fire Rated Glass
10	Fire Rating - 120 Minutes
11	Surface Finish - As per Client Requirement

SIZE:

Sr.	Clear Width	Clear Height	Qty
01	1200	2100	14

This Drawing & Design is the property of NIHVA TECHNOLOGIES. Not to be sold or copied to any other concern.

TITLE :- FIRE DOOR

NIHVA TECHNOLOGIES PVT. LTD.

NIHVA TECHNOLOGIES PVT. LTD. PUNE
Tel : 020 66304033
Email:- info@nihva.com
Website:- www.nihva.com

NAME	DATE	SIGN	
S.J	03/01/2024		CLIENT - Smith Structures India Pvt. Ltd.
A.K	03/01/2024		LOCATION - PUNE
V.T	03/01/2024		PRODUCT - FIRE DOOR / QTY-14 No's
If any queries contact : design1@nihva.com			DWG NO - NIHVA/23-24/CLT/062 / REV- 0
MENSION ARE IN mm			SCALE : NTS / SHEET : 01 OF 01