




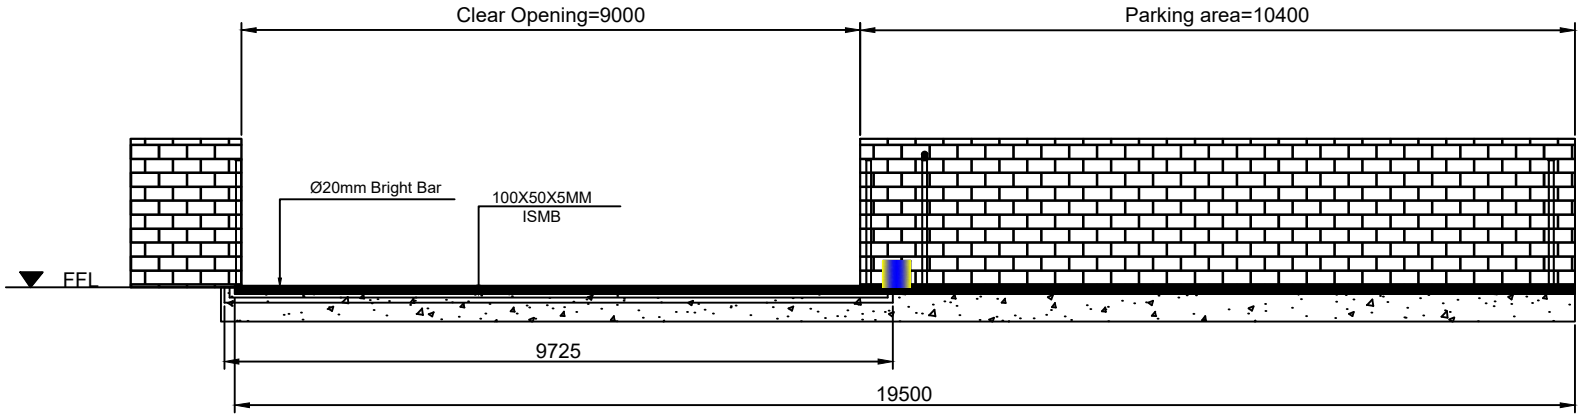


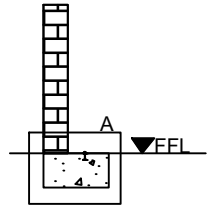

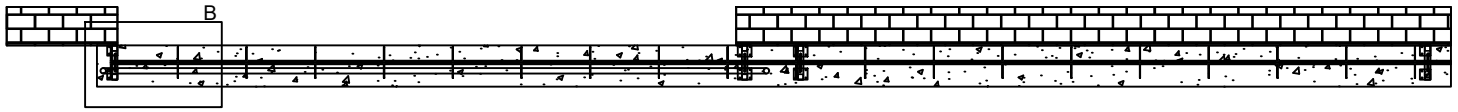

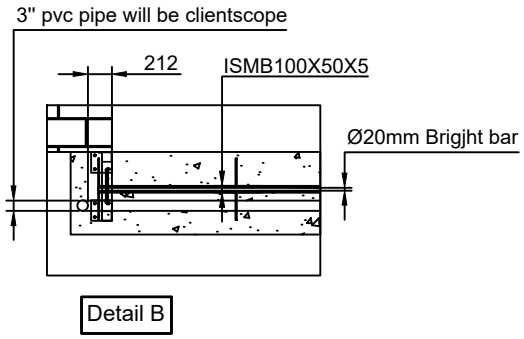

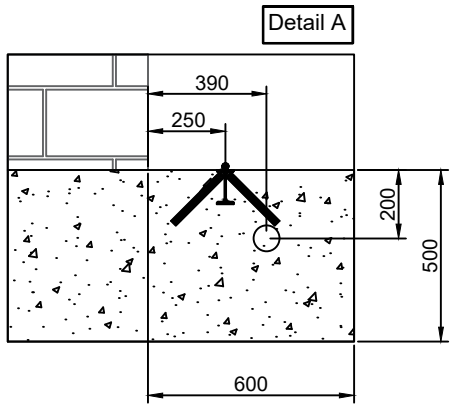

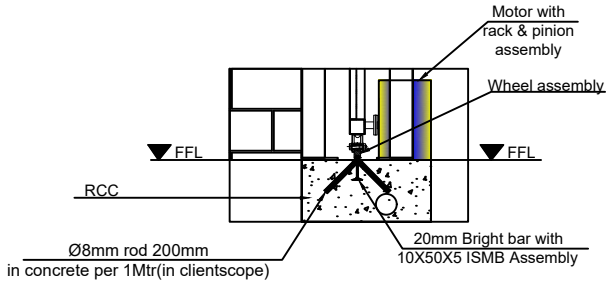

Note:-

1.All Dimension are in MM.
2.All Civil work and if required motor foundation or ms bracket will be in Client scope
3.Civil,Installation and Fabrication Tolerance will be ±20mm
4.Reuired Parking will be 10400 mm
5.Surface Finish(painting): Approved RAL

This drawing & design is the property of NIHVA TECHNOLOGIES. Not to be sold or copied to any other concern.

TITLE:- Motorized Sliding Gate Foundation

	NAME	DATE	SIGN
DRAWN	NIRMALA	02/03/2023	
CHECK	A.K	02/03/2023	
APPRD.	V.T	02/03/2023	

If any queries contact : design@nihva.com

ALL DIMENSION ARE IN mm

NIHVA TECHNOLOGIES PVT. LTD.
NIHVA TECHNOLOGIES PVT. LTD. PUNE
Tel : 020 66304033
Email:- info@nihva.com
Website:- www.nihva.com

CLIENT - Farmson Pharmaceutical Pvt. Ltd. Gujarat.

LOCATION -

PRODUCT - Motorized Sliding Gate | QTY- 01

DWG NO:- NIHVA/22-23/CLT/0187 | REV-00

SCALE: NTS | SCALE:-- 1:1 | SHEET: 01 OF 01

Rev No.	Revision	Date	Revised By