


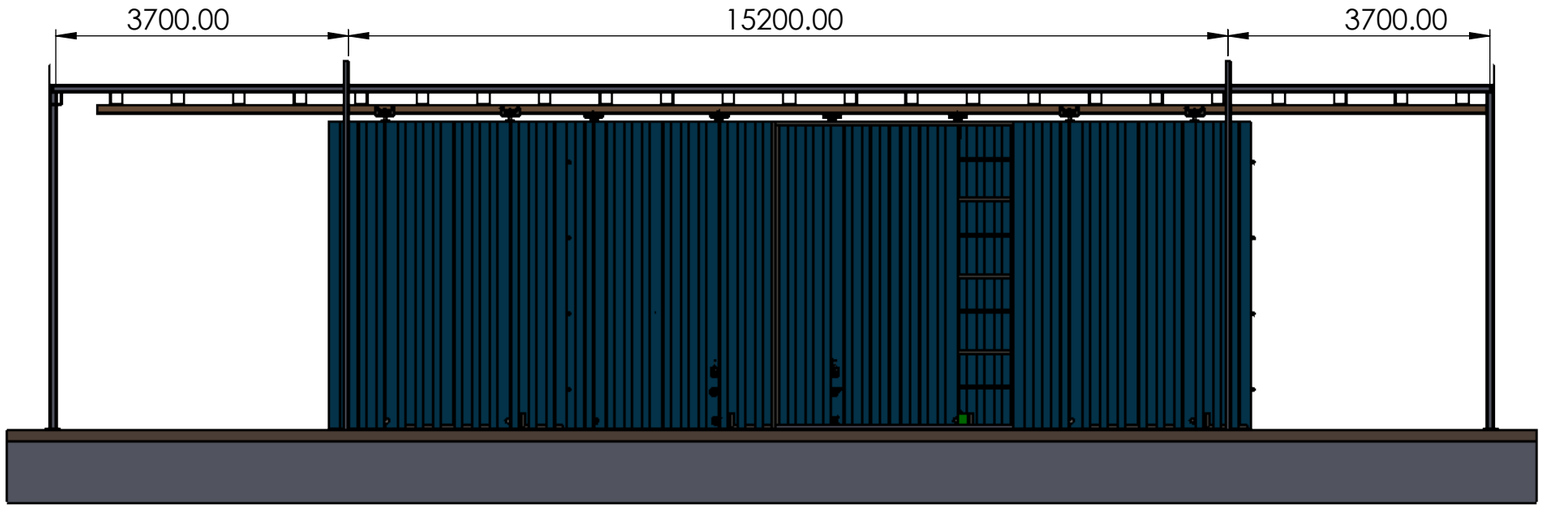


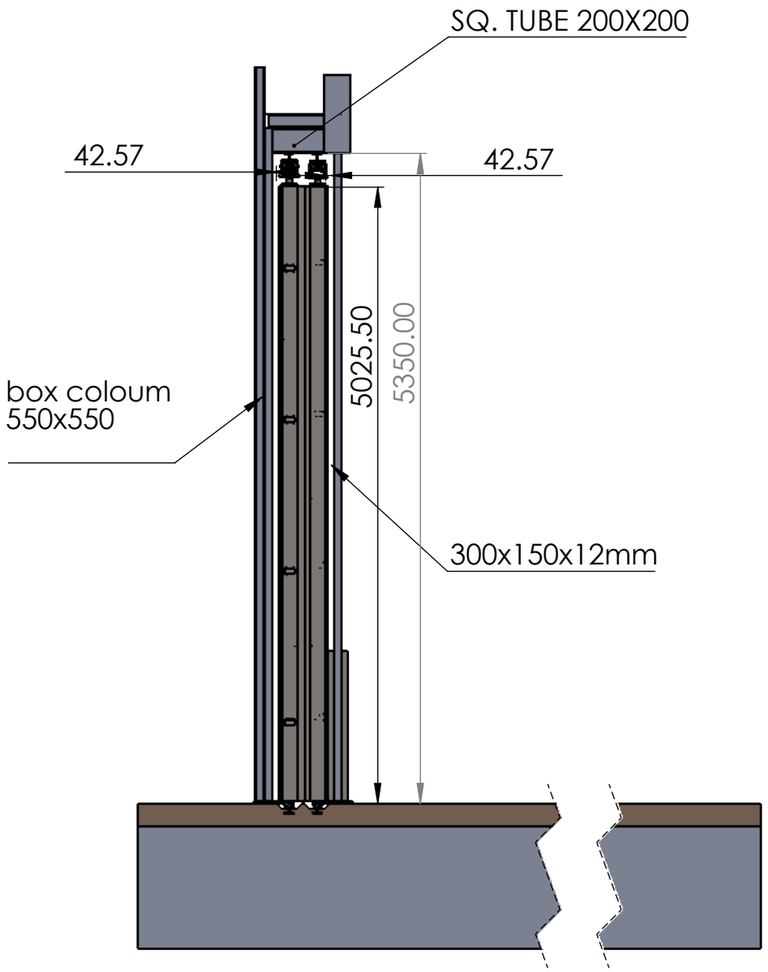


TITLE - DOOR AUTOMATION				NIHVA Technologies Pvt. Ltd.	NIHVA TECHNOLOGIES PVT.LTD.PUNE
DWG NO - NTPL-272					Website - www.nihva.com
	NAME	SIGNATURE	DATE	PROJECT NO - NTPL-272	
DRAWN	J.P		13-09-2025	PRODUCT - HANGER DOOR	REVISION -
CHK'D	V.T.		13-09-2025	SITE LOCATION - AMRAVATI	WEIGHT -
APPV'D	V.T.		13-09-2025	MATRIAL -	QTY - 1
if any queries contact - supportautomation@nihva.com				PROJECTION METHOD:	SCALE :
ALL DIMENSION ARE IN mm			A3		SHEET 1 OF 5


BOM Table			
ITEM NO.	PART NUMBER	DESCRIPTION	QTY.
1	MOTOR		1
2	SPOCKET 1	17 TEETH & 19.05MM PITCH	1
3	SPOCKET 2	32 TEETH & 19.05MM PITCH	1
4	DUEAL SOPCKET CHAIN		1
5	motor base plate		1
6	SHAFT D-40MM	FOR WHEEL (L-300MM)	1
7	HEX BOLT DIA M12x40MM(HALF THREAD)	MTL - MS	4
8	SKF_F4B 40M-TF		2

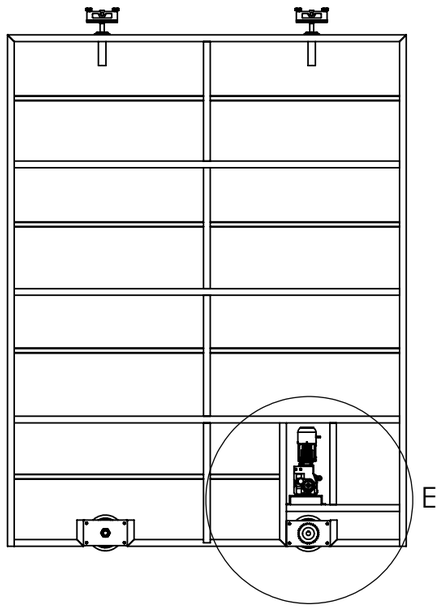

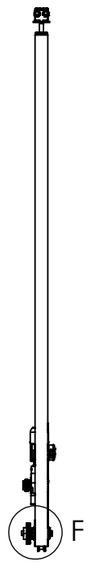

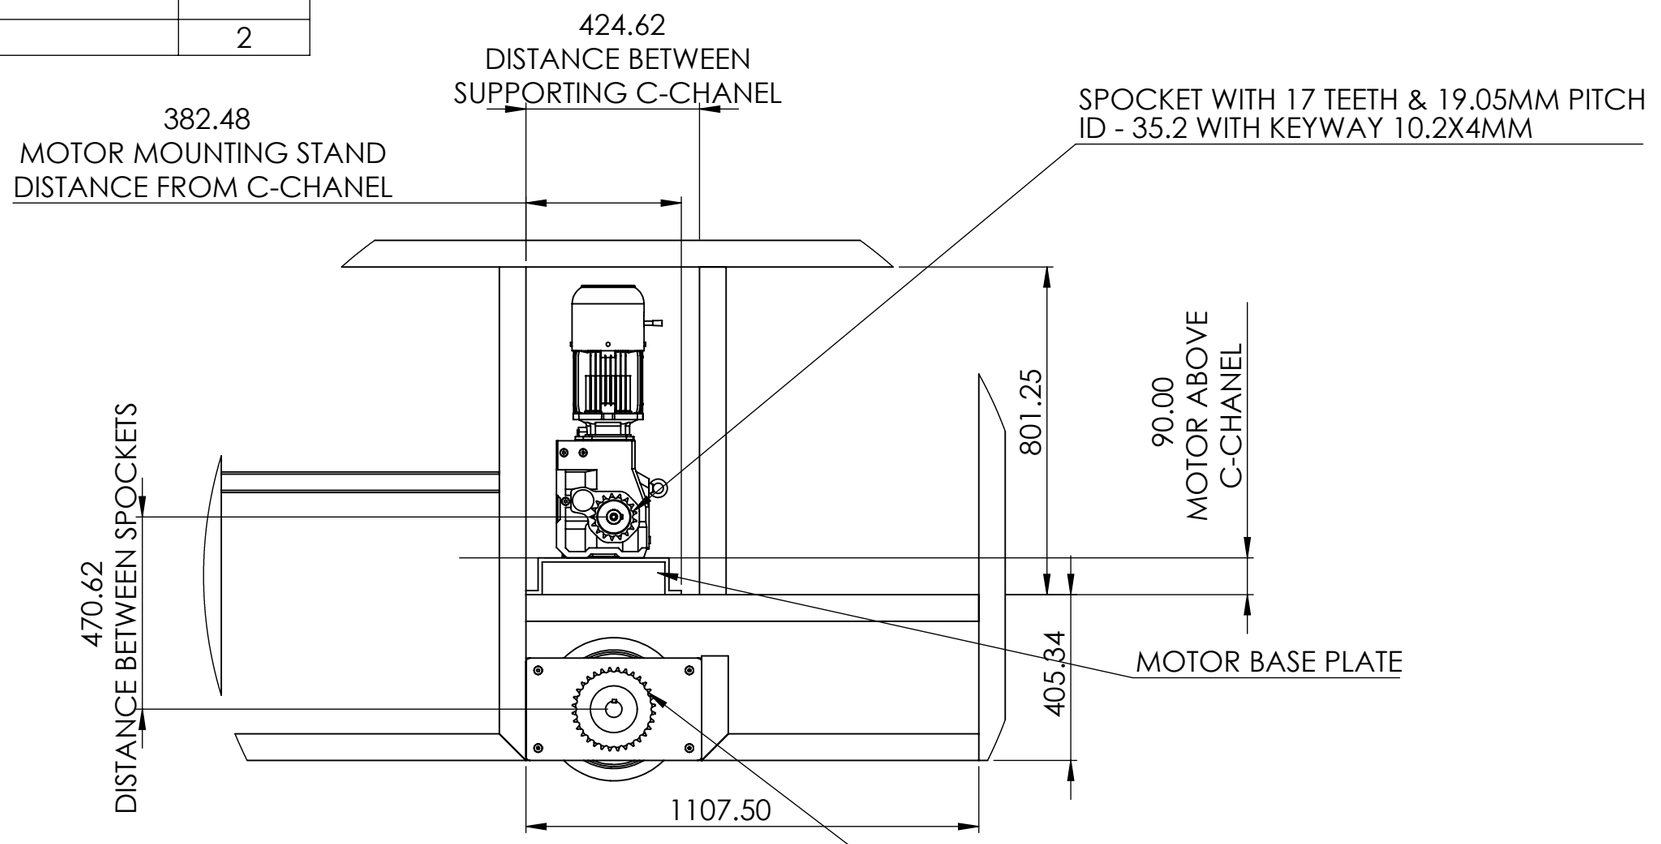

DETAIL E
SCALE 1 : 15

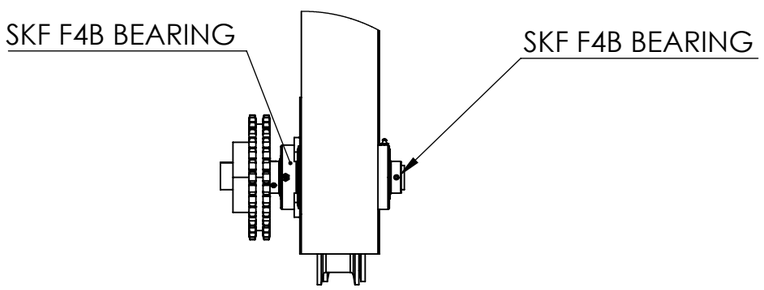


DETAIL F
SCALE 1 : 10

TITLE - DOOR AUTOMATION				NIHVA Technologies Pvt. Ltd.	NIHVA TECHNOLOGIES PVT.LTD.PUNE Website - www.nihva.com
DWG NO - NTPL-000-PM-001-00-00-00					
	NAME	SIGNATURE	DATE	PROJECT NO - NTPL-000-PM	
DRAWN	J.P		13-09-2025	PRODUCT - HANGER DOOR	REVISION -
CHK'D	V.T.		13-09-2025	SITE LOCATION -	WEIGHT -
APPV'D	V.T.		13-09-2025	MATRIAL -	QTY - 1
if any queries contact - supportautomation@nihva.com				PROJECTION METHOD:	SCALE :
ALL DIMENSION ARE IN mm			A3		SHEET 2 OF 5

sliding direction

inner view

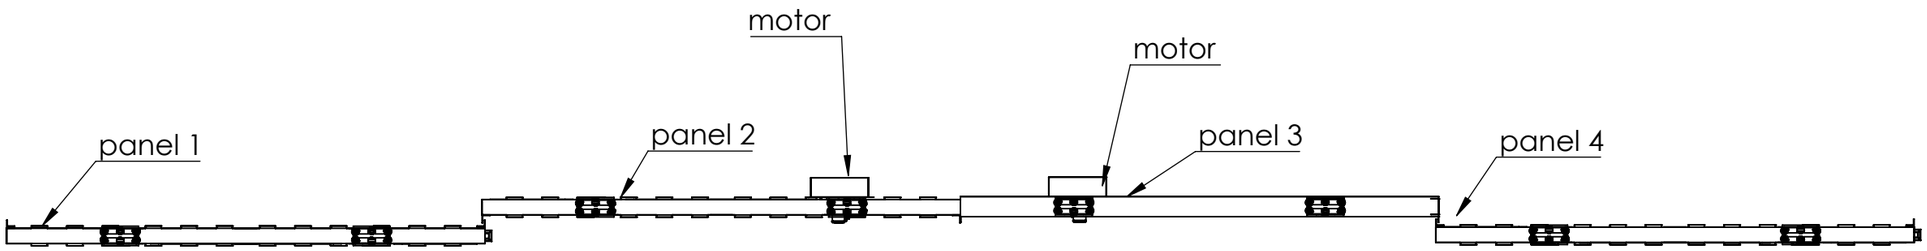


outer view

TITLE - DOOR AUTOMATION				NIHVA Technologies Pvt. Ltd. NIHVA TECHNOLOGIES PVT.LTD.PUNE Website - www.nihva.com	
DWG NO - NTPL-272					
	NAME	SIGNATURE	DATE	PROJECT NO - NTPL-272	
DRAWN	J.P		01-09-2025	PRODUCT - HANGER DOOR	REVISION -
CHK'D	V.T.		01-09-2025	SITE LOCATION - AMRAVATI	WEIGHT -
APPV'D	V.T.		01-09-2025	MATRIAL -	QTY - 1
if any queries contact - supportautomation@nihva.com				PROJECTION METHOD:	SCALE :
ALL DIMENSION ARE IN mm			A3		SHEET 3 OF 5


Step 1 - L Angle weld on a main body structure

Step 2 - After that installed corrogated sheet (scrwing)


Step 3 - After that installed side cover and motor cover (scrwing)

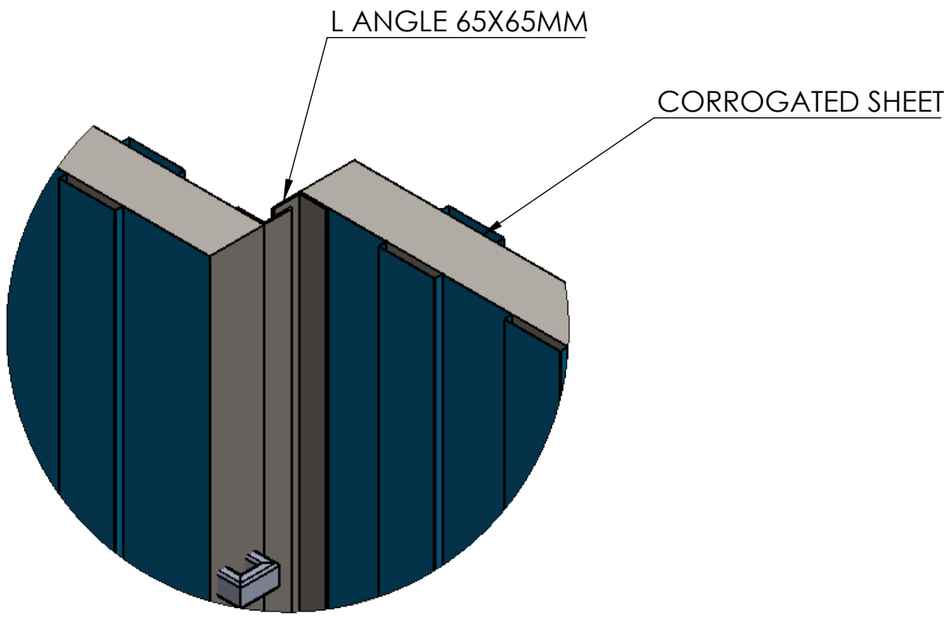

DETAIL A
SCALE 1 : 10

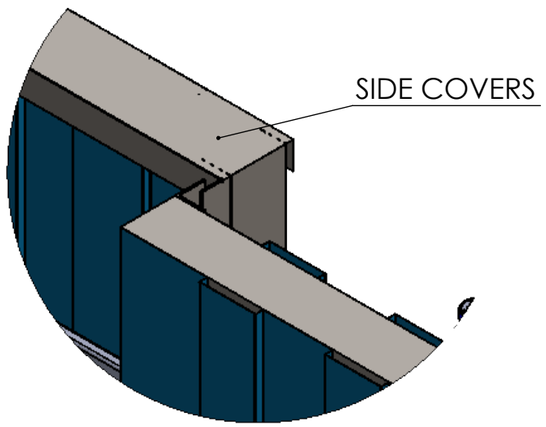


DETAIL B
SCALE 1 : 10

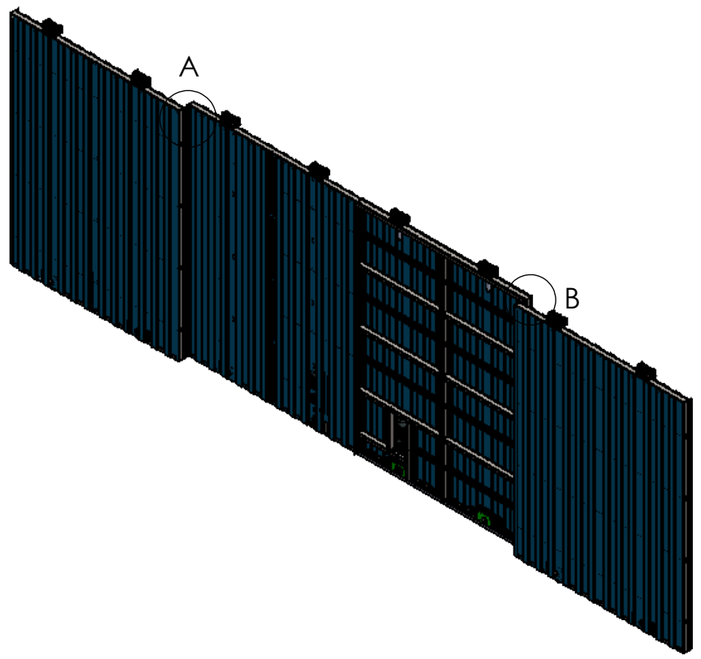


TITLE - DOOR AUTOMATION				NIHVA Technologies Pvt. Ltd.	NIHVA TECHNOLOGIES PVT.LTD.PUNE
DWG NO - NTPL-272					Website - www.nihva.com
	NAME	SIGNATURE	DATE	PROJECT NO - NTPL-272	
DRAWN	J.P		01-09-2025	PRODUCT - HANGER DOOR	REVISION -
CHK'D	V.T.		01-09-2025	SITE LOCATION - AMRAVATI	WEIGHT -
APPV'D	V.T.		01-09-2025	MATRIAL -	QTY - 1
if any queries contact - supportautomation@nihva.com				PROJECTION METHOD:	SCALE :
ALL DIMENSION ARE IN mm			A3		SHEET 4 OF 5


L ANGLE ARRAGEMENT

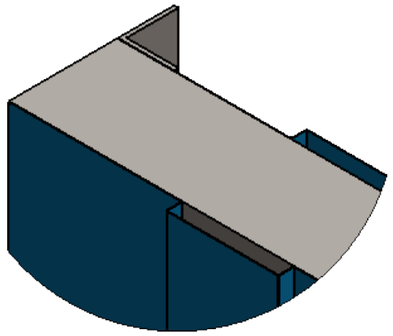

DETAIL C
SCALE 1 : 5

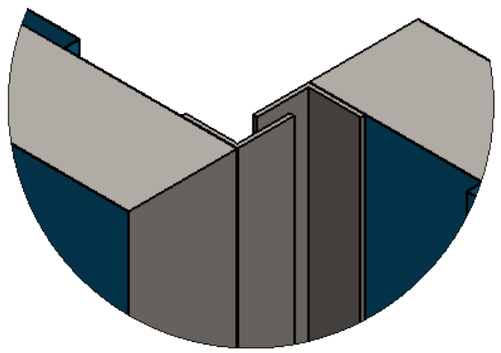

DETAIL D
SCALE 1 : 5

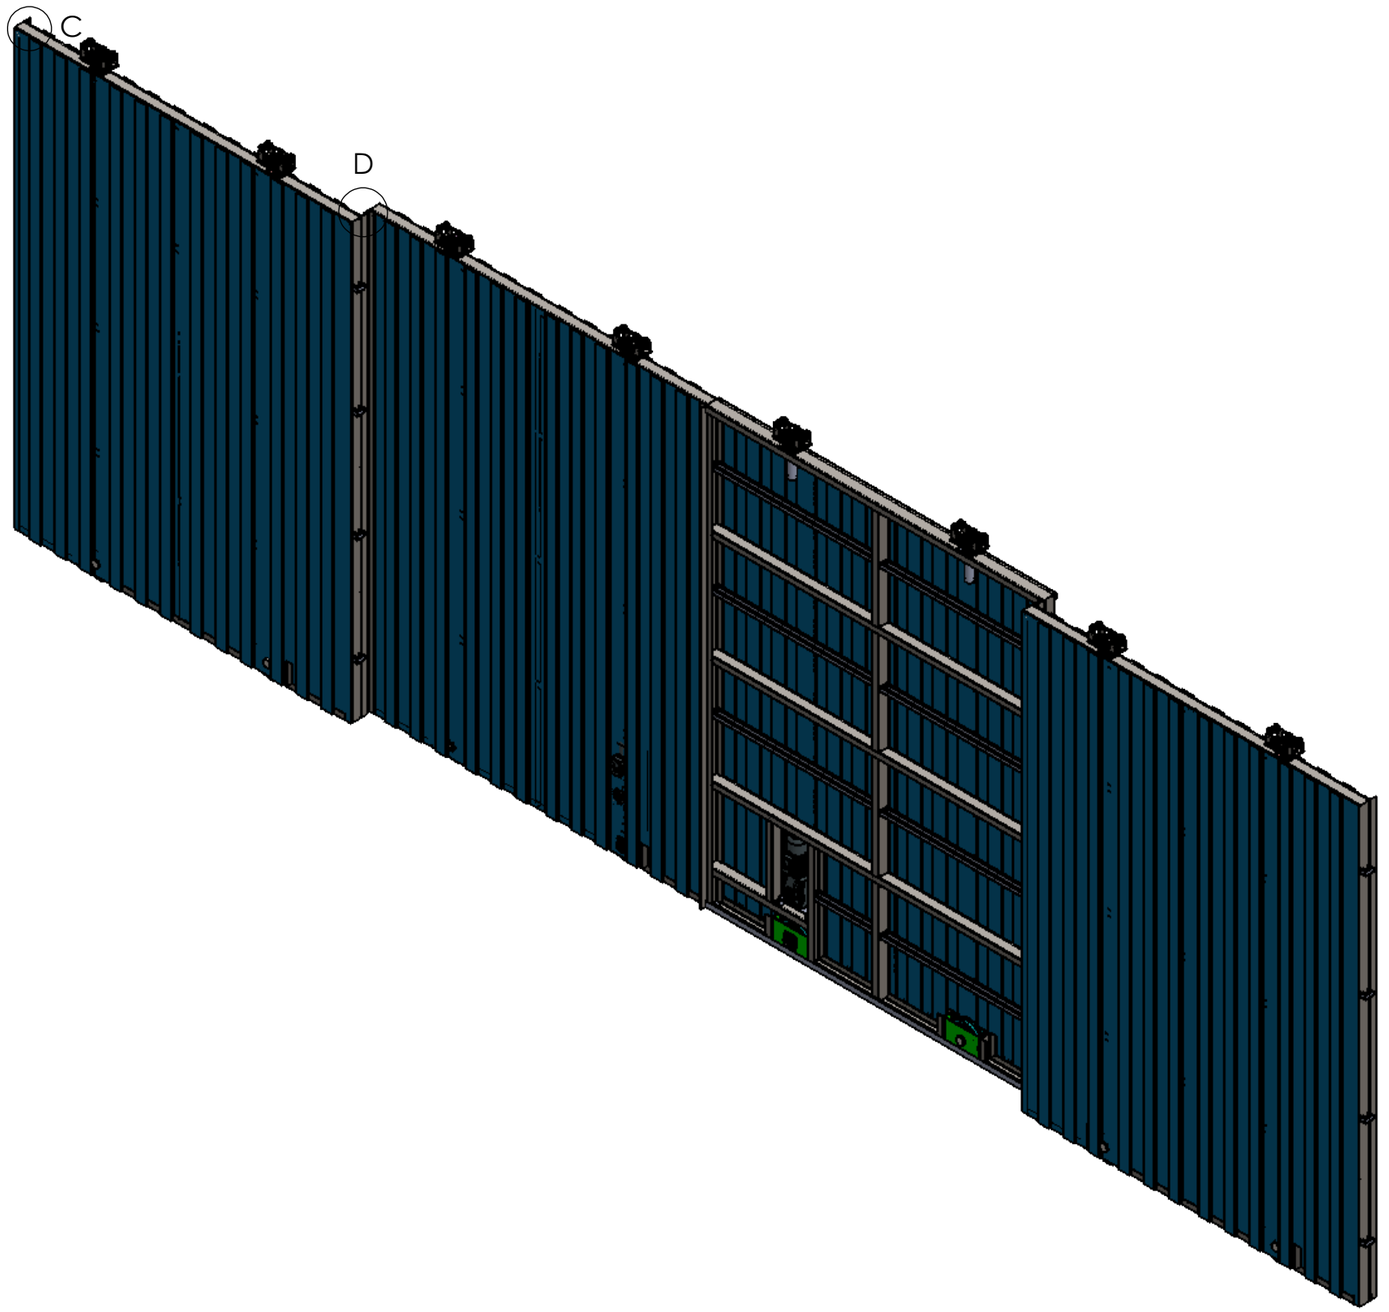

TITLE - DOOR AUTOMATION				NIHVA TECHNOLOGIES PVT.LTD.PUNE	
DWG NO - NTPL-272				Website - www.nihva.com	
	NAME	SIGNATURE	DATE	PROJECT NO - NTPL-272	
DRAWN	J.P		01-09-2025	PRODUCT - HANGER DOOR	REVISION -
CHK'D	V.T.		01-09-2025	SITE LOCATION - AMRAVATI	WEIGHT -
APPV'D	V.T.		01-09-2025	MATRIAL -	QTY - 1
if any queries contact - supportautomation@nihva.com				PROJECTION METHOD:	SCALE :
ALL DIMENSION ARE IN mm			A3		SHEET 5 OF 5