


DRAWING

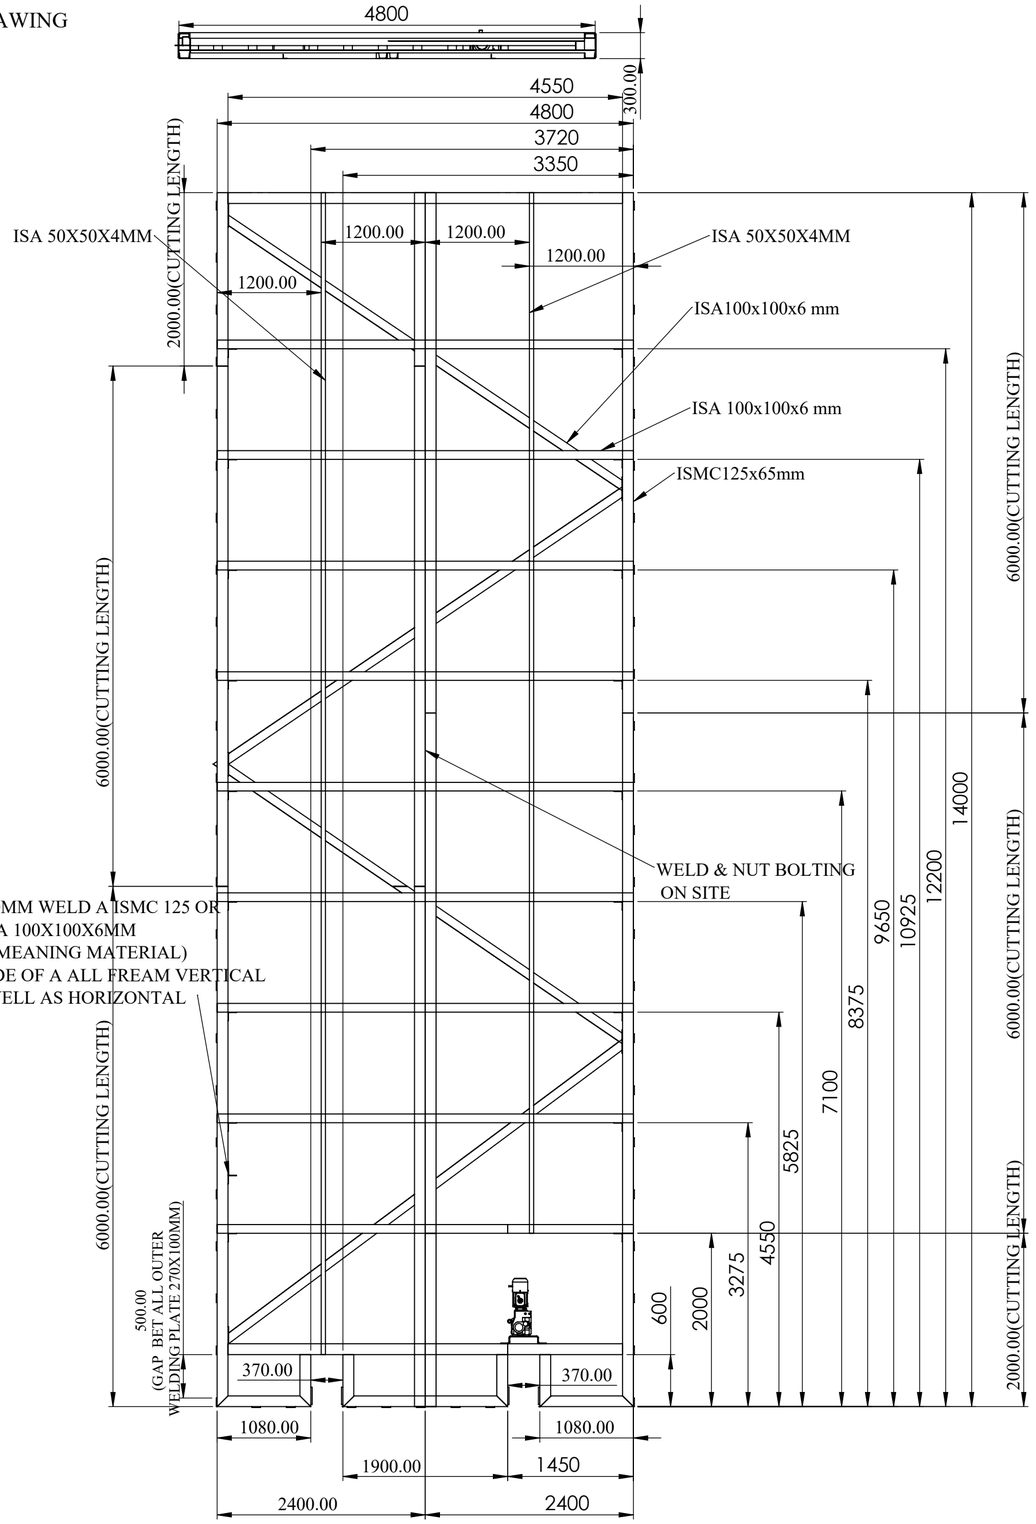


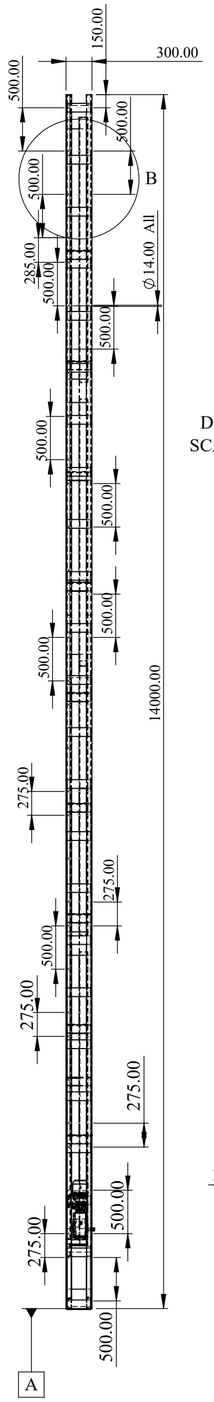


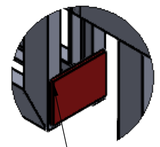

DETAIL C
SCALE 1 : 16

MOTOR BRACKET
MTG PLATE
275X200X16MM

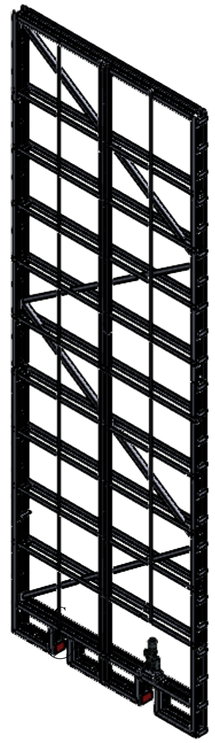

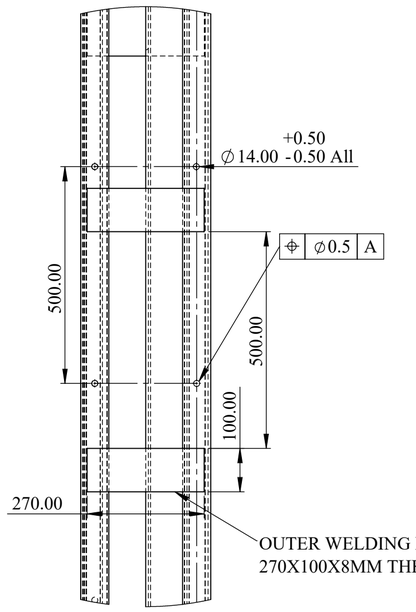

DETAIL B
SCALE 1 : 10

REV DESCRIPTION	DATE	REV NO
	08-08-2025	REV 00
1.		

NOTE :

NAME: HANGER SLINDING DOOR
SIZE: W8.6 X H14 M
INTERNAL DOOR - LEAF NO:01
QTY: 01 NOS.

SPECIAL INSTRUCTION'S :

TITLE - DOOR AUTOMATION

DWG NO - NTPL-0007-PM-001


NIHVA TECHNOLOGIES PVT.LTD.PUNE
Website - www.nihva.com

	NAME	SIGNATURE	DATE	
				PRODUCT - BI-PARTING SLIDING HANGER DOOR
DRAWN	J.P.		07-08-2026	PROJECT NO - NTPL-0007 / REVISION - 00
CHK'D	B.S.		09-08-2026	SITE LOCATION - HYDERABAD / WEIGHT -
APPV'D	V.T.		09-08-2026	MATRIAL - / QTY - 1

If any queries contact - Sales@nihva.com

ALL DIMENSION ARE IN mm | A2 | PROJECTION METHOD: | SCALE : | SHEET 1 OF 2


DRAWING

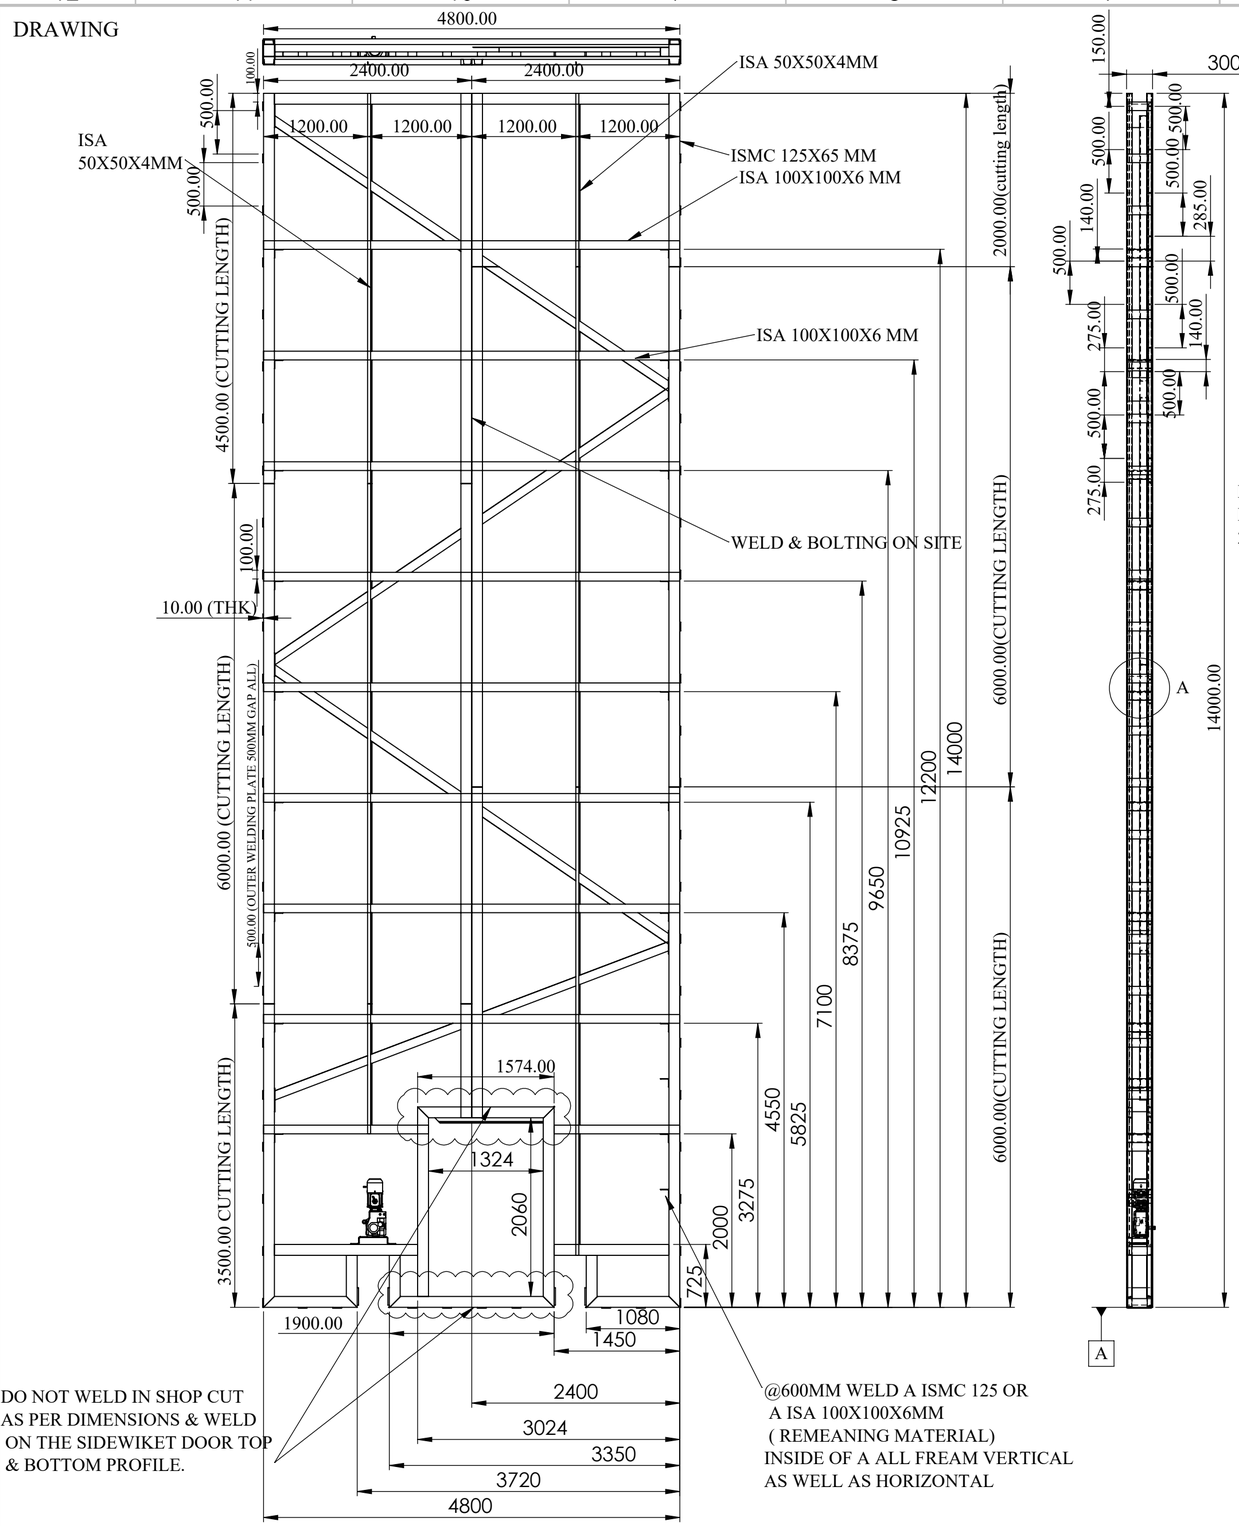




MOTOR BRACKET
MTG PLATE
275X200X16MM

DETAIL D
SCALE 1 : 15

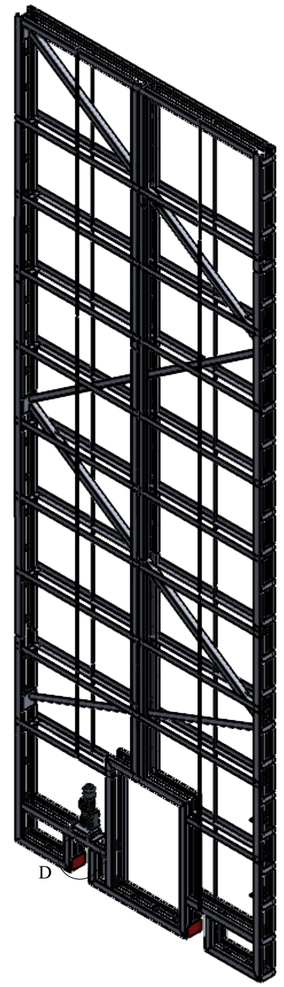

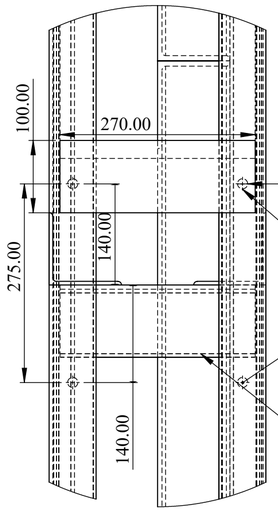

+0.50
∅14.00 -0.50 ALL

⌖ ∅0.5-Ⓜ A

14MM HOLE DIA
ALLOWED TOLERANCE
+/- 0.5MM

OUTER WELDING PLATE
270X100X8MM THK EACH

DETAIL A
SCALE 1 : 6

DO NOT WELD IN SHOP CUT
AS PER DIMENSIONS & WELD
ON THE SIDEWIKET DOOR TOP
& BOTTOM PROFILE.

@600MM WELD A ISMC 125 OR
A ISA 100X100X6MM
(REMEANING MATERIAL)
INSIDE OF A ALL FREAM VERTICAL
AS WELL AS HORIZONTAL

REV DESCRIPTION	DATE	REV NO
	08-08-2025	REV 00
1.		

NOTE :

NAME: HANGER SLINDING DOOR
SIZE: W8.6 X H14 M
INTERNAL DOOR - LEAF NO:02
QTY: 01 NOS.

SPECIAL INSTRUCTION'S :

TITLE - DOOR AUTOMATION			
DWG NO - NTPL-0007-PM-001			
NIHVA Technologies Pvt. Ltd.	NIHVA TECHNOLOGIES PVT.LTD.PUNE Website - www.nihva.com		
	NAME	SIGNATURE	DATE
DRAWN	J.P.		07-08-2026
CHK'D	B.S.		09-08-2026
APPV'D	V.T.		09-08-2026
PRODUCT - BI-PARTING SLIDING HANGER DOOR			
PROJECT NO - NTPL-0007	REVISION - 00		
SITE LOCATION - HYDERABAD	WEIGHT -		
MATRIAL -	QTY - 1		
If any queries contact - Sales@nihva.com	PROJECTION METHOD:	SCALE :	
ALL DIMENSION ARE IN mm A2		SHEET 2 OF 2	