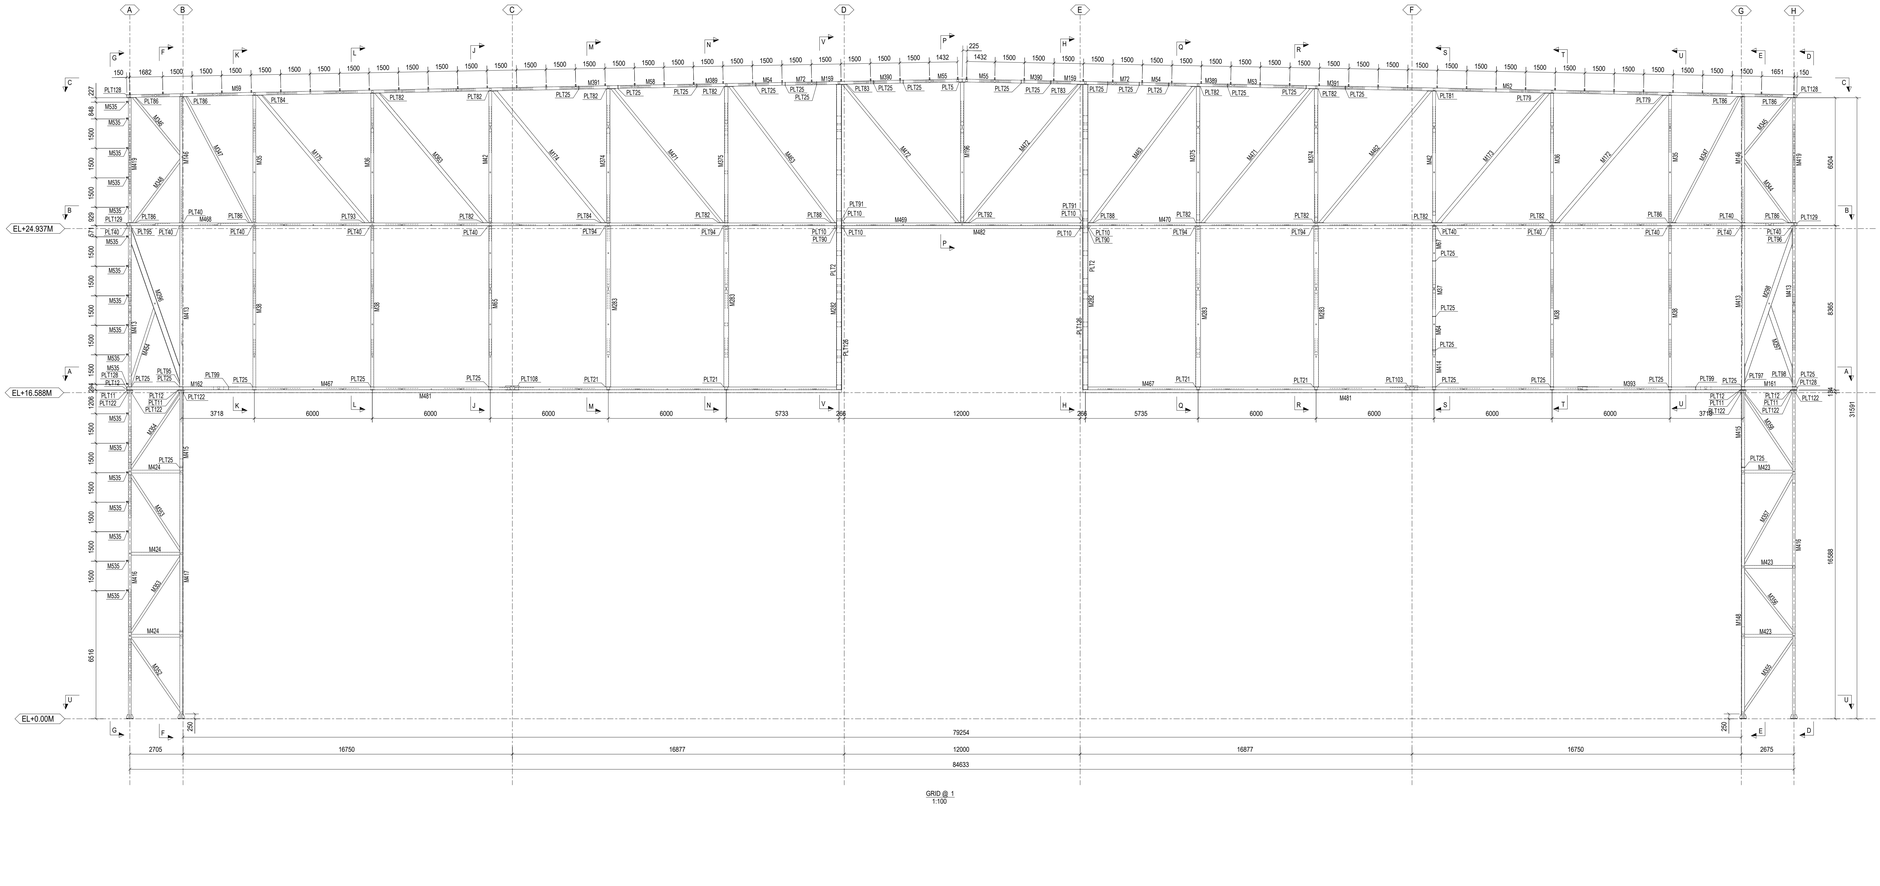
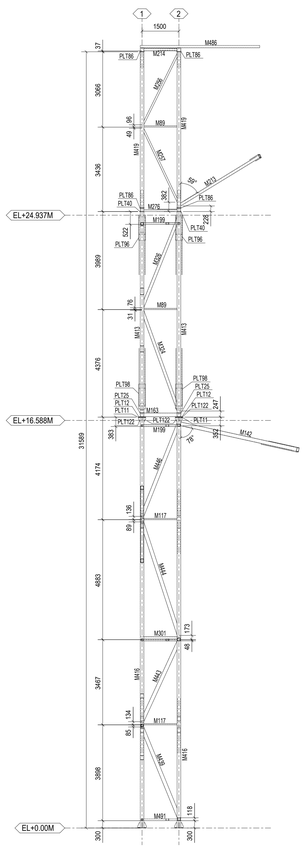
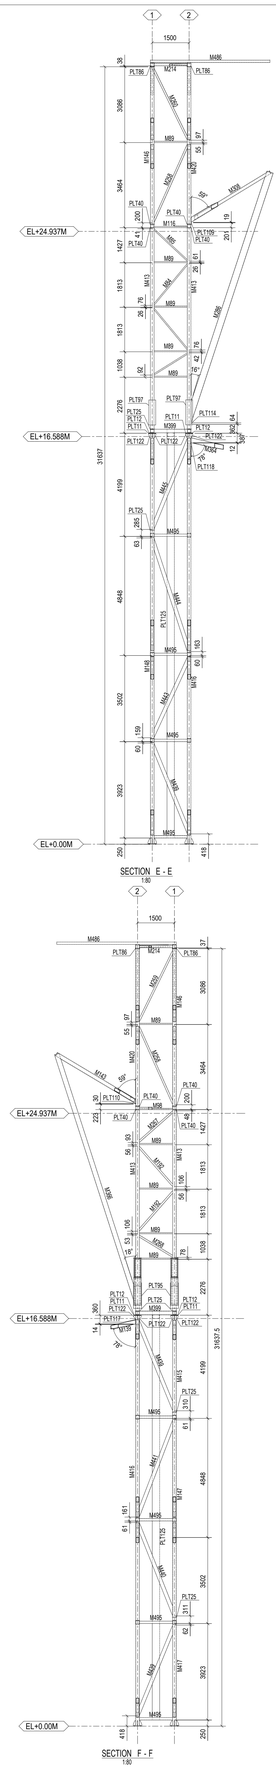
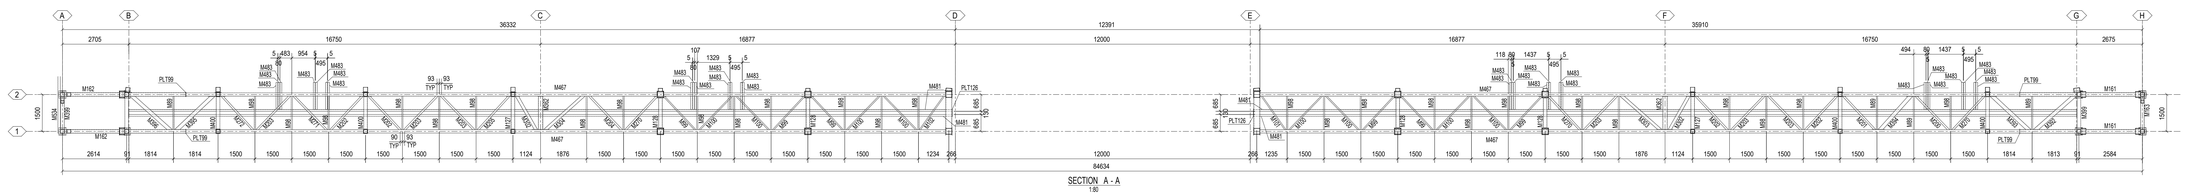
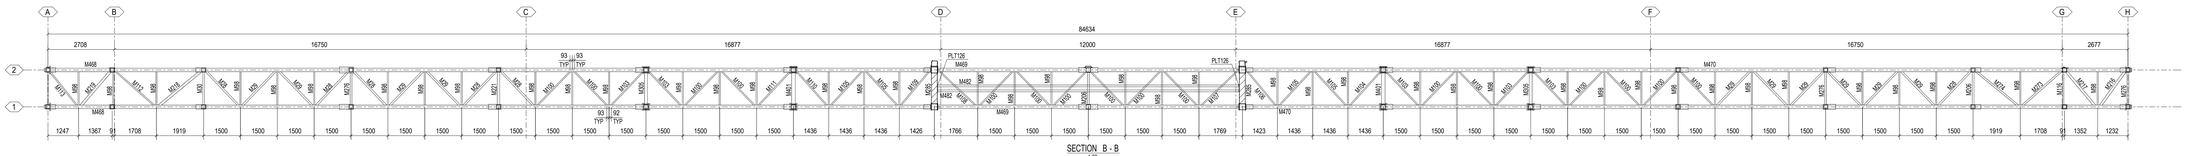
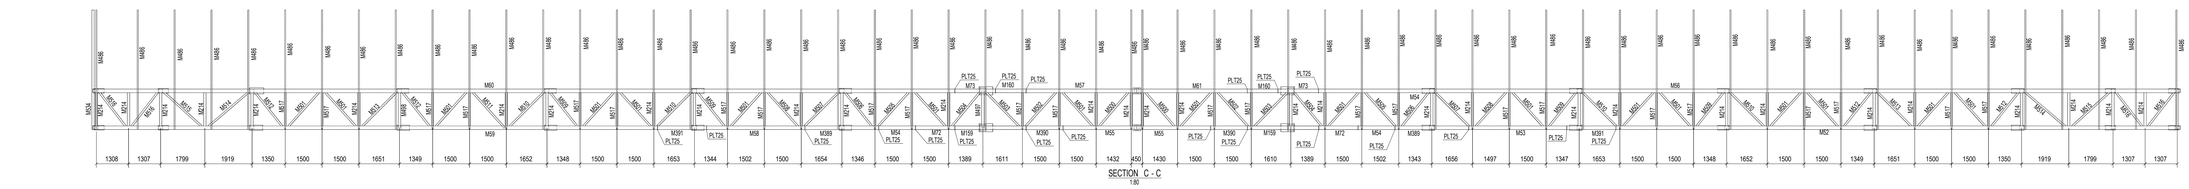

EL+24.937M
EL+16.588M
EL+0.00M
GRID @ 1
1:100


EL+24.937M
EL+16.588M
EL+0.00M
SECTION D - D
1:80


EL+24.937M
EL+16.588M
EL+0.00M
SECTION E - E
1:80
SECTION F - F
1:80


SECTION A - A
1:80


SECTION B - B
1:80


SECTION C - C
1:80


SECTION U - U
1:80