


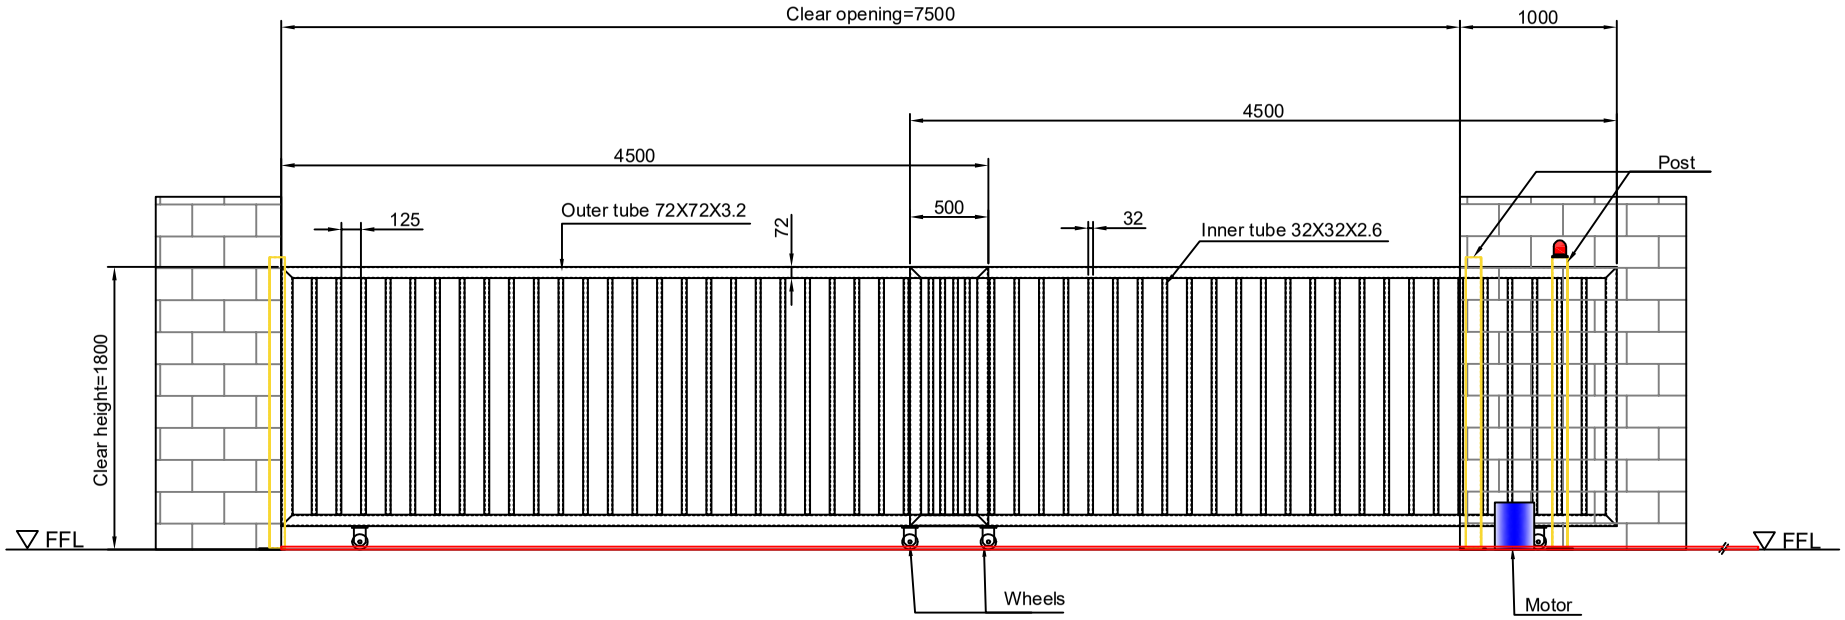

Opening direction

Note:-

1.All dimension are in MM

2.Above given drawing is only for the client understanding purpose

2.1 Outer tube will be 72X72X3.2mm

2.2 Inner tube will be 32X32X2.6mm

3.Required parking space will be 4600mm

4.All civil work will be in client scope

This drawing & design is the property of NIHVA TECHNOLOGIES. Not to be sold or copied to any other concern.

TITLE:- Two Leaf for tel.sliding gate

	NAME	DATE	SIGN
DRAWN	SUJATA	22/02/2022	
CHECK	G.PATIL	22/02/2022	
APPRD.	A.K	22/02/2022	

If any queries contact : design@nihva.com

ALL DIMENSION ARE IN mm

NIHVA TECHNOLOGIES PVT. LTD.
NIHVA TECHNOLOGIES PVT. LTD. PUNE
Tel : 020 66304033
Email:- info@nihva.com
Website:- www.nihva.com

CLIENT - Kunal Structure Ind. Pvt. Ltd

LOCATION - Gujrat (Diyodar)

PRODUCT - Tel.sliding gate | QTY-

DWG NO:- NIHVA/21-22/CLT/0357 | REV- 0

SCALE: NTS | SCALE:-- 1:1 | SHEET: 01 OF 01

Rev No.	Revision	Date	Revised By