
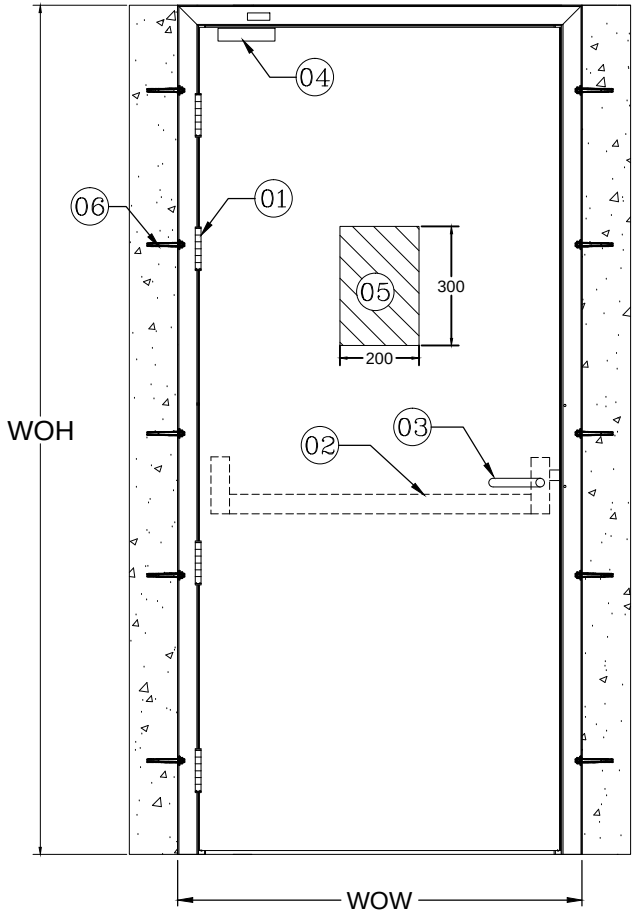


IN SIDE

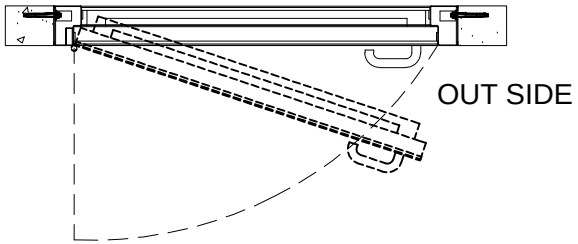

OUT SIDE

Abbrevation's:
WOW-Wall Opening Width
WOH-Wall Opening Height

HARDWARE LIST:-

SR.NO	DESCRIPTION	QTY.
01	HINGES	04 Nos.
02	PANIC BAR SINGLE POINT	01 No.
03	EXTERNAL TRIM	01 No.
04	DOOR CLOSER	01 No.
05	VISION PANEL 200X300	01 No.
06	ANCHOR FASTENERS	10 Nos.

DOOR OPENING TYPE: TYPE 3 - LEFT HAND REVERSE

(for opening type refer door handling sheet)

Door Sizes :-

SR.NO	WOW	WOH	QTY.
01	1200	2480	01 No.
02	1190	2500	01 No.

COLOR : RAL 9016 TRAFFIC WHITE

NOTE:-
*All Dimensions are in mm.
*Tolerance:-All Linear Dimensions ±3mm,Others ±0.5mm.
*The Drawing Is For Location of Hardware only. Drawing Does Not Represent The Hardware For More Clarity, Please Go Through Hardware Broucher.

NIHVA TECHNOLOGIES PVT. LTD.
NIHVA TECHNOLOGIES PVT. LTD. PUNE
Email:- info@nihva.com
Website:- www.nihva.com

TITLE:
FIRE DOOR

CLIENT'S APPROVAL :

CLIENT - RUTCON CONSTRUCTION PROJECT PVT. LTD.

PROJECT - JISL SITE HUBBALLI

SITE LOCATION -

DWG. NO. : NIHVA/16-17/0046

SCALE: NTS	WT:	SHEET:1 OF 1

DRAWN BY: ANIL KHOT DATE: 23-07-2016

CHECK : ANIL DATE: 23-07-2016

If any queries contact : projects@nihva.com

NOTE: ALL DIMENSION ARE IN mm

THIS DRAWING & DESIGNING IS THE PROPERTY OF NIHVA TECHNOLOGIES. NOT BE SOLD OR COPY TO ANY OTHER CONCERN.