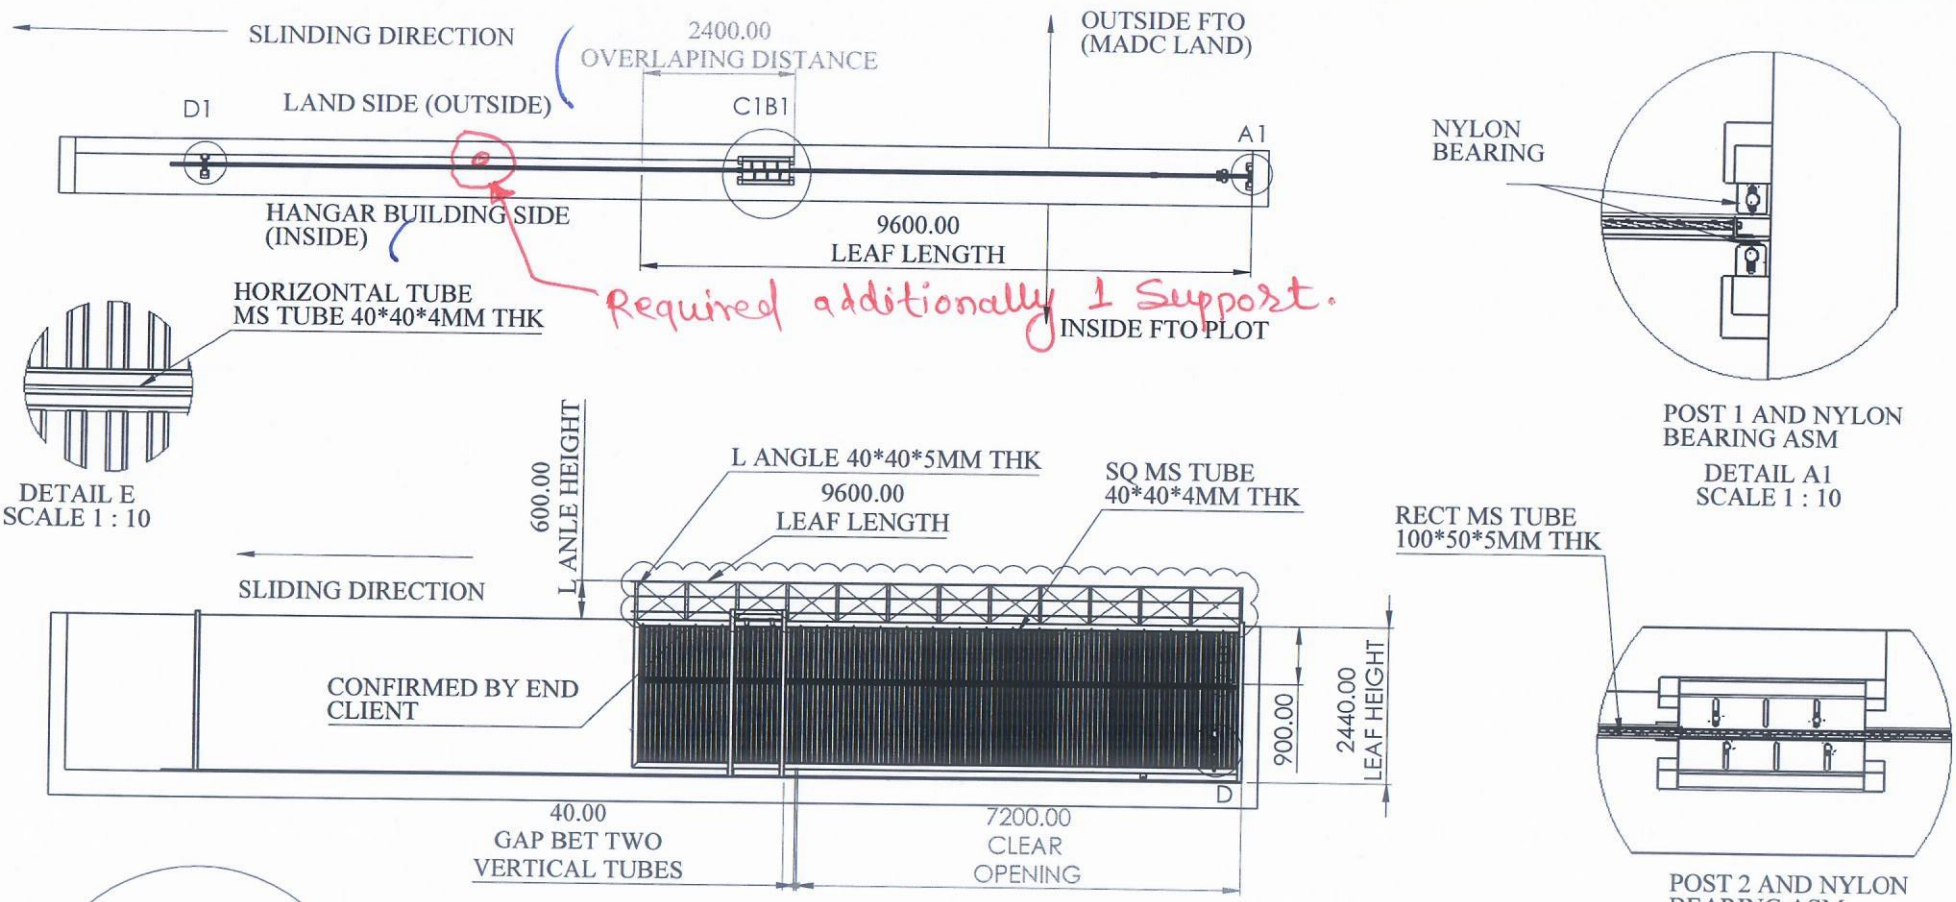



DETAIL E
SCALE 1 : 10

POST 1 AND NYLON
BEARING ASM

DETAIL A1
SCALE 1 : 10


POST 2 AND NYLON
BEARING ASM

DETAIL C1B1
SCALE 1 : 20

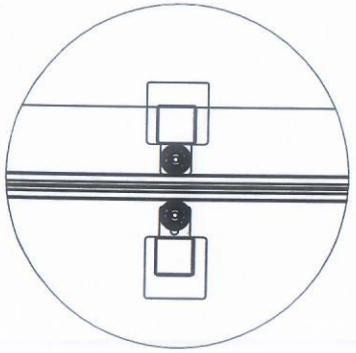

POST NO 3 &
NYLON ROLLER BERAING
ASM

DETAIL D1
SCALE 1 : 10

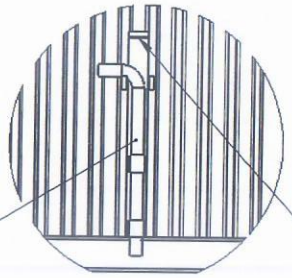


TOWER BOLT LOCKING
ARRANGEMENT.


DETAIL D
SCALE 1 : 15

NOTE :


1)GA DRAWING TYPE NO 01
2)Total column -04 (A1,B1,C1,D1)
3) 03 column posts when the gates is in the closed position.(A1,B1,C1)
4) 03 column posts when the gates is in the fully open position.(B1,C1,D1)
5) barbed wire design is zigzag pattern.


TITLE - GATE AUTOMATIOM				NIHVA TECHNOLOGIES PVT.LTD.PUNE
DWG NO - NTPL-000-PM-001-00-00-00				Website - www.nihva.com
	NAME	SIGNATURE	DATE	PROJECT NO - NTPL-000-PM
DRAWN	V.W		21-05-2025	PRODUCT - SINGLE SLIDING GATE
CHK'D	S.W.		21-05-2025	SITE LOCATION -
APPV'D	V.T.		21-05-2025	
if any queries contact - supportautomation@nihva.com				REVISION - 01 / QTY - 1
ALL DIMENSION ARE IN mm			A3	SCALE / SHEET 1 OF 1

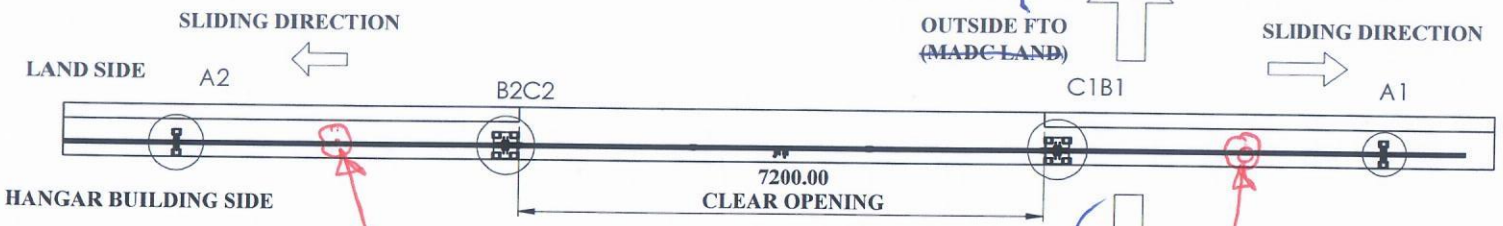

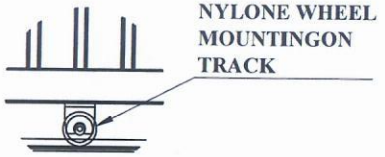


DETAIL H
SCALE 1 : 15

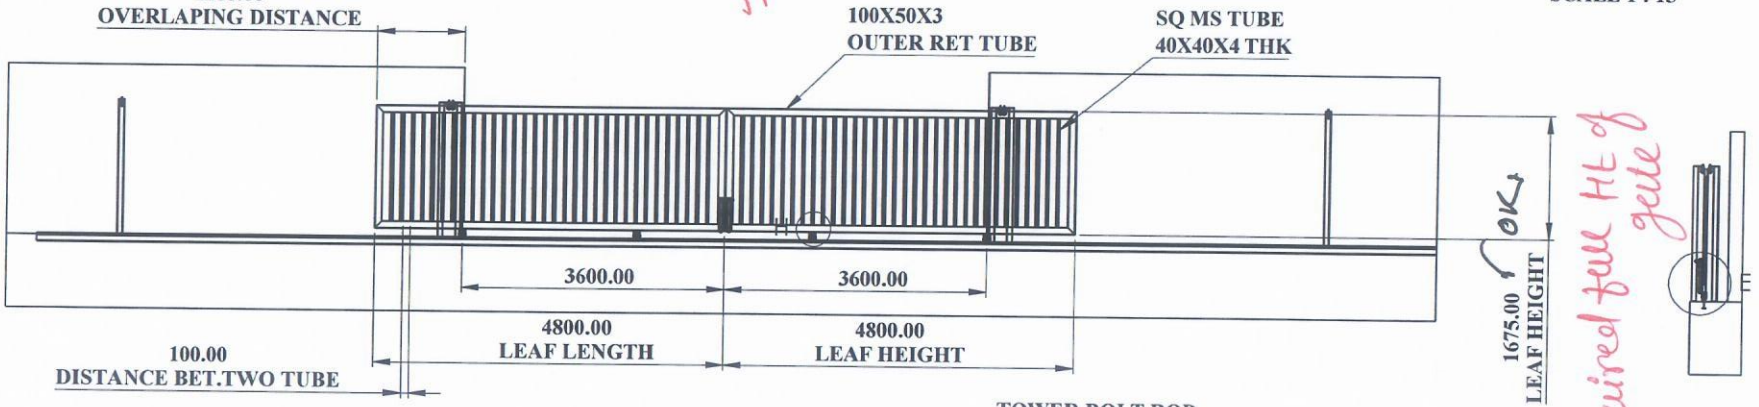

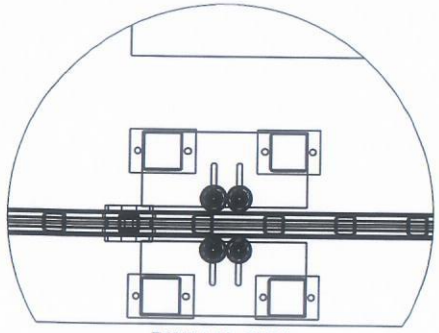


DETAIL C1B1
SCALE 1 : 10

POST1 AND NYLON
BEARING ASM

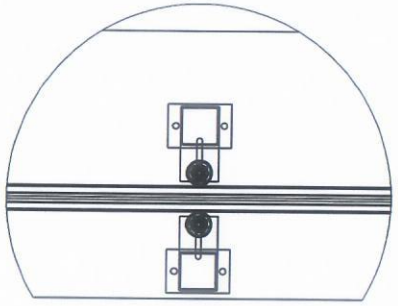

DETAIL A2
SCALE 1 : 10

POST 2 AND NYLON
BEARING ASM

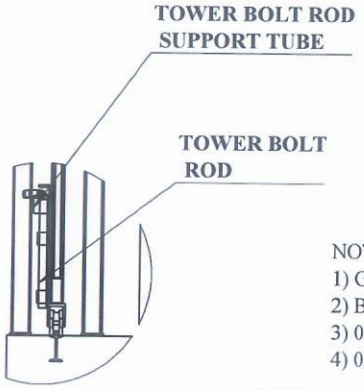


DETAIL SCALE E
1 : 20

TOWER BOLT LOCKING
ARRANGEMENT


NOTE:
1) GA DRAWING TYPE NO 03
2) BARBED WIRE IS NOT MENTION IN DWG.
3) 03 column posts when the gate is in the closed position.(A1,B1,C1 &A2,B2,C2)
4) 03 column posts when the gate is in the closed position.(A1,B1,C1 &A2,B2,C2)

TITLE - GATE				NIHVA TECHNOLOGIES PVT.LTD.PUNE
DWG NO - NTPL			QTY - 1	Website - www.nihva.com
	NAME	SIGNATURE	DATE	PROJECT NO - NTPL
DRAWN	V.B.		28-05-2025	PRODUCT - BY PARTING SLIDING GATE
CHK'D	S.W.		28-05-2025	SITE LOCATION - AMRAVATI
APPV'D	V.T.		28-05-2025	
if any queries contact - supportautomation@nihva.com				REVISION -
ALL DIMENSION ARE IN mm			A3	SCALE - SHEET 1 OF 1

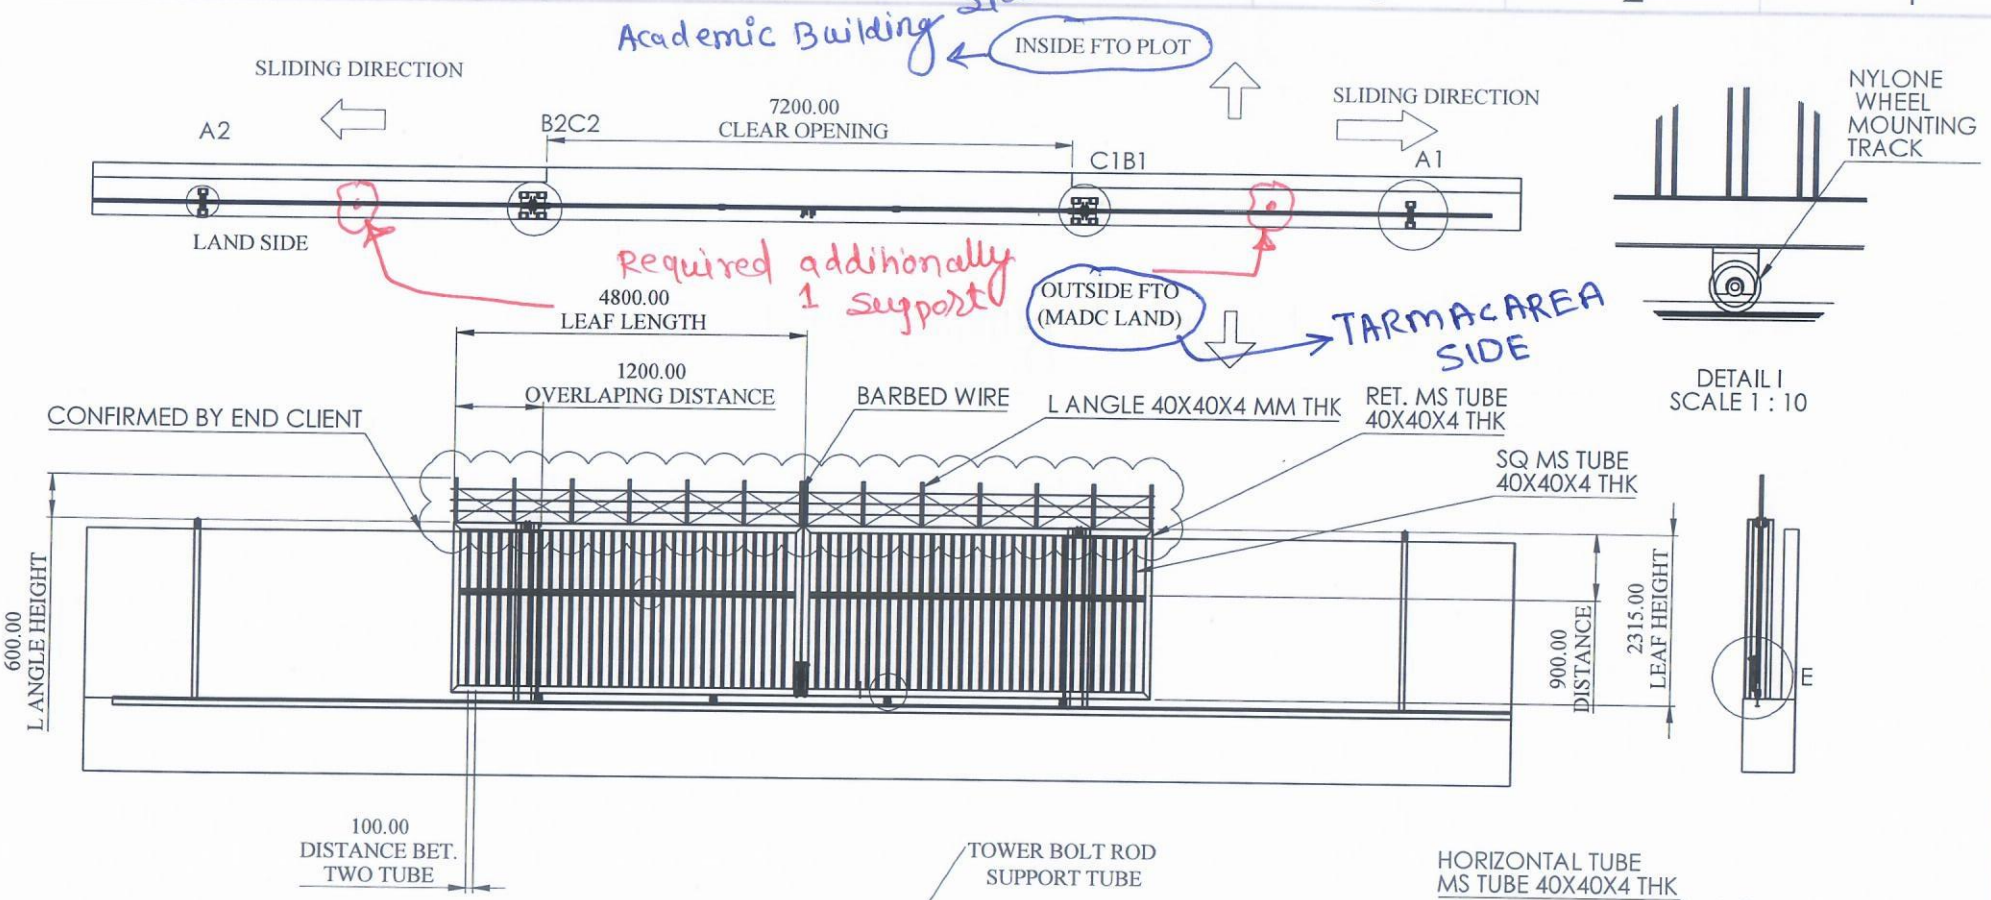


NOTE: 1) GA DRAWING TYPE NO 02
2) BARBED WIRE DESIGN IS ZIGZAG PATTERN.
3) 03 column posts when the gate is in the closed position.(A1,B1,C1 &A2,B2,C2)
4) 03 column posts when the gate is in the closed position.(A1,B1,C1 &A2,B2,C2)


TITLE - GATE				NIHVA TECHNOLOGIES PVT.LTD.PUNE
DWG NO - NTPL268-PM			QTY - 1	Website - www.nihva.com
	NAME	SIGNATURE	DATE	PROJECT NO - NTPL268-PM- AD
DRAWN	V.B.		21-03-2025	PRODUCT - BY PARTING SLIDING GATE
CHK'D	S.W.		21-03-2025	SITE LOCATION -
APP'V'D	V.T.		21-03-2025	
if any queries contact - supportautomation@nihva.com				REVISION -
ALL DIMENSION ARE IN mm			A3	SCALE - SHEET 1 OF 1

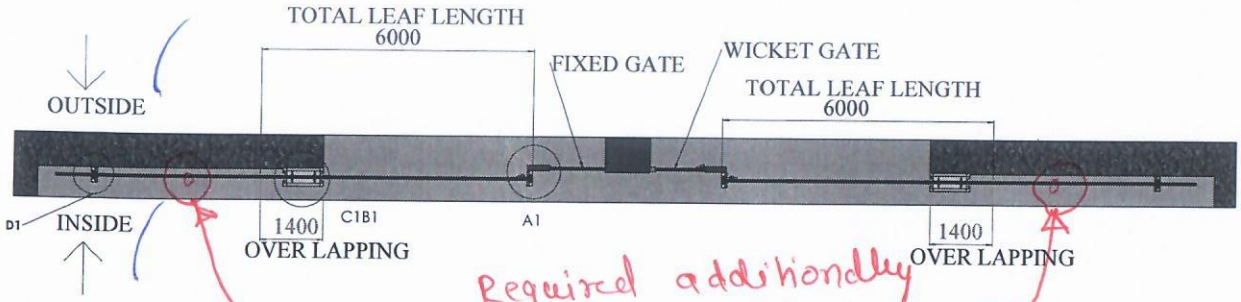

Required additionally 1 support

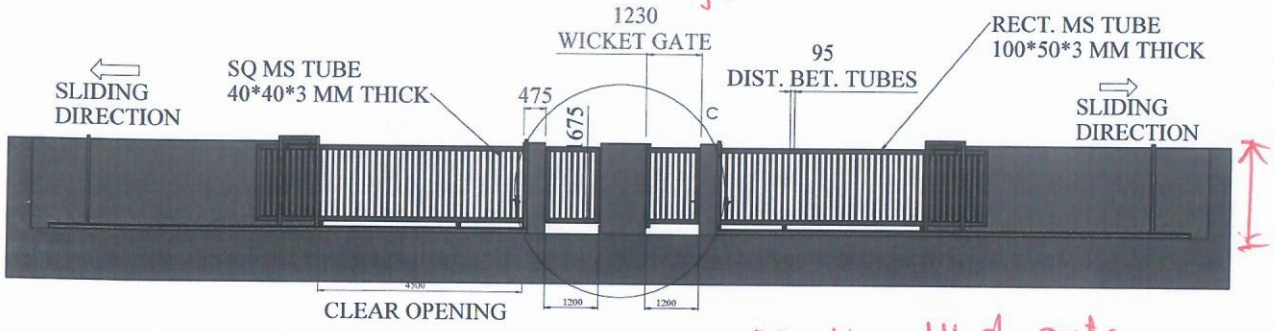


Mention Ht of gate.

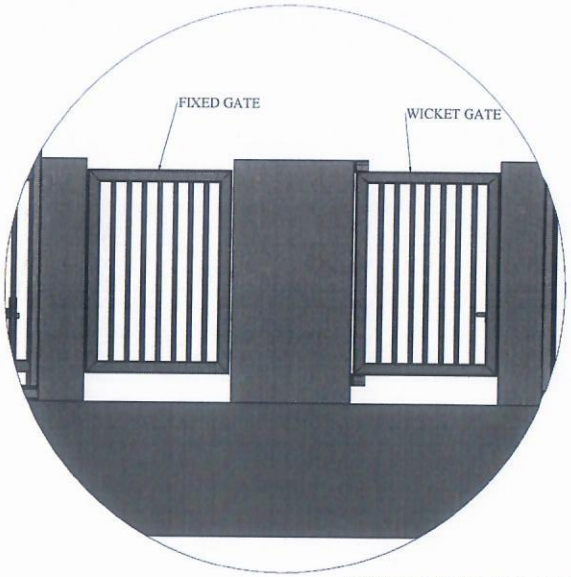


FIXED GATE AND SWING GATE VIEW

DETAIL C
SCALE 1 : 15

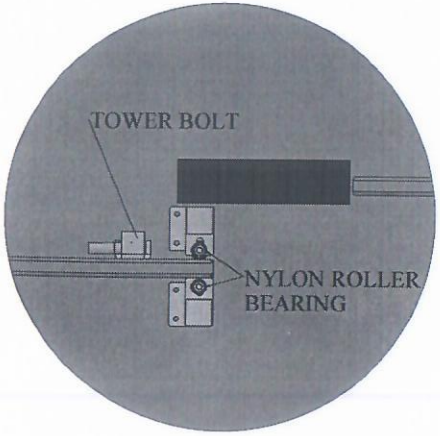


POST 1 AND NYLON ROLLER BEARING ASSEM.

DETAIL A1
SCALE 1 : 5

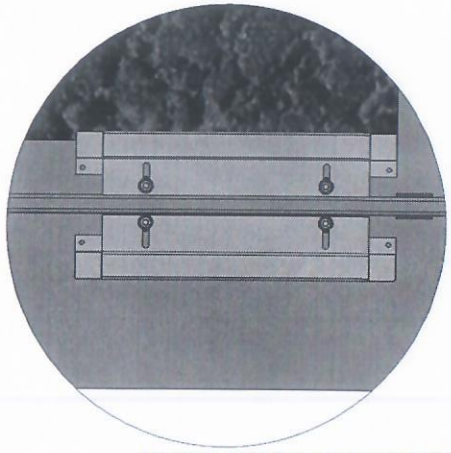

POST 2 AND NYLON ROLLER BEARING ASSEM.


DETAIL C1B1
SCALE 1 : 5

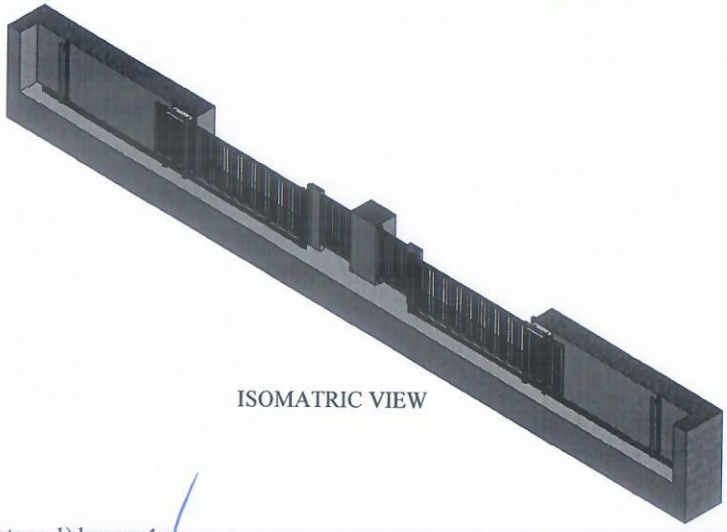


ISOMATRIC VIEW


Note : - 1)dwg no 4
2) barbed wire is not menstion in this dwg.
3)Total column -04 (A1,B1,C1,D1)
4) 03 column posts when the gates is in the closed position.(A1,B1,C1)
5) 03 column posts when the gates is in the fully open position.(B1,C1,D1)

SBFINAL ASSM. GA DRAWING

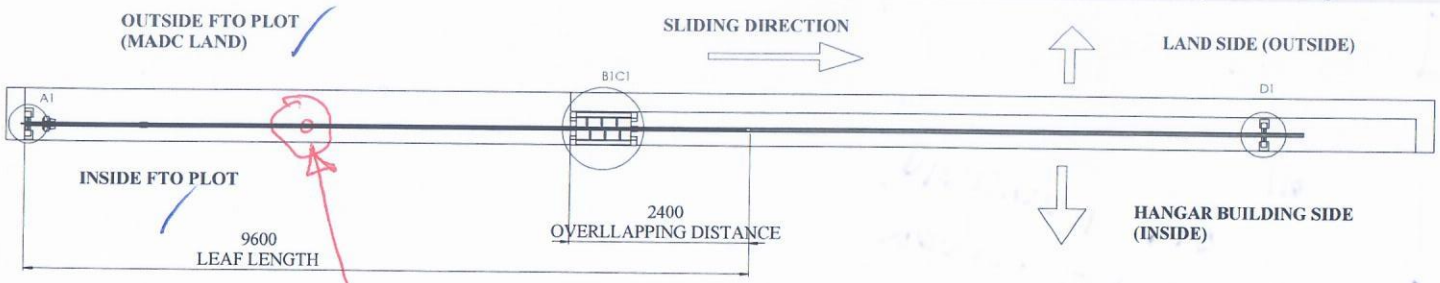


Required Additionally 1 Support

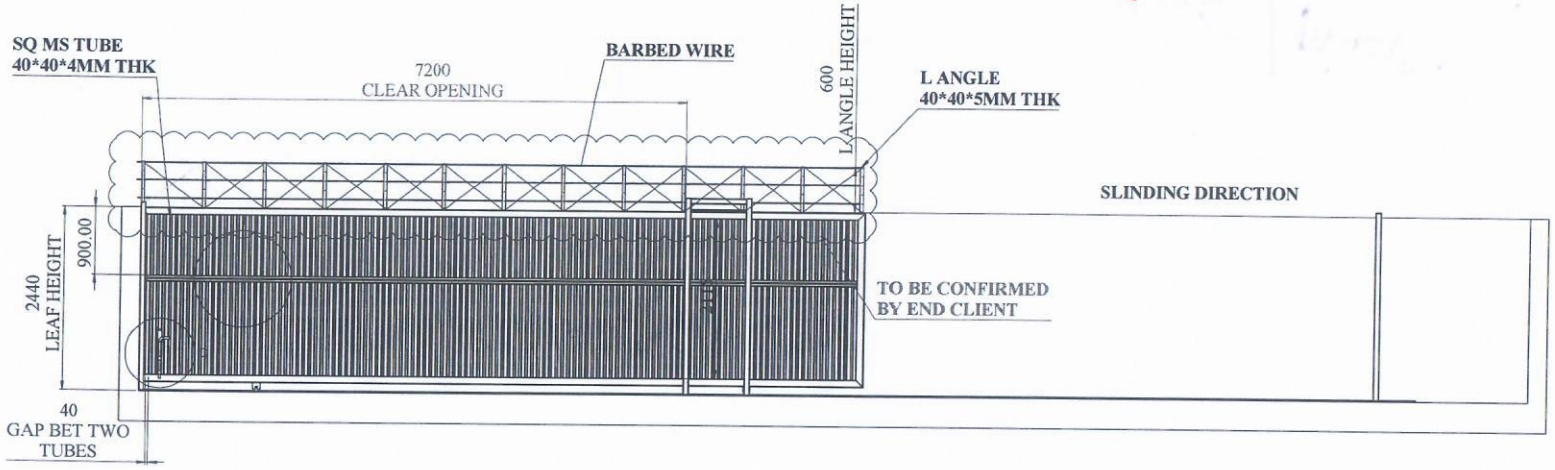

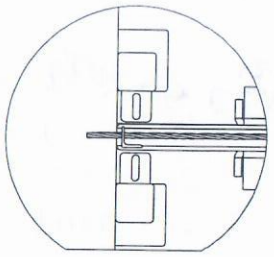


POST 1 & NYLON
ROLLER ASM

DETAIL A1
SCALE 1 : 5

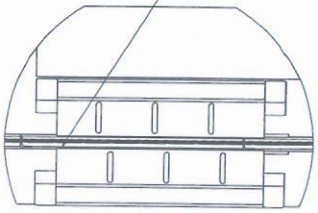


POST 2 & NYLON
ROLLER ASM
DETAIL B1C1
SCALE 1 : 9

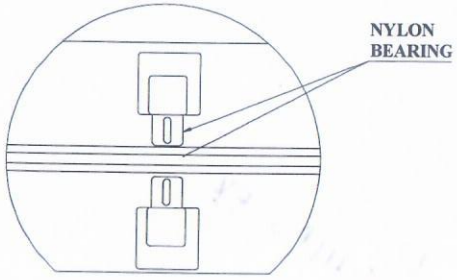


POST 3 & NYLON
ROLLER ASM

DETAIL D1
SCALE 1 : 5

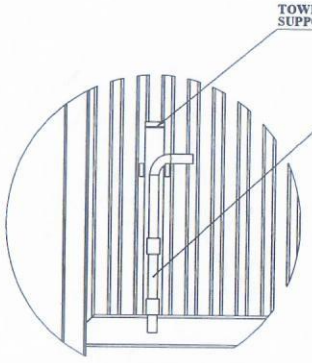

TOWER BOLT LOCKING
ARRANGEMENT

DETAIL D
SCALE 1 : 8

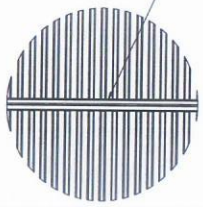

DETAIL I
SCALE 1 : 17

NOTE :

1)GA DRAWING SINGLE SLIDING GATE TYPE NO 05.
2)Total column -04 (A1,B1,C1,D1)
3) 03 column posts when the gates is in the closed position.(A1,B1,C1)
4) 03 column posts when the gates is in the fully open position.(B1,C1,D1)
5) barbed wire design is zigzag pattern.

GA DRAWING TYPE 05