



Date- 13/10/2017.

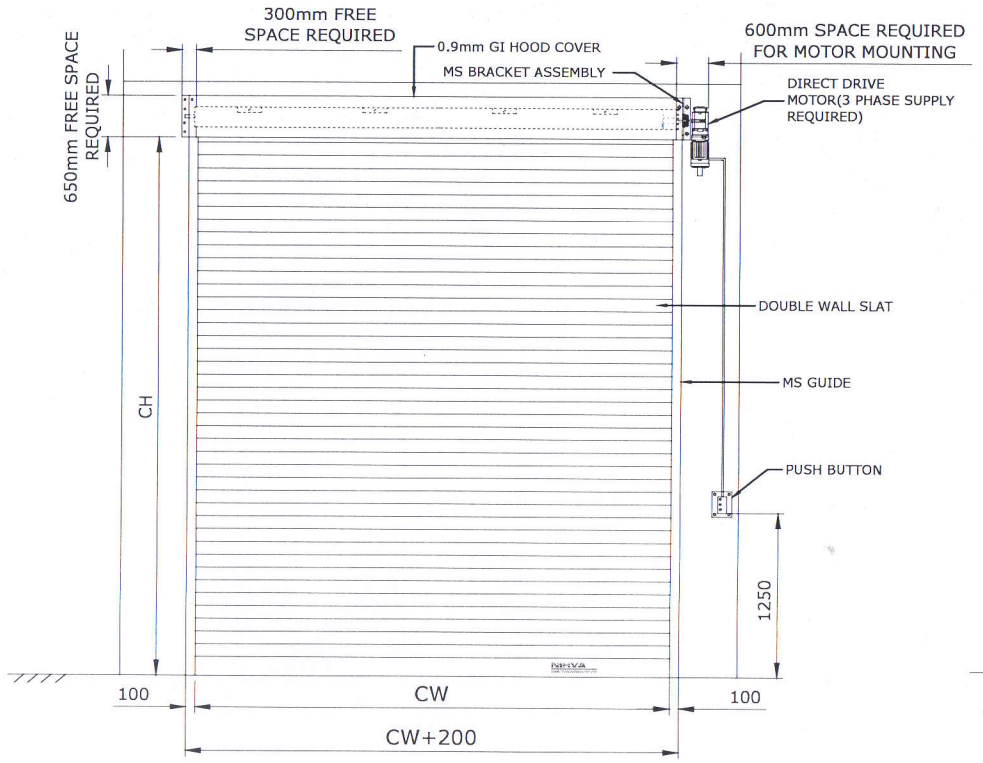


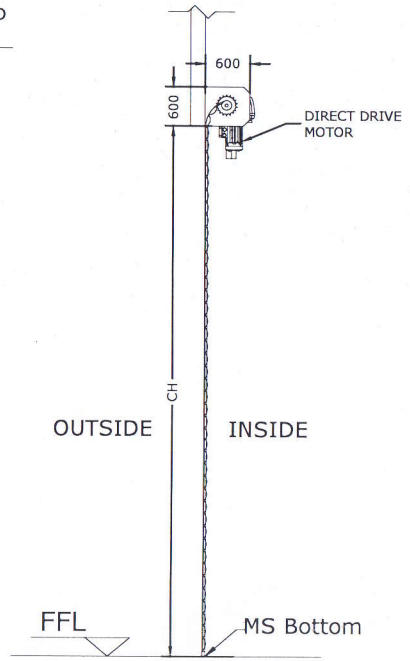

Section A-A

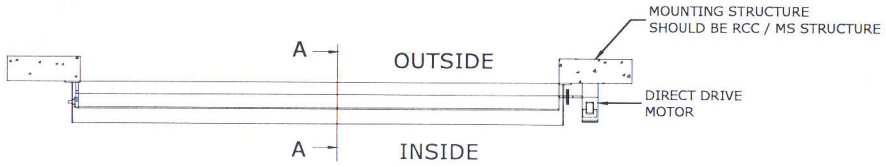

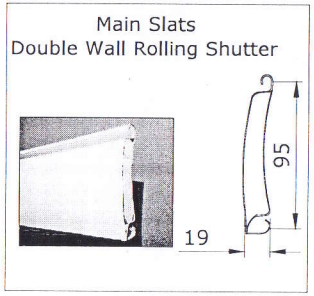

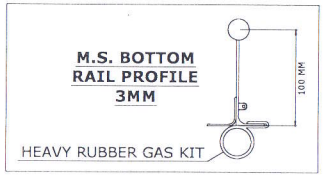

RS1 - 2500×3000 - Media 1.
Right side motor.

CLEAR WIDTH (CW)	CLEAR HEIGHT (CH)	QUANTITY
2000 mm	3000 mm	2 NOS
2500 mm	3000 mm	1 NOS

RAL 9001

COLOR OF SLATS & SHUTTER -RAL9002 (GRAY WHITE)

DIMENSION :		
CLEAR WIDTH	CLEAR HEIGHT	QUANTITY
2000 mm	3000 mm	2 NOS
2500 mm	3000 mm	1 NOS
MATERIAL :		
THICKNESS :		

NOTE:-
1. STRUCTURE FOR SHUTTER FOR SHUTTER WILL BE IN CLIENT'S SCOPE.
2. 3 PHASE SUPPLY SHOULD BE PROVIDED.

NIHVA TECHNOLOGIES PVT. LTD.
NIHVA TECHNOLOGIES PVT. LTD. PUNE
Email:- info@nihva.com
Website:- www.nihva.com

TITLE:
DOUBLE WALL ROLLING SHUTTER

CLIENT'S APPROVAL :


CLIENT - DHOOT BUILDERS		
PROJECT -SKODA AUTO IND.PVT.LTD		
SITE LOCATION - AURANGABD		
DWG. NO. : NIHVA/17-18/0219		
SCALE: NTS	WT:	SHEET:1 OF 1
DRAWN BY: OMKAR		DATE: 27-09-2017
CHECKED BY: SHEKHAR		DATE: 27-09-2017
APPROVED BY : SHEKHAR		DATE: 27-09-2017


If any queries contact : projects@nihva.com

NOTE: ALL DIMENSIONS ARE IN mm


RS2 - 2×3 - a. Test cell technical Floor - Right side motor.
b. media 1 - Right side motor mountings.


Date - 13/10/2017.

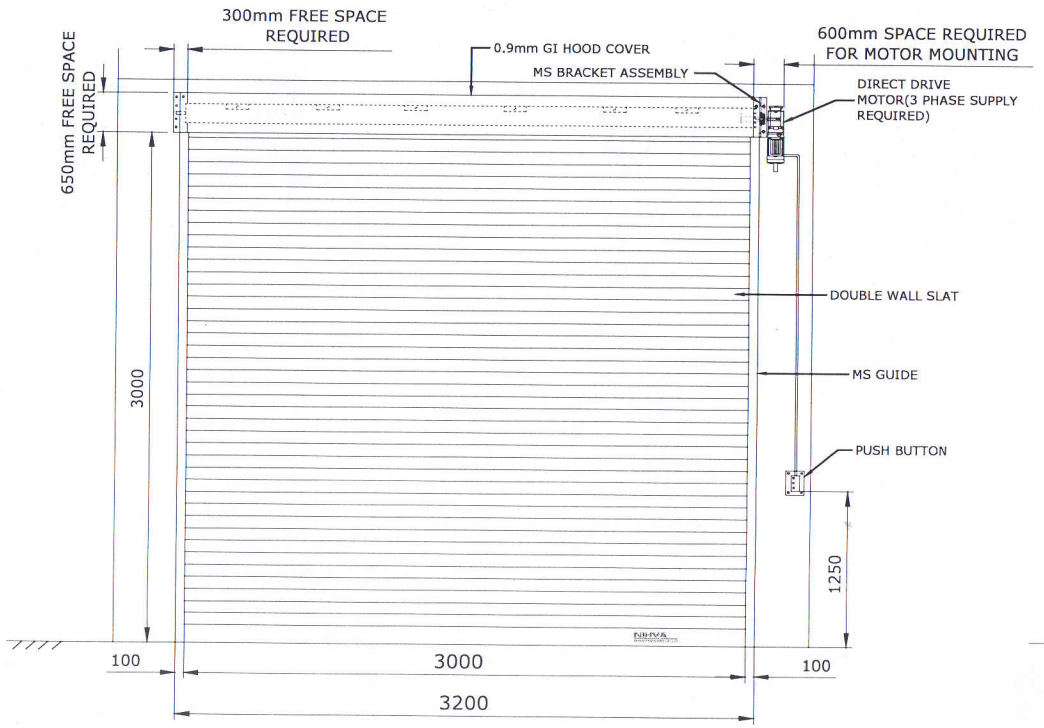


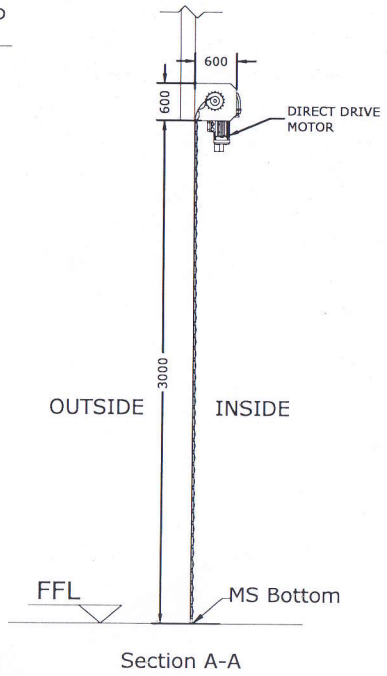

Section A-A

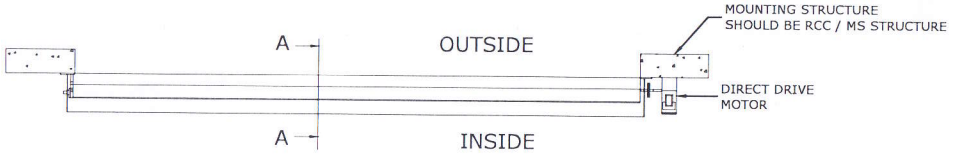

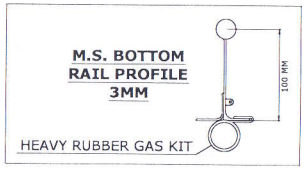

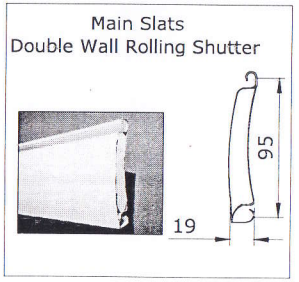

RS1 3x3 - Electric room Right side motor space available.

RAL 9001

COLOR OF SLATS & SHUTTER -RAL9002 (GRAY WHITE)

CLEAR WIDTH (CW)	CLEAR HEIGHT (CH)	QUANTITY
3000 mm	3000 mm	2 NOS

DIMENSION :		
CLEAR WIDTH	CLEAR HEIGHT	QUANTITY
3000 mm	3000 mm	2 NOS

MATERIAL :

THICKNESS :

NOTE:-

1.STRUCTURE FOR SHUTTER FOR SHUTTER WILL BE IN CLIENT'S SCOPE.
2. 3 PHASE SUPPLY SHOULD BE PROVIDED.

NIHVA
NIHVA TECHNOLOGIES PVT. LTD.
NIHVA TECHNOLOGIES PVT. LTD. PUNE
Email:- info@nihva.com
Website:- www.nihva.com

TITLE:

DOUBLE WALL ROLLING SHUTTER

CLIENT'S APPROVAL :

CLIENT - DHOOT BUILDERS	
PROJECT -SKODA AUTO IND.PVT.LTD	
SITE LOCATION - AURANGABD	
DWG. NO. : NIHVA/17-18/0218	
SCALE: NTS	WT: SHEET:1 OF 1
DRAWN BY: OMKAR	DATE: 27-09-2017
CHECKED BY: SHEKHAR	DATE: 27-09-2017
APPROVED BY : SHEKHAR	DATE: 27-09-2017
If any queries contact : projects@nihva.com	
NOTE: ALL DIMENSIONS ARE IN mm	

Right side motor mountings.