


DETAILED FOUNDATION FOR
9M SLIDING GATE

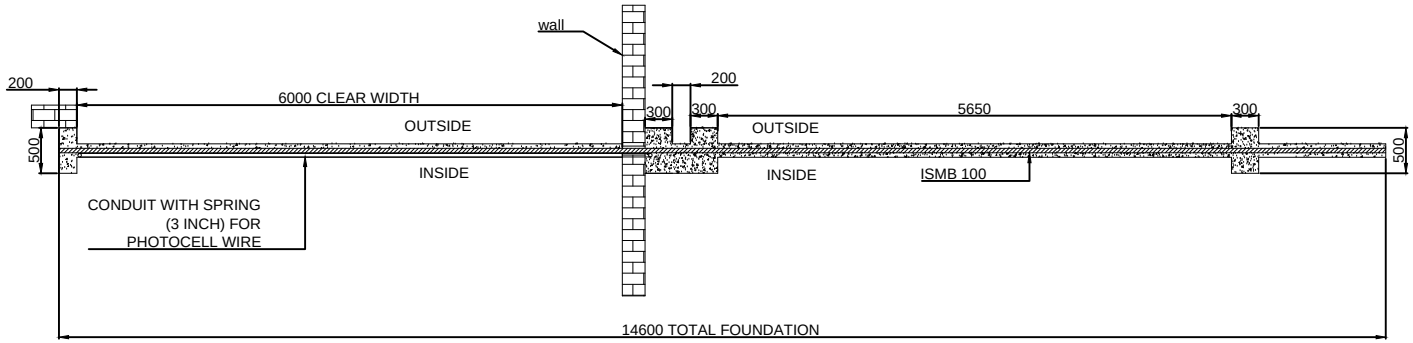

DETAILED FOUNDATION FOR
6M SLIDING GATE

This drawing & design is the property of NIHVA TECHNOLOGIES. Not to be sold or copied to any other concern.

TITLE
DETAILED FOUNDATION FOR
9M & 6M SLIDING GATE

NIHVA TECHNOLOGIES PVT. LTD.
NIHVA TECHNOLOGIES PVT. LTD. PUNE
Tel : 020 66304033
Email:- info@nihva.com
Website:- www.nihva.com

	SIGN	DATE
DRAWN	OMKAR	16/11/17
CHECK	SHEKHAR	16/11/17
REV.		
APPROVAL	SHEKHAR	16/11/17

If any queries contact : design@nihva.com

ALL DIMENSION ARE IN mm

CLIENT - SHILCHAR TECHNOLOGIES LTD.

PROJECT -

SITE - VADODARA

DWG. NO. : NIHVA/17-18/0271 | REV-0

SCALE: NTS | WT: | SHEET: 01 OF 01