


DWG.NO: SALT_1729_FDN_01_R0

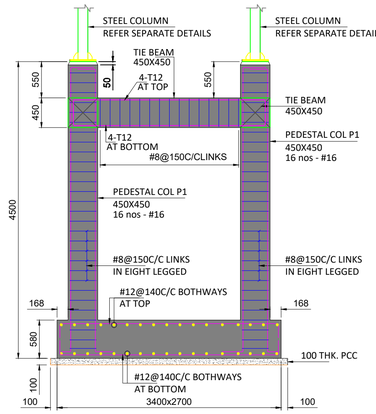


FOOTING & COLUMN REINFORCEMENT DETAIL FC1

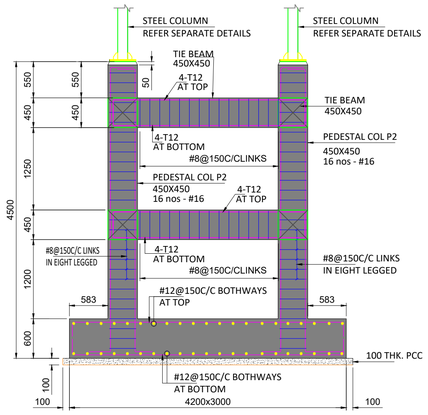

FOOTING & COLUMN REINFORCEMENT DETAIL FC2

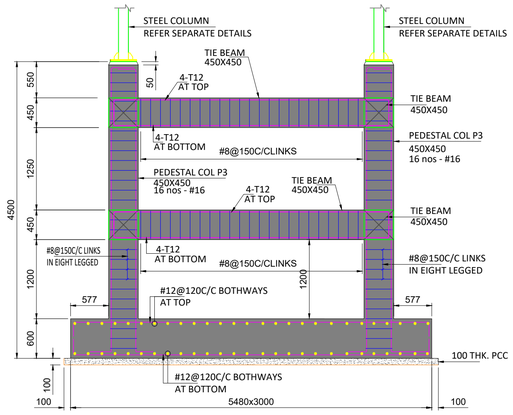


FOOTING & COLUMN REINFORCEMENT DETAIL FC3

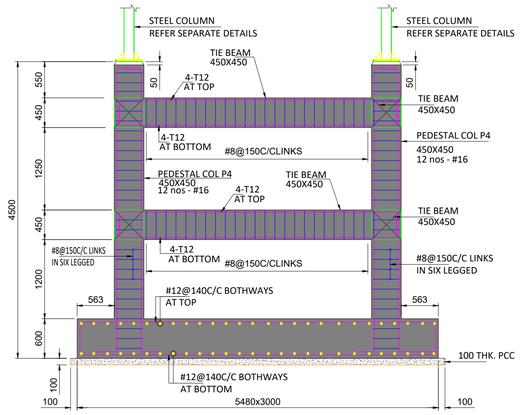


FOOTING & COLUMN REINFORCEMENT DETAIL FC4

SCHEDULE OF COLUMN & FOOTING


		GROUP NO. -FC1	GROUP NO. -FC2	GROUP NO. -FC3	GROUP NO. -FC4
COLUMN / PEDESTAL NO.		P1	P2	P3	P4
PEDESTAL SIZE (b X l)		450 X 450	450 X 450	450 X 450	450 X 450
PEDESTAL STEEL FOOTING TO PLINTH LEVEL.		16 nos - #16	16 nos - #16	16 nos - #16	12 nos - #16
GRADE OF CONCRETE		M25	M25	M25	M25
FOOTING SIZE (L X B)		(2700x3400)	(3000x4200)	(3000x5480)	(3000x5480)
DEPTH	D	580	600	600	600
	d				
BOTTOM STEEL (B/W)		#12 @ 140C/C	#12 @ 150C/C	#12 @ 120C/C	#12 @ 140C/C
TOP STEEL (B/W)		#12 @ 140C/C	#12 @ 150C/C	#12 @ 120C/C	#12 @ 140C/C
GRADE OF CONCRETE		M25	M25	M25	M25

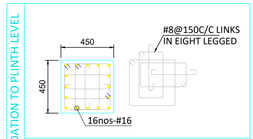

REINFORCEMENT DETAIL
FOR PEDESTAL P1, P2 & P3- 450X450

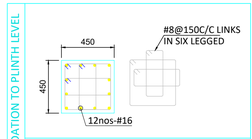


REINFORCEMENT DETAIL
FOR PEDESTAL P4- 450X450

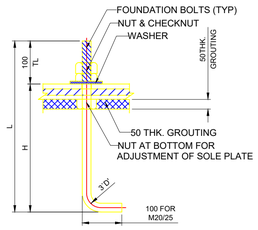


TYPICAL DETAILS OF L-TYPE
BOLTS (EMBEDED)

'L' BOLT DETAILS FOR STRUCTURAL COLUMN

Ø (BOLT DIA)	H(MM)	TL(MM)	L(MM)	COLUMN	TOTAL 'L' BOLTS
20mm 8.8 GRADE	800	100	900	REFER LAYOUT	64
				TOTAL	64

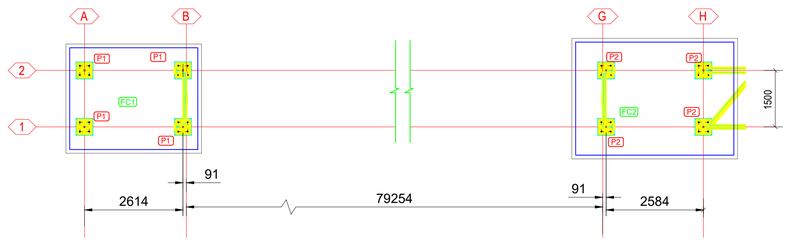

LAYOUT FOR FOUNDATION LEVEL

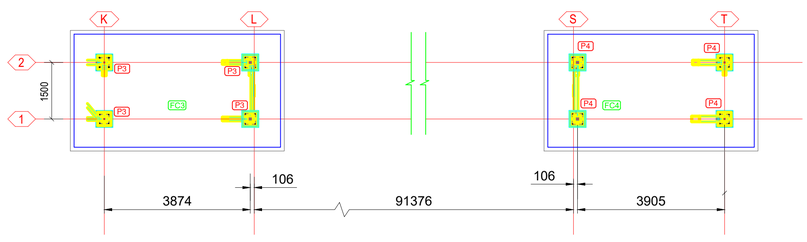

LAYOUT FOR FOUNDATION LEVEL

REV.NO.	DESCRIPTION.	REV.DATE	DRAWN.	CHKD.	APPD.
0	ISSUED FOR APPROVAL	05.11.22	IMS	HAB	HAB

DWG.TITLE :-	FOUNDATION DRAWING FOR DOOR FRAME TRUSS BETWEEN 84M & 99M
PROJECT	MEGADOOR INSTALLATION AT HYDRABAD AIRPORT
CLIENT	GMR
	SALT DESIGN SERVICES — NIHVA TECHNOLOGIES PVT. LTD. PUNE Tel : 020.66304033 Email:- info@nihva.com Website:- www.nihva.com

DRAWN :RRK	CHECKED : HAB	SCALE: 1:100
APPROVED : HAB	JOB CODE. : 1729	DATE: 05.11.2022
DWG.NO: SALT_1729_FDN_01_R0	(SH-1OF1)	REV. - R0 SIZE. - A1

A1 (841 x 594)