

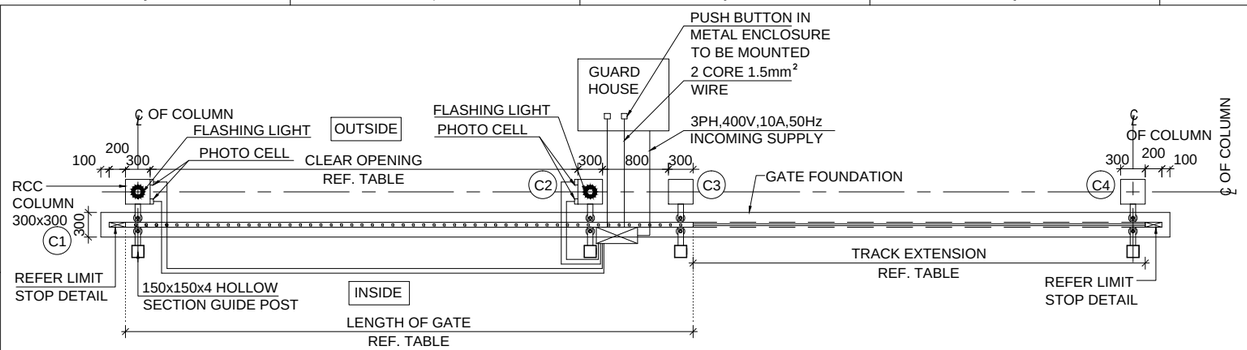




## SLIDING GATE PLAN CLOSED POSITION

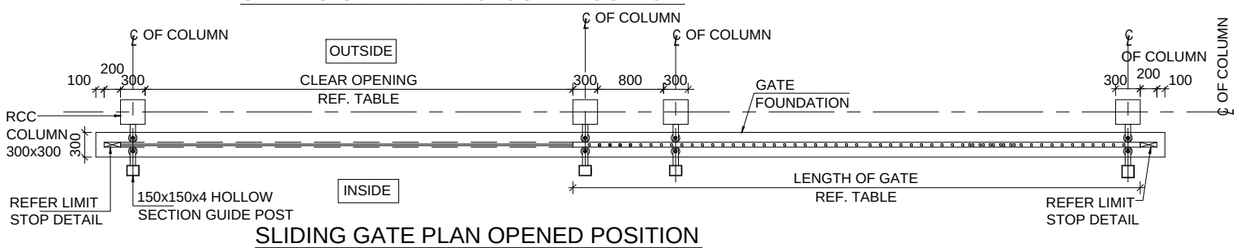



## SLIDING GATE PLAN OPENED POSITION

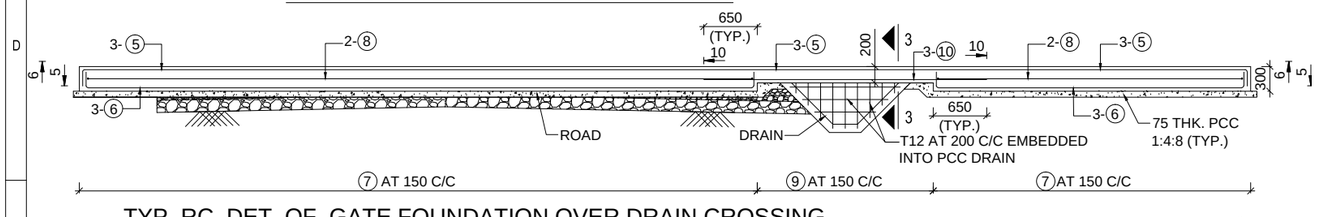




## TYP. RC. DET. OF GATE FOUNDATION OVER DRAIN CROSSING

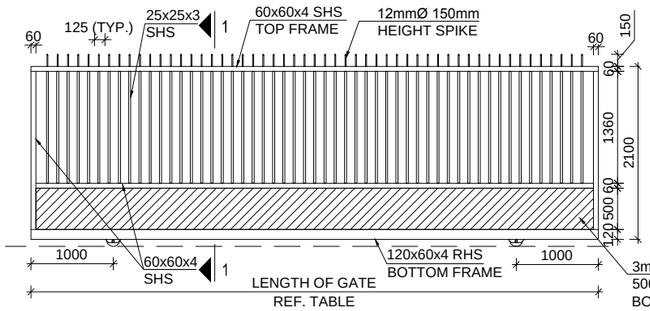



## SLIDING GATE ELEVATION

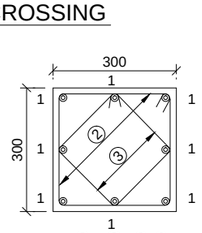

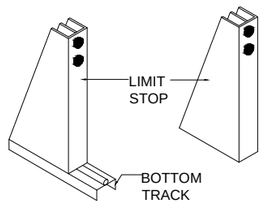


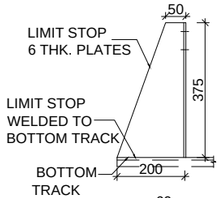
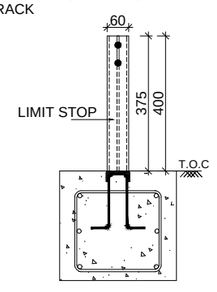
## LIMIT STOP DETAILS


## INPUT TO VENDOR

## SCHEDULE OF SLIDING GATE'S AT GUARD HOUSE

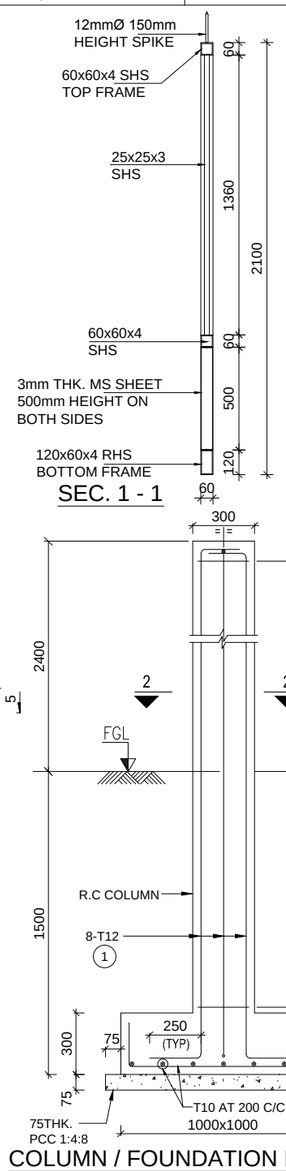
| GATE ID | CLEAR OPENING (mm) | TRACK EXTENSION (mm) | LENGTH OF GATE (mm) | COLUMN LOCATION | | | | T.O.C OF FOUNDATION |
|---|---|---|---|---|---|---|---|---|
| | | | | CENTRE OF COLUMN - C1 | | CENTRE OF COLUMN - C4 | | |
| | | | | NORTH | EAST | NORTH | EAST | |
| 1 | 7500 | 7800 | 9200 | 3178571.779 | 730810.141 | 3178555.079 | 730810.141 | +214.450 |
| 6 | 8800 | 9100 | 10500 | 3178611.231 | 730099.212 | 3178611.231 | 730118.512 | +214.000 |
| 10 | 5800 | 6100 | 7500 | 3178611.231 | 730079.119 | 3178611.231 | 730092.419 | +214.000 |
| 11 | 5800 | 6100 | 7500 | 3178591.871 | 730810.141 | 3178578.571 | 730810.141 | +214.450 |





## COLUMN / FOUNDATION DETAIL

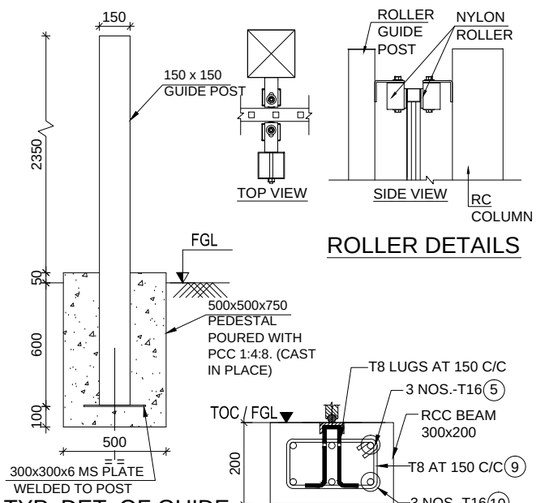


## ROLLER DETAILS

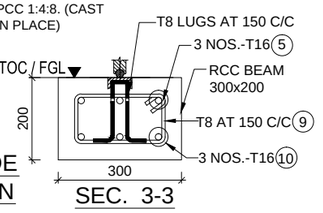


## TYP. DET. OF GUIDE POST FOUNDATION

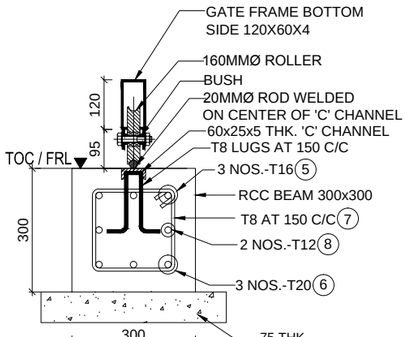


## GATE FOUNDATION DETAILS

## LEGEND:

FGL - FORMED GROUND LEVEL
FRL - FINISHED ROAD LEVEL
SHS - SQUARE HOLLOW SECTION
RHS - RECTANGULAR HOLLOW SECTION
T.O.C - TOP OF CONCRETE

| DESIGNER OF RECORD | |
|---|---|
| JOHN SOLDEEP | 09/02/2015 |
| NAME | DATE |
| L&T CONSTRUCTION | |

| ITR | |
|---|---|
| Rathnavel | 09/02/15 |
| NAME | DATE |

## NOTES:

1. ALL DIMENSIONS ARE IN MILLIMETERS AND LEVELS ARE IN METERS.
2. GRADE OF CONCRETE SHALL BE M35.
3. CLEAR COVER TO REINFORCEMENT SHALL BE 40mm FOR GATE FOUNDATION AND 40mm FOR COLUMN.
4. T-DENOTES HIGH YIELD STRENGTH DEFORMED BAR HAVING YIELD STRENGTH NOT LESS THAN 500 N/sq.mm. CONFORMING TO IS:1786-2008.
5. ALL STRUCTURAL STEEL SECTIONS / PLATES SHALL BE OF GRADE 250 MPA CONFIRMING TO IS: 2062-2006.
6. HOLLOW SECTIONS SHALL BE OF GRADE 310 MPA CONFIRMING TO IS: 4923-1997.
7. FOR LAYOUT OF ROAD, FENCE & GATES REFER DWG. NO. O12205-C-DP-03-RD-0010 & 0011, O12205-C-DP-03-RD-0023 TO 0028, O12205-C-DP-03-RD-0044 TO 0073.
8. FRL / FGL SHALL BE LOCALLY MATCHED WITH T.O.C OF FOUNDATION .
9. DETAILS SHOWN ARE FOR PREPARING SHOP DWG. WHICH MAY SUBJECT TO CHANGE AS PER VENDOR STANDARD DETAIL IN CONSULTATION WITH CLIENT.

| CHECKED BY | SIGN | DATE | CHECKED BY | SIGN | DATE | CHECKED BY | SIGN | DATE |
|---|---|---|---|---|---|---|---|---|
| ARCHITECTURE | | 09.02.15 | HVAC | | 09.02.15 | GIS | | |
| CIVIL & STRUCTURAL | | 09.02.15 | FPS | | 09.02.15 | GEOTECH. | | |
| ELECTRICAL | | 09.02.15 | PIPING | | | | | |
| ELV SYSTEM | | 09.02.15 | PHE | | 09.02.15 | | | |

US Army Corps of Engineers®
ALASKA DISTRICT

| MARK | DESCRIPTION | DATE | APPR. |
|---|---|---|---|
| D | ISSUED FOR 100% FORMAL SUBMISSION | 09.02.2015 | RBS |
| C | ISSUED FOR 100% FORMAL SUBMISSION | 15.10.2014 | RBS |
| B | ISSUED FOR 100% APPROVAL | 25.06.2014 | SB |
| A | ISSUED FOR 95% APPROVAL | 21.04.2014 | SB |

This drawing is the property of L&T Construction. B&F-EDRC and must not be passed on to any person or body not authorised by us to receive it nor be copied or otherwise made use either in full or in part by such person or body without our prior permission in writing.

| | | | |
|---|---|---|---|
| DSGN. BY: | PAKR | 10.04.2014 | |
| DRWN BY: | MSRK | 10.04.2014 | |
| CHKD BY: | RJS | 15.04.2014 | |
| APPD BY: | SB | 21.04.2014 | |
| REV: D | RELEASED FOR: CLIENTS APPROVAL | PLOT SCALE: N.T.S | |
| SIZE: A2 | | | |

PRIME CONTRACTOR:
BOEING INTERNATIONAL CORPORATION INDIA PVT. LTD

L&T Construction Buildings & Factories

PROJECT: C-17 BEDDOWN FACILITIES- HINDAN AFS
TITLE: EXTERNAL DEVELOPMENT NUM. & RC. DETAILS OF MOTORIZED SLIDING GATES AT GUARD HOUSES

DRAWING NO. O12205-C-DP-03-NR-0045
REFERENCE NO. 03-C-0045
SHEET OF

FEBRUARY 09, 2015 100%