

DRAWING No.
H6543/TD/1115


DO NOT SCALE

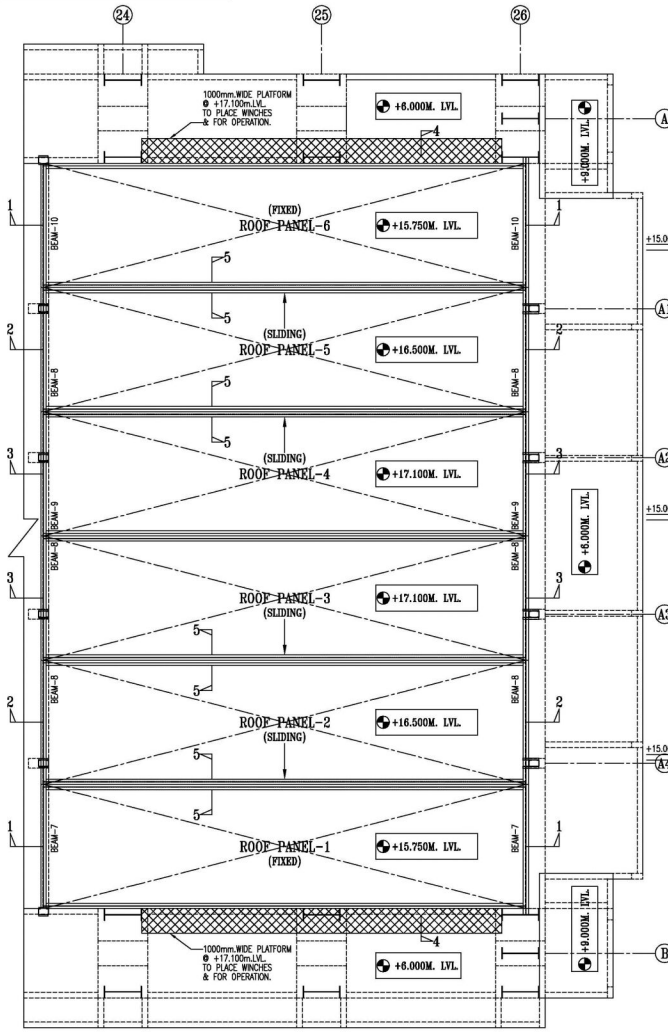


PART PLAN AT BLASTING CHAMBER ROOF LEVEL.(+12.750M.LVL.)
(ROOF PANELS SHOWN IN CLOSED POSITION)

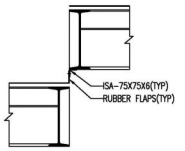


SECTION 5-5

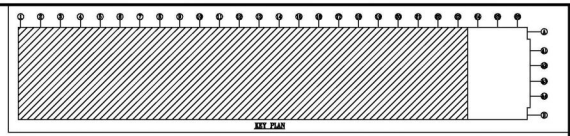


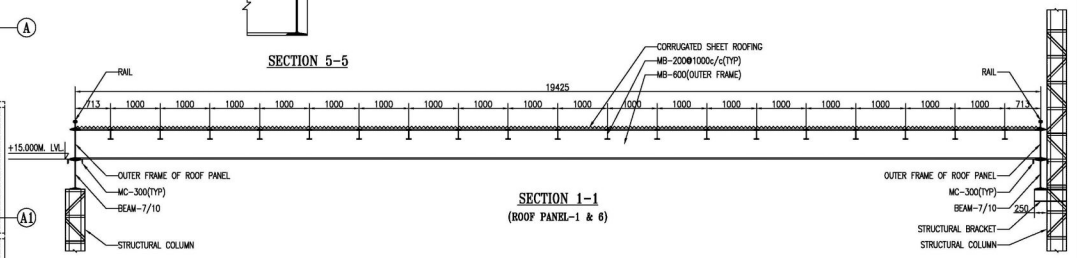


SECTION 1-1
(ROOF PANEL-1 & 6)

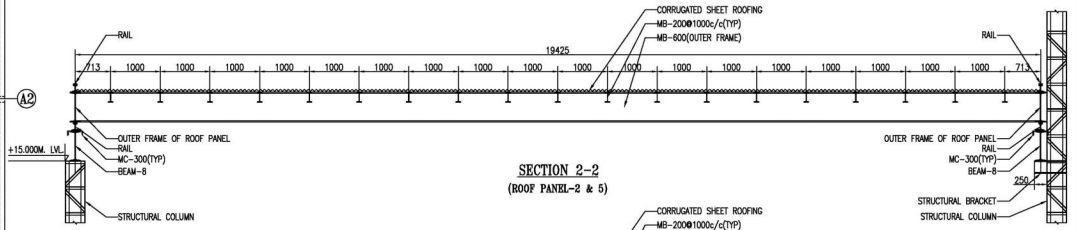


SECTION 2-2
(ROOF PANEL-2 & 5)

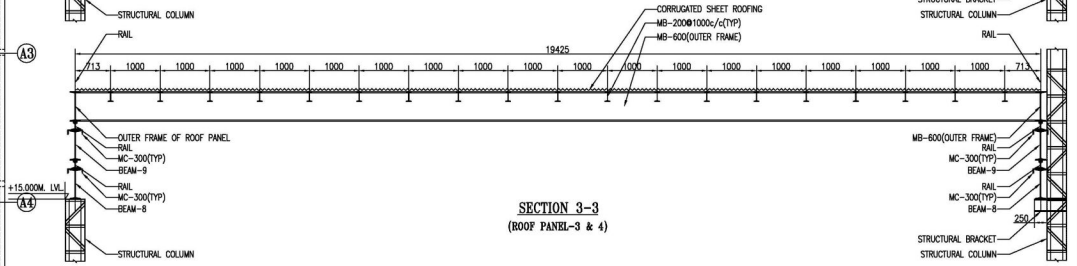

SECTION 3-3
(ROOF PANEL-3 & 4)

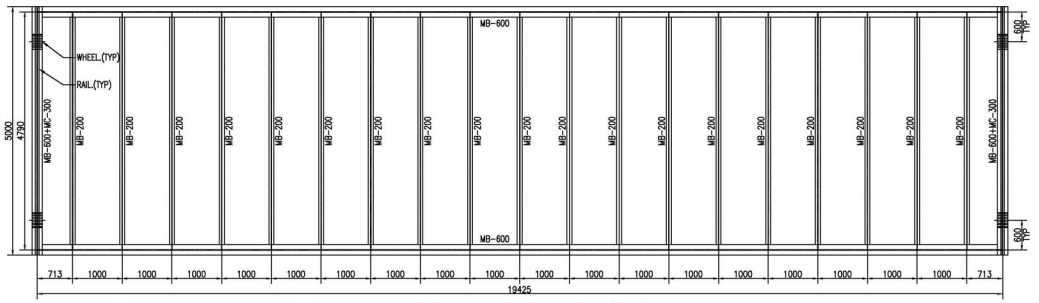

DETAILS OF TYPICAL ROOF PANEL. (PLAN)
(WHEELS ONLY FOR MOVING PANELS)

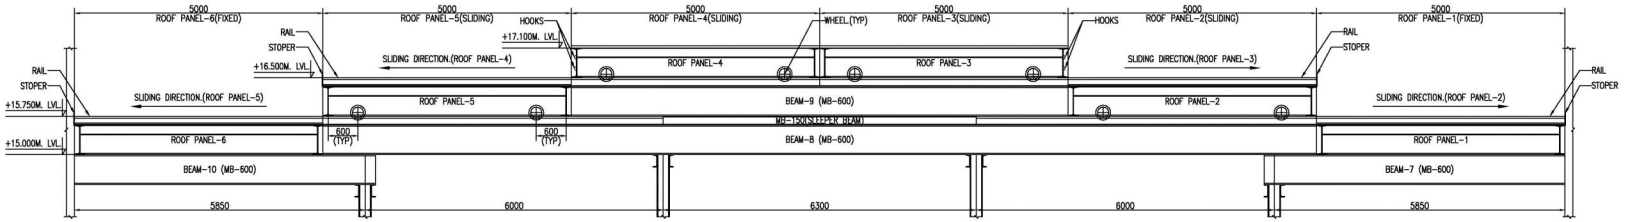

SECTION 4-4

NOTES.

1. ALL DIMENSIONS ARE IN 'mm' & LEVELS ARE IN 'm'.
2. THIS DRAWING IS TO BE READ IN CONJUNCTION WITH RELEVANT ARCHITECTURAL AND STRUCTURAL DRAWINGS.
3. FOR GENERAL NOTES & TYPICAL DETAILS REFER DRG. NO.H6543/TD/0001 TO 0004
4. FOR OTHER DETAILS, REFER LIST OF DRGS. IN DRG. NO.H6543/TD4001
5. SIZES INDICATED IN DRAWING ARE TENTATIVE

METHORD OF OPERATION.

1. SEQUENCE OF SLIDING OPERATION SHALL BE AS FOLLOWS.
   a). PANEL-4 TO SLIDE ABOVE PANEL-5
   b). PANEL-3 TO SLIDE ABOVE PANEL-2
   c). PANEL-4 & 5 TOGETHER TO SLIDE ABOVE PANEL-6
   d). PANEL-3 & 2 TOGETHER TO SLIDE ABOVE PANEL-1
2. SLIDING MOVEMENT WILL BE BY WINCHES MOUNTED ON PLATFORM AT BOTH SIDES. HOOKS ARE PROVIDED TO PANELS-3 & 4 TO FACILITATE ATTACHMENT TO WINCH.
3. CARE SHOULD BE TAKEN TO ENSURE THAT PANELS-3 & 4 ARE NOT TO BE MOVED WITHOUT PANELS-2 & 5 AT THEIR POSITION. (HENCE HOOKS ARE NOT PROVIDED TO PANELS-2 & 5)

This drawing is Copyright ©
Document Produced by dealsPDF Unregistered :: http://www.docudeals.com