


3170 L
QTY - 3

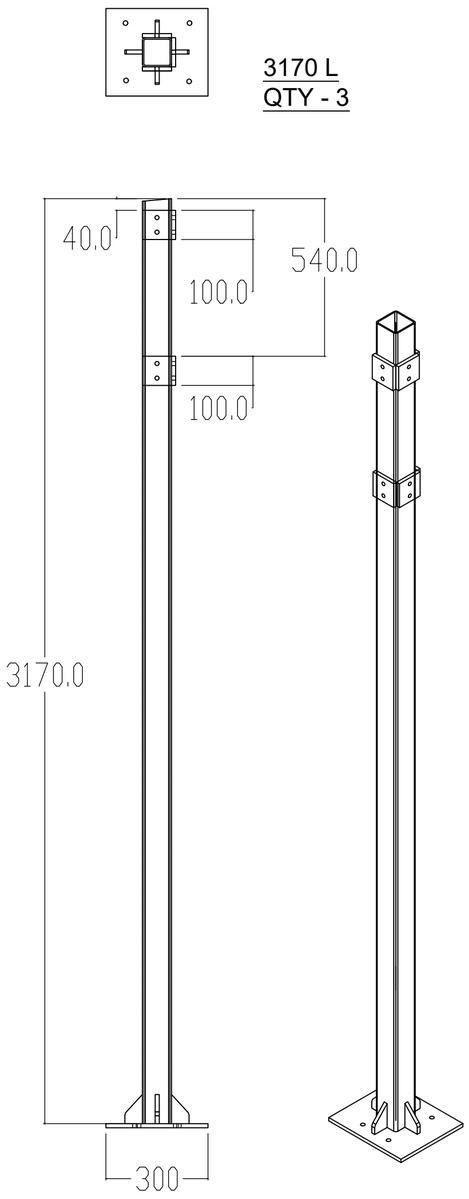


3350 L
QTY - 5

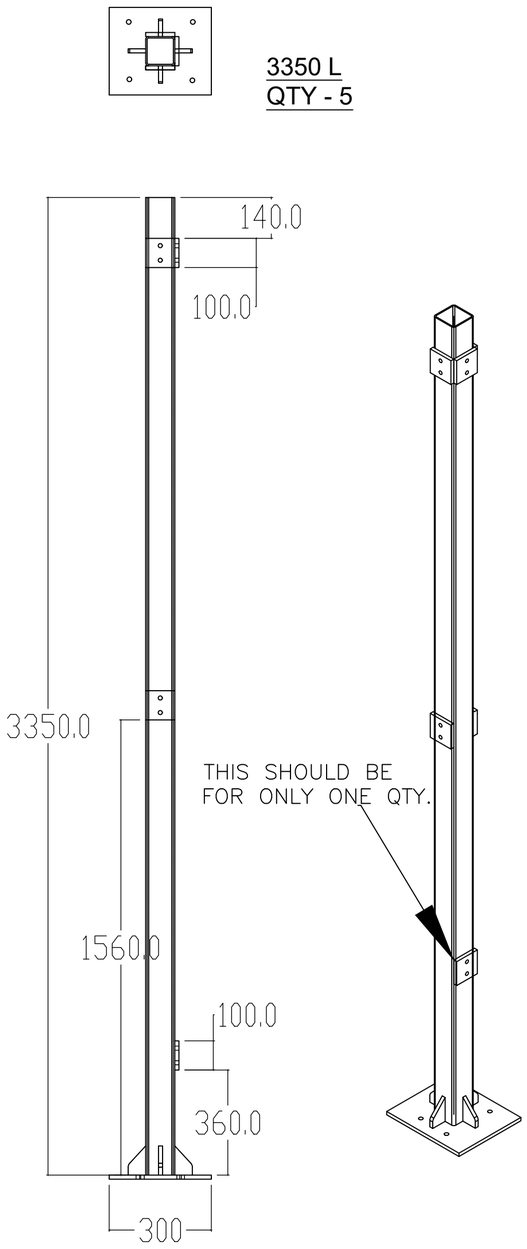

4550 L
QTY - 3

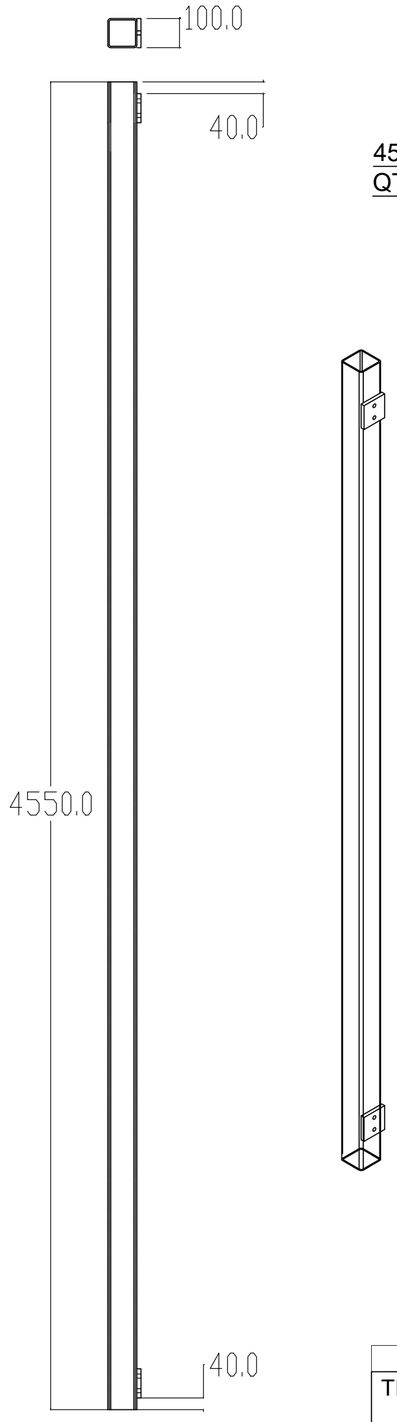

3110 L
QTY - 1

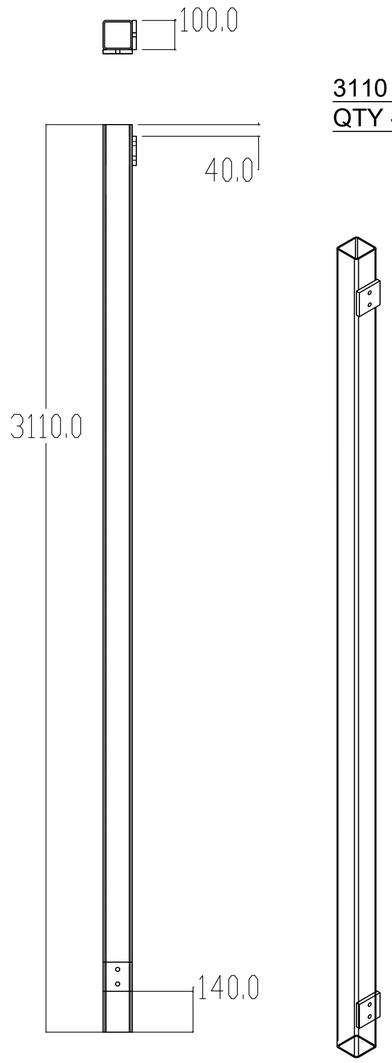

REV NO.	DESCRIPTION	Date	Revised By

TITLE:- SQ TUBE WELDG DWG - 1				NIHVA TECHNOLOGIES PVT. LTD. PUNE Tel : 020 66304033 Email:- info@nihva.com Website:- www.nihva.com	
	NAME	DATE	SIGN		
DRAWN	MAHESH S.	22/10/22		CLIENT - NIHVA TECHNOLOGIES PVT.LTD	
CHECK	MAHESH S.	22/10/22		LOCATION -	
APPRD.	VIJAY T.	22/10/22		PRODUCT: FIX & RETRACTABLE ROOF	
If any queries contact : design@nihva.com				DWG NO:-NIHVA/22-23/MFG/0048	REV- 0
ALL DIMENSION ARE IN mm				SCALE: NTS	SCALE:-- 1:1 SHEET: 01 OF 01